

ID Plans Mall

Produced for:
**Property
Management**



Basic



Dimensions



Dumpster



Electric



Emergency Response



Fire



Gas



HVAC



Irrigation



Landscape



Lighting



Location



Parking



Pavement



Pylon Sign



Roof



Signage



Space



Storm



Water



Owner's Manual – Section Overview



Provides general information on the property, generally not found elsewhere, such as loading docks, fences, mailboxes, bollards, and tenant mailboxes.



Provides building width and exterior dimensions to scale.



Identifies the locations and sizes of dumpsters, together with the name of the dumpster companies and the locations of all trash cans.



Identifies the location of all electric meters, the units they operate and the meter numbers. It also locates outside receptacles, phone booths and telephone numbers.



A compilation of the electrical, fire and water site plans, for quick, easy-access in case of any emergency situation.



Identifies the locations of all fire hydrants, risers, valves, and fire riser rooms if present. Will also identify fire sprinkler zones if information is provided.



Identifies the locations of all gas meters, the units they operate. It also identifies the gas company name and the contact numbers.



Identifies the manufacturer, model & serial numbers, and locations for all HVAC units.



Identifies the locations of all the valves and the zones they operate. It details underground wire tracking, timer locations and type, as well as what the water source is.



Identifies greenscape from hardscape. Locates and provides approximate shape of each bed and green areas.



Basic



Dimensions



Dumpster



Electric



Emergency Response



Fire



Gas



HVAC



Irrigation



Landscape



Lighting



Location



Parking



Pavement



Pylon Sign



Roof



Signage



Space



Storm



Water





Owner's Manual – Section Overview



Identifies all under-canopy and parking lot lighting. It separates tenant operated from owner operated lighting and details the location, type, and voltage of each light. Furthermore it also identifies meters, photo-cells, contactors, and timers.



Identifies the exact geographic location of the property. Contains the physical address with the zip code, including a macro and micro view.



Details the total number of spaces and identifies all disabled spaces and ramps. It also locates speed bumps, humps, and striping



Identifies all pavement markings including handicap spaces, directional arrows, stop lines, crosswalks, fire lanes, etc.



Provides photos and overall measurements for pylon signs and monuments signs, as well as the panel sign measurements.



Identifies any equipment/features on the rooftop of the property such as vents, hot stacks, pitch pockets, etc. (This information is to be provided by the customer at the time of the survey.)



Identifies every sign on the property, its location, and verbatim the wording on each sign.



This page identifies the size and quantity of catch basins, as well as location of storm drains and spillways.



Identifies the location of each apartment/garage/mailbox numbers and the square footage of the unit.



Identifies the location of water meters, the units they operate and the meter numbers. It also identifies hose bibs, zurn fittings, water shut-offs and back-flow preventers.



...excellence by design!

ID Plans Corp.
1035 E. Brandon Blvd.
Brandon, FL 33511
www.idplans.com

Tel: (813) 657 2545
Fax: (813) 655 9370

ID Plans Mall

100 Park Plaza Drive
Daly City, CA 94015


682,352 Square Feet



The blank site plan is provided as a tool for the property manager to generate mark-ups or to fax to contractors.

Blank


Page 1 of

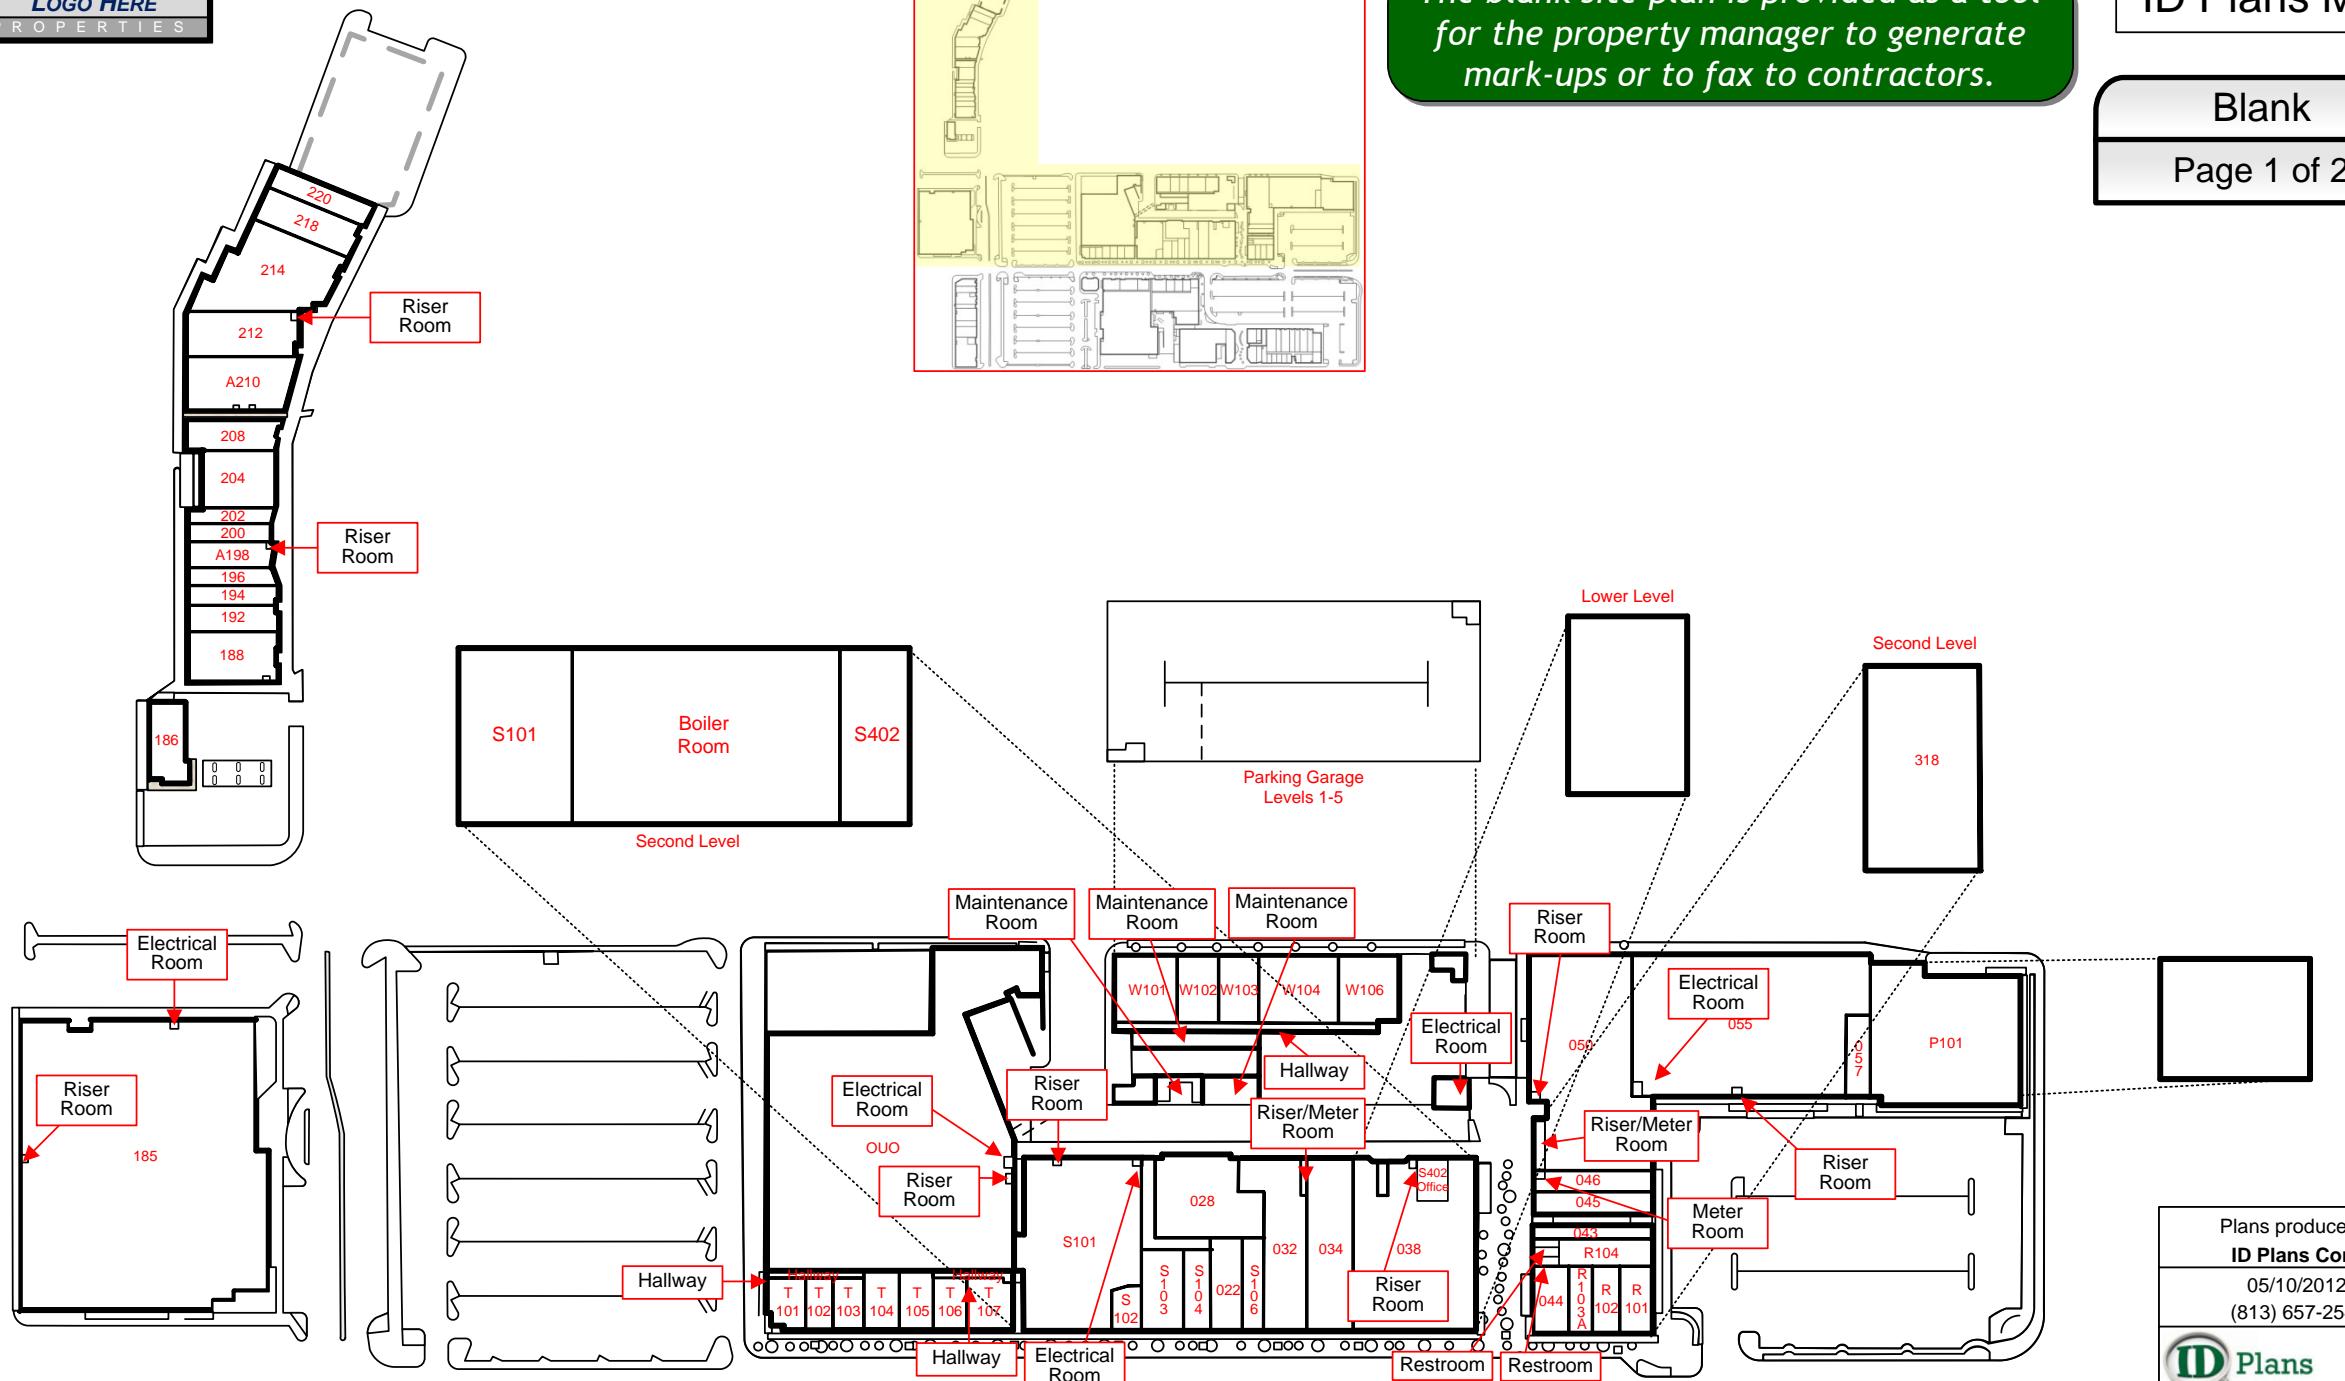

Plans produced by:
ID Plans Corp
05/10/2012
(813) 657-2545



© 201

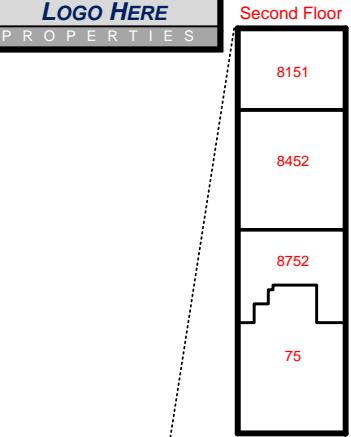


Riser Room

Hallway

Hallway

Hallway

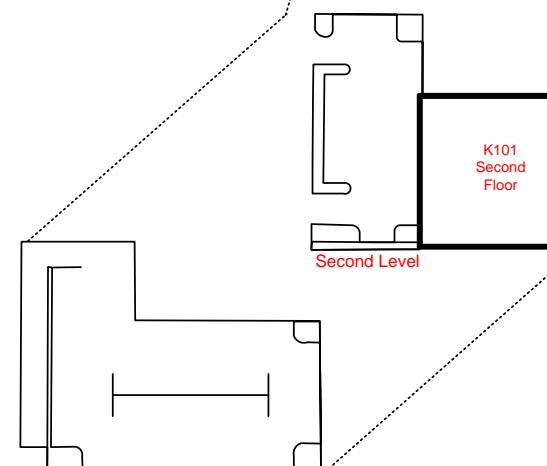

K101
Second Floor

Second Floor

Third Floor

Third Level

The blank site plan is provided as a tool for the property manager to generate mark-ups or to fax to contractors.

ID Plans Mall

Blank

Page 2 of 2

Plans produced by:
ID Plans Corp
05/10/2012
(813) 657-2545



© 2012



The basic site plan provides general information on the property typically not found elsewhere, such as loading docks, fences, railings, mailboxes, flag poles, freezers and bollards.


	Bench		Concrete Dumpster Enclosure		Gas Pump		Service Loading Ramp		Wooden Fence
	Bike Rack		Concrete Steps		Ground Level Rollup Door		Single Mailbox		Wrought Iron Fence
	Block Wall		Drinking Fountain		Loading Dock		Speaker		
	Bus Stop		Elevator		Mail Box		Stairs w/Railing		
	Chain Link Dumpster Enclosure		Flag Pole		Newspaper Stand		Table w/ Number of Chairs		
	Chain Link Fence		Fountain		Railing		Umbrella Table w/ Number of Chairs		

Plans produced by:
ID Plans Corp
05/10/2012
(813) 657-2545



© 2012

The basic site plan provides general information on the property typically not found elsewhere, such as loading docks, fences, railings, mailboxes, flag poles, freezers and bollards.

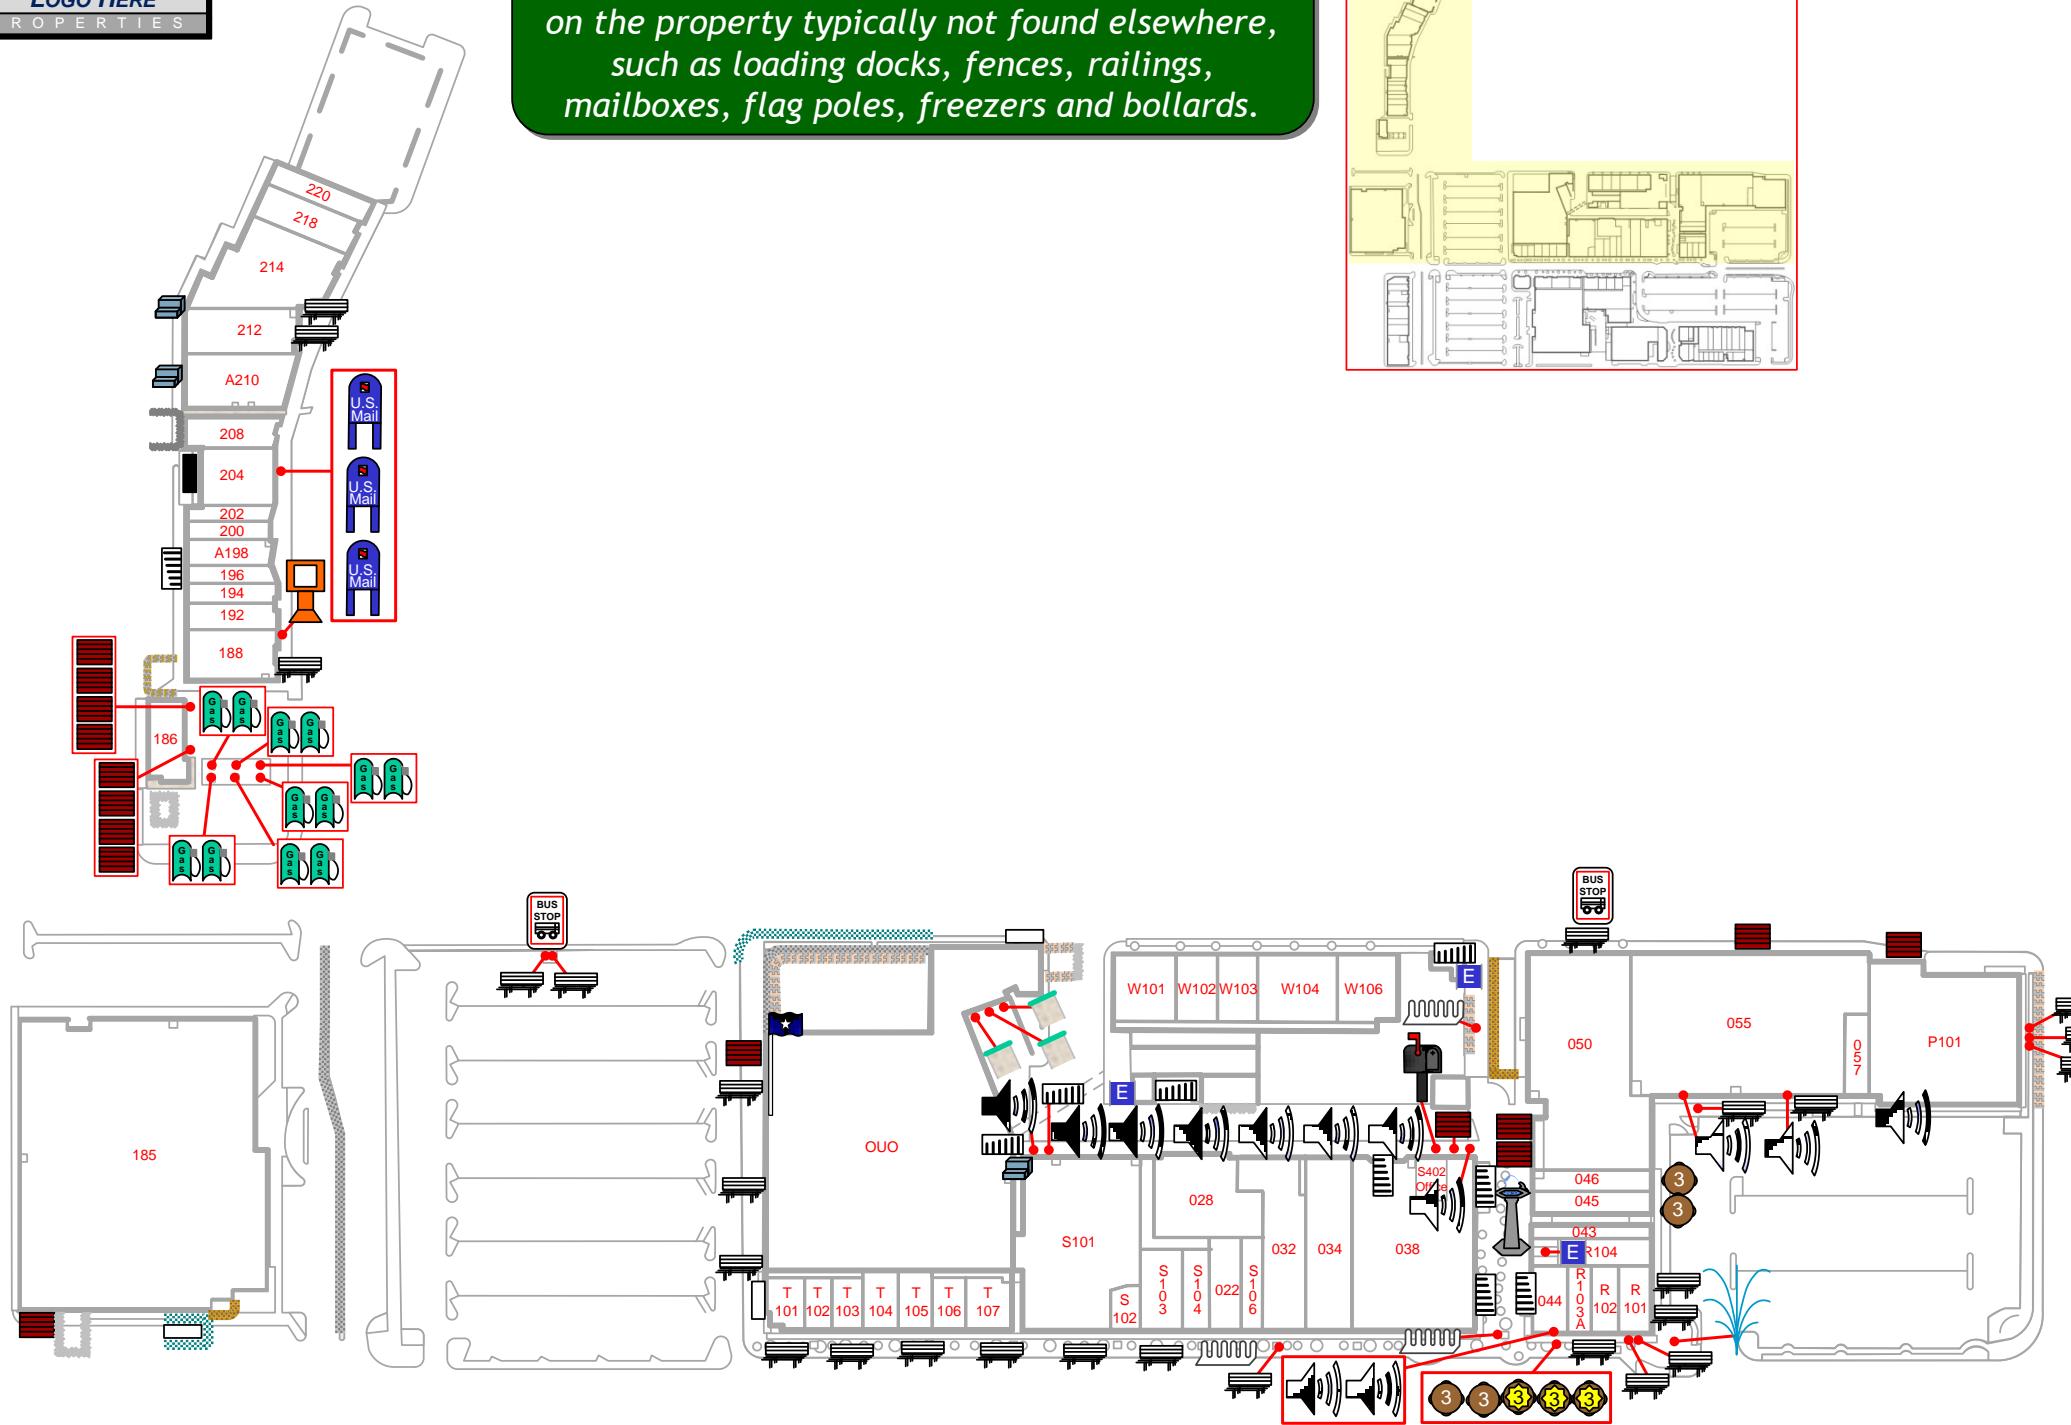


Plans produced by:
ID Plans Corp
05/10/2012
(813) 657-2545




© 2012

The basic site plan provides general information on the property typically not found elsewhere, such as loading docks, fences, railings, mailboxes, flag poles, freezers and bollards.

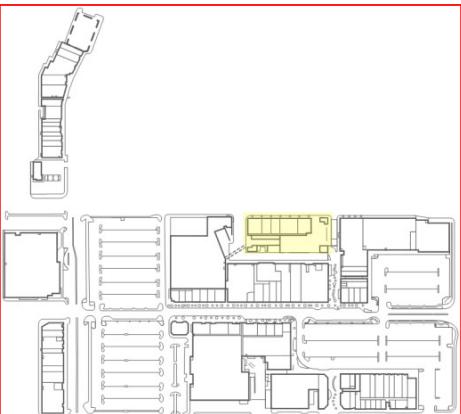


Fifth Level

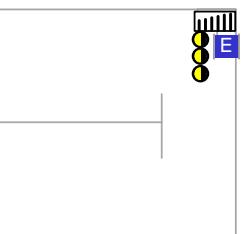


Fourth Level



Third Level

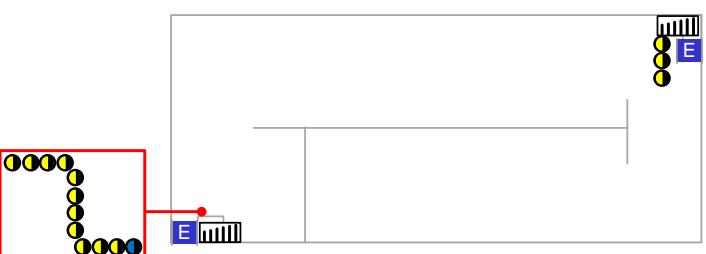

Second Level

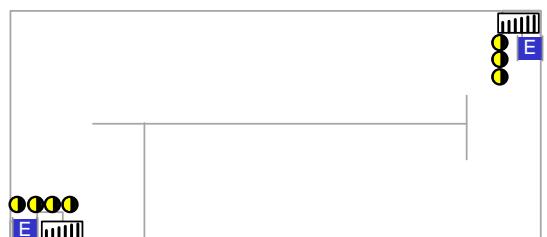

First Level

Plans produced by:
ID Plans Corp
05/10/2012
(813) 657-2545



© 2012

Basic	
Page 3 of 7	
●	Bollard
● ●	Bollards with Railing
-----	Chain Link Fence
E	Elevator
-----	Railing
	Stairs w/Railing



The basic site plan provides general information on the property typically not found elsewhere, such as loading docks, fences, railings, mailboxes, flag poles, freezers and bollards.

	ATM		Chain Link Fence		FedEx Box		Railing		Umbrella Table w/ Number of Chairs
	Bench		Concrete Dumpster Enclosure		Ground Level Rollup Door		Service Loading Ramp		Wrought Iron Fence
	Bike Rack		Concrete Steps		Loading Dock		Speaker		
	Block Wall		Elevator		Mail Box		Stairs w/Railing		
	Bus Stop		Escalator		Picnic Table		Table w/ Number of Chairs		

Plans produced by:

ID Plans Corp


05/10/2012

(813) 657-2545




© 2012



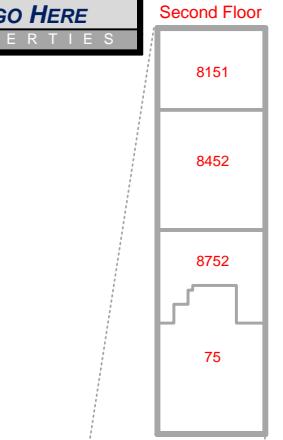

The basic site plan provides general information on the property typically not found elsewhere, such as loading docks, fences, railings, mailboxes, flag poles, freezers and bollards.

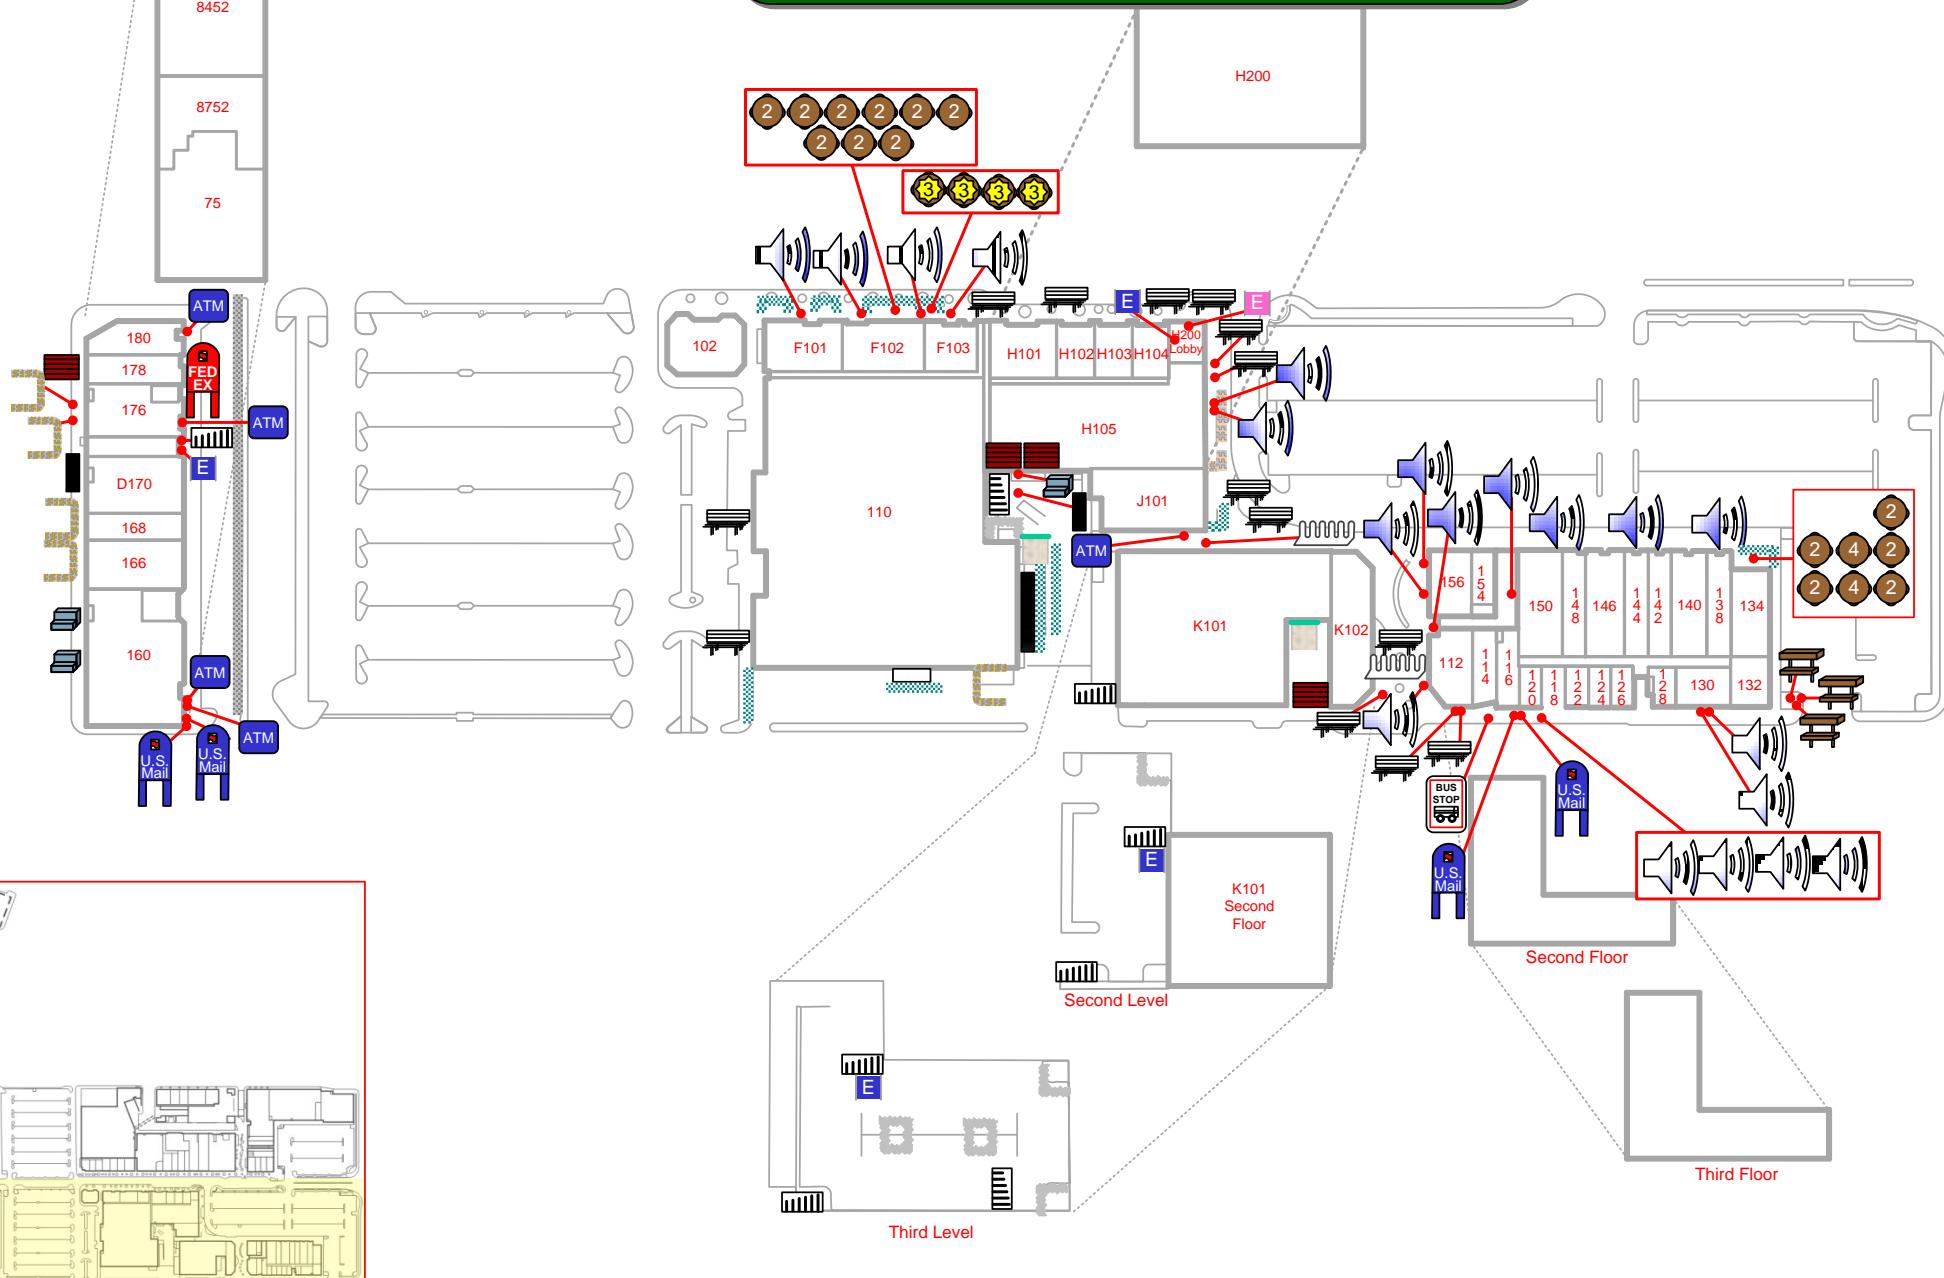


Plans produced by:
ID Plans Corp
05/10/2012
(813) 657-2545



© 2012

The basic site plan provides general information on the property typically not found elsewhere, such as loading docks, fences, railings, mailboxes, flag poles, freezers and bollards.




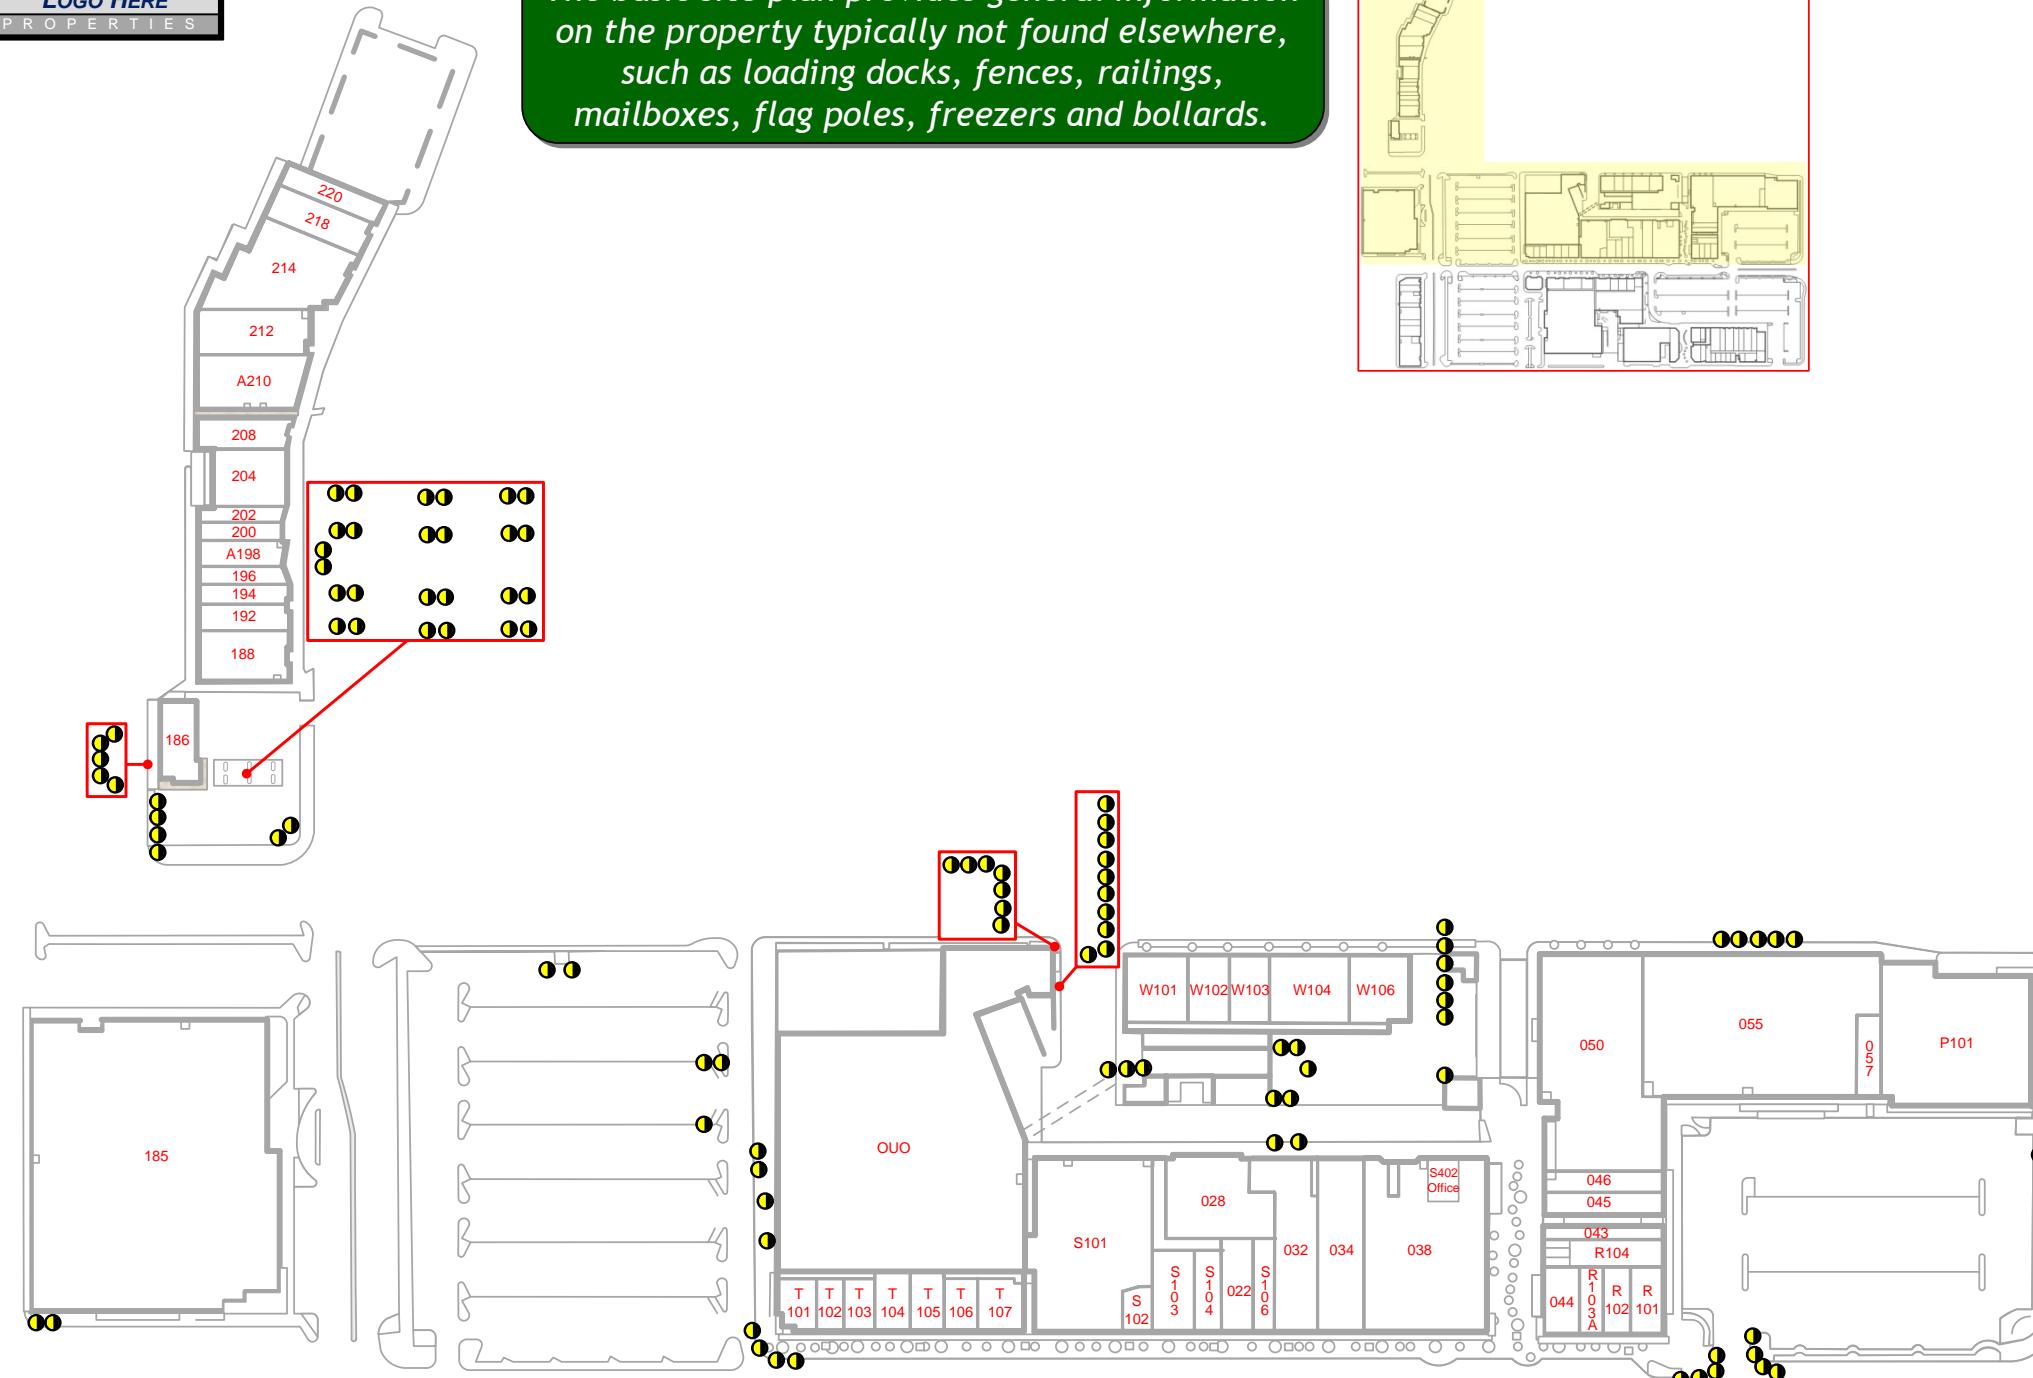


Bollard

Plans produced by:
ID Plans Corp
05/10/2012
(813) 657-2545



© 2012

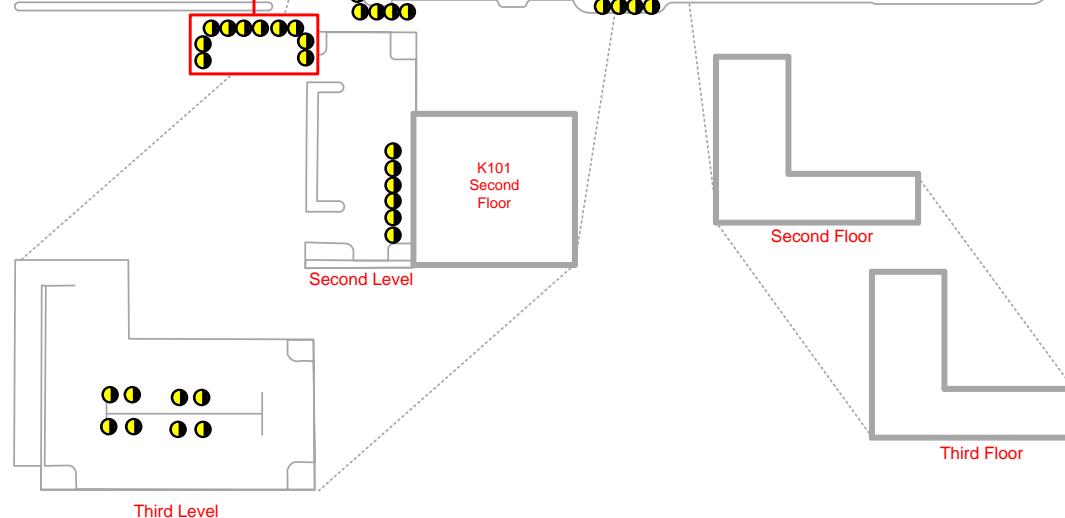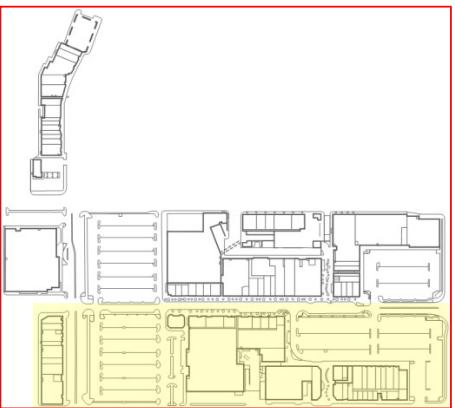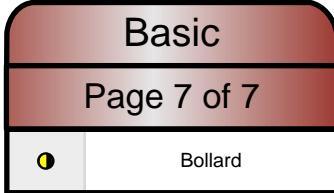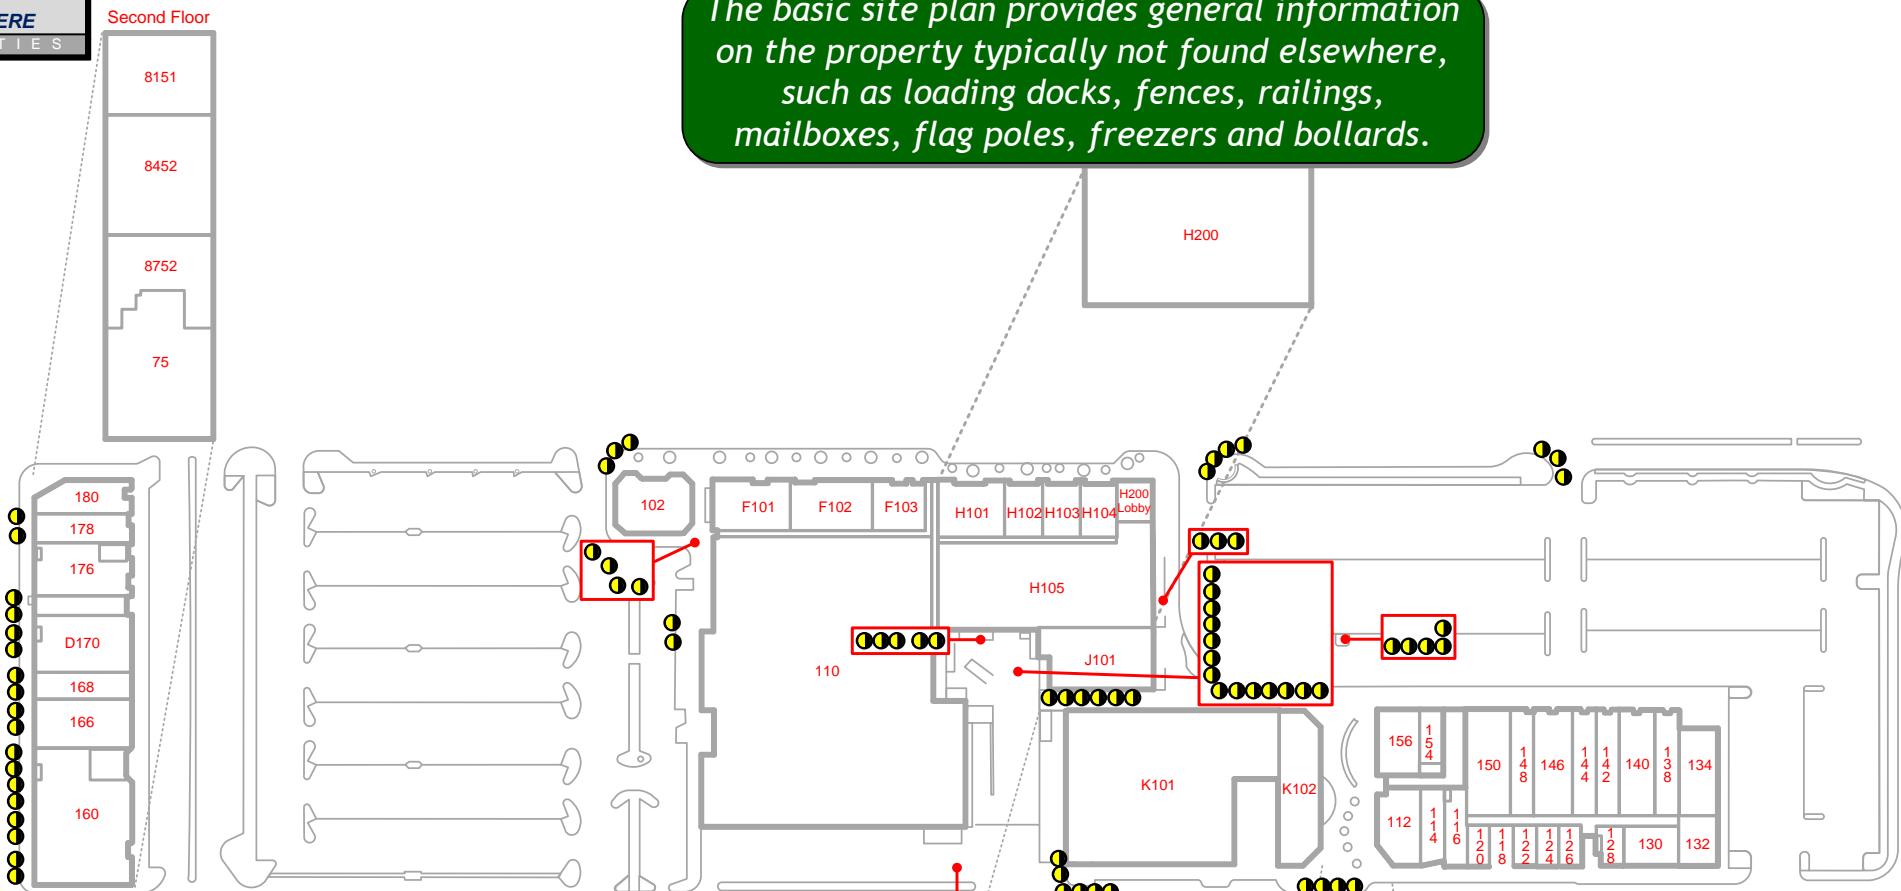


Plans produced by:
ID Plans Corp
05/10/2012
(813) 657-2545



© 2012

This dimensions site plan provides parking lot measurements to scale.





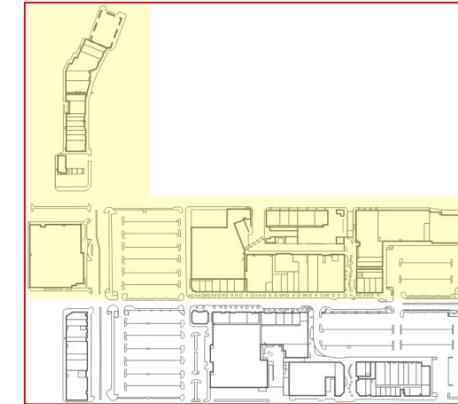


Plans produced by:

ID Plans Corp
05/10/2012
(813) 657-2545



This dimensions site plan provides parking lot measurements to scale.

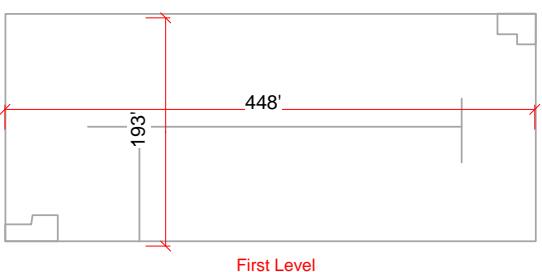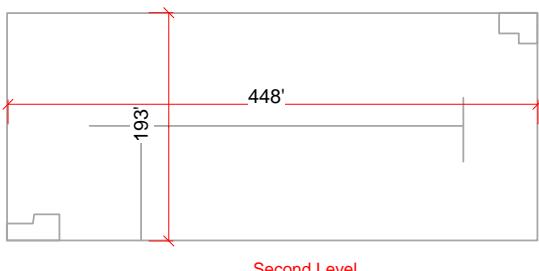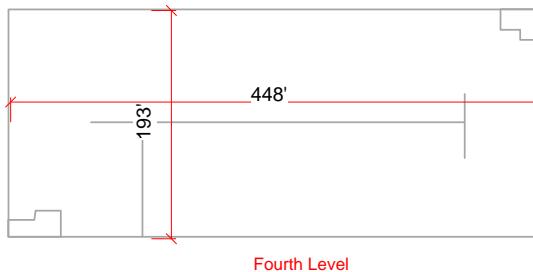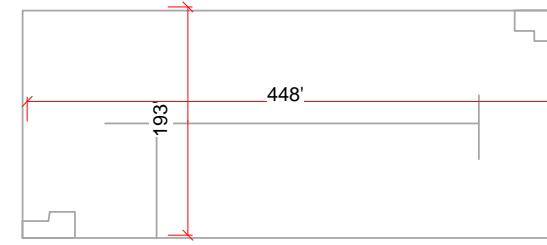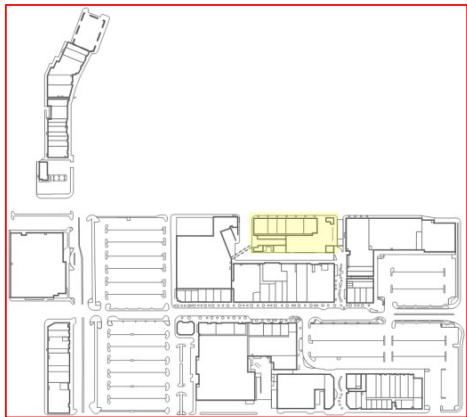

Plans produced by:
ID Plans Corp
05/10/2012
(813) 657-2545








Scale: 1 in =

150ft. 0in.

© 2012



The dimensions site plan provides store front width and exterior dimensions to scale.

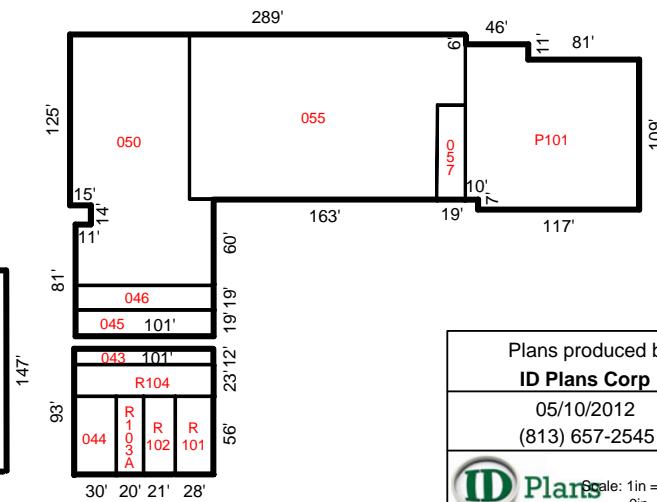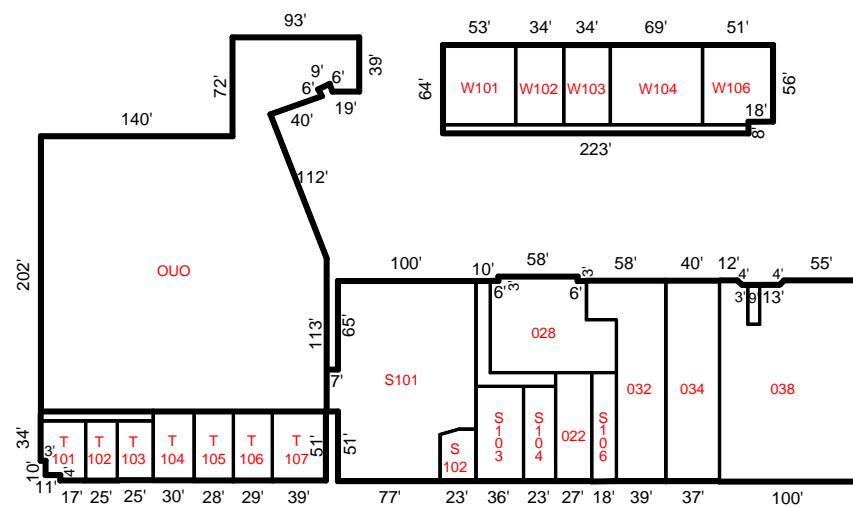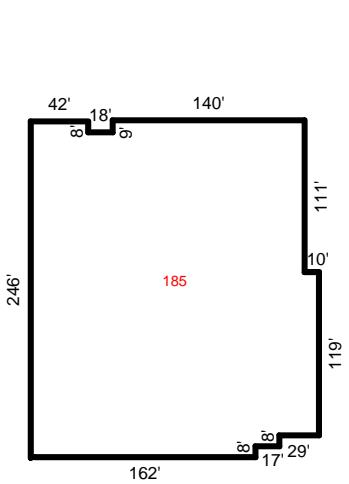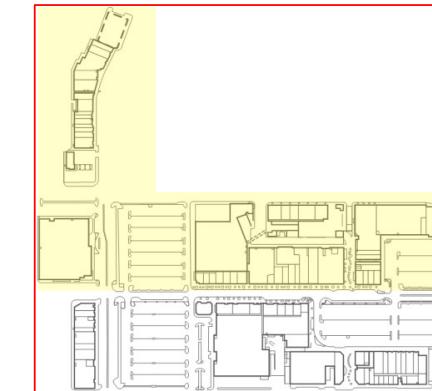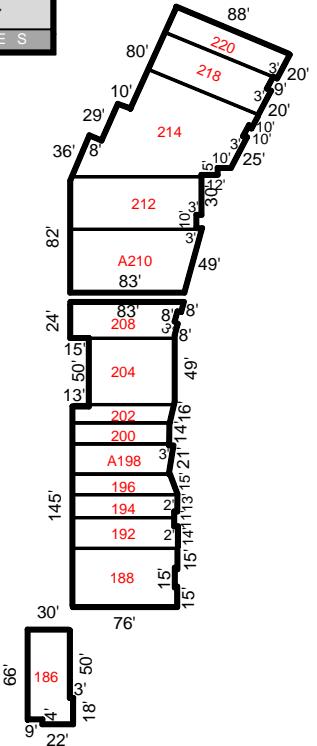

Plans produced by:
ID Plans Corp
05/10/2012
(813) 657-2545




Scale: 1in = 130ft.
0in.

© 2012





The dumpster site plan identifies the location and sizes of dumpsters, together with the name of the dumpster companies and the locations of trash cans, ash urns and grease traps.

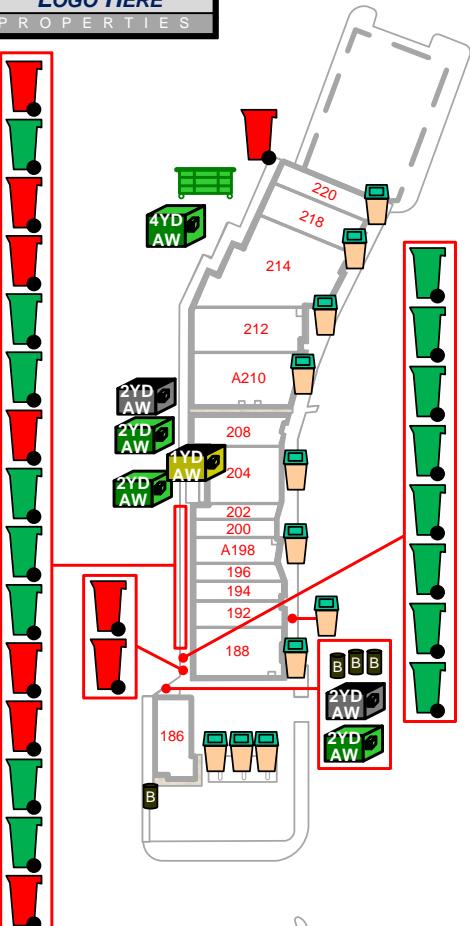

Grease Collection Company: Big Sky Enterprise (B)
Telephone Number: 800-479-7993

Waste Collection Company: Allied Waste (AW)
Telephone Number: 650-756-1130

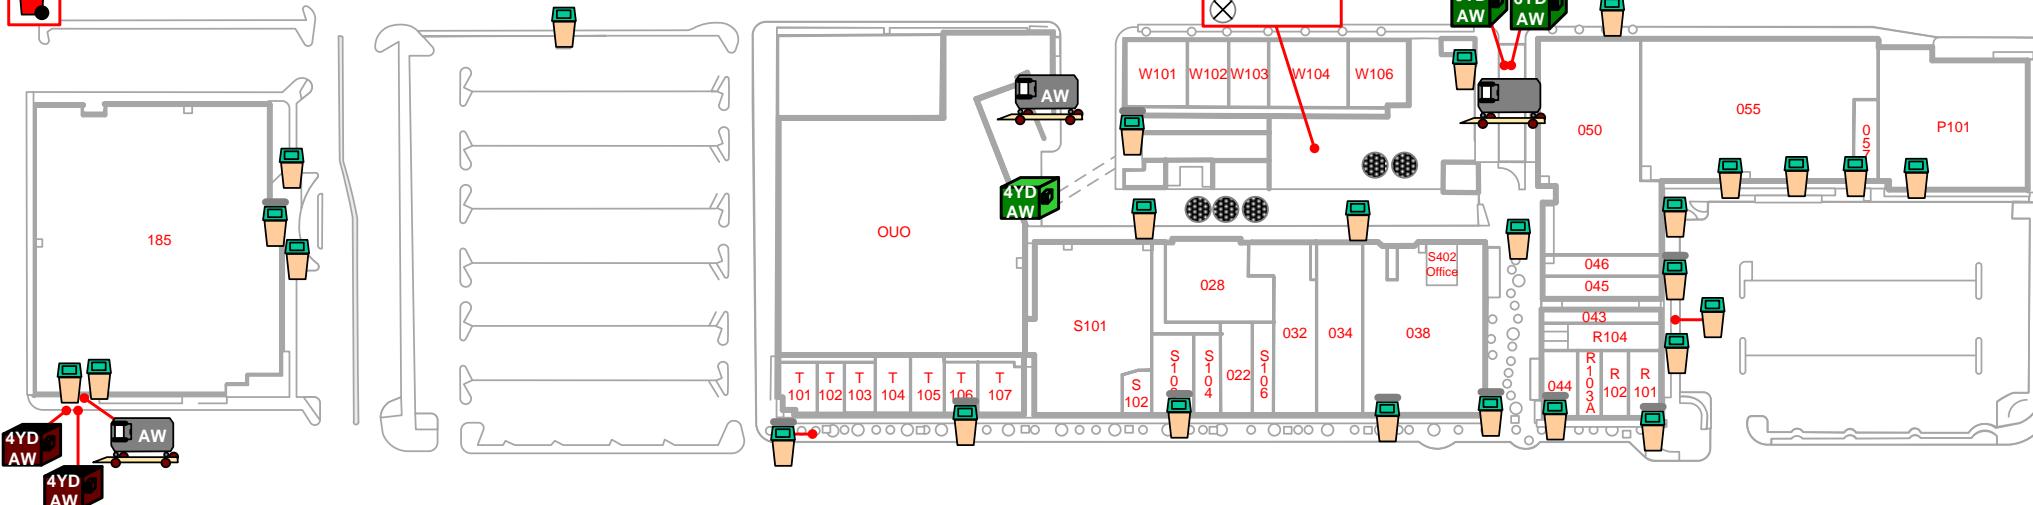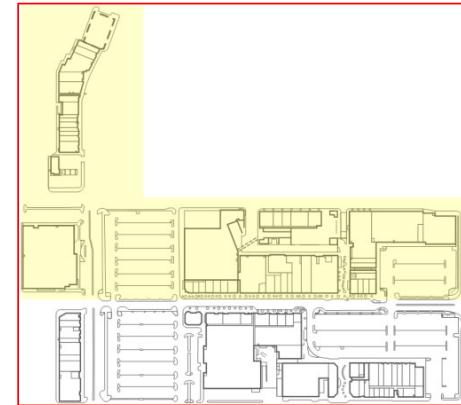


Dumpster	
Page 1 of 3	
	1YD Dumpster
	2YD Dumpster
	4YD Dumpster
	Cardboard Dumpster
	Garbage Cart
	Grease Container
	Grease Trap Sampling Point
	In-ground Grease Trap Cover
	Recycling Garbage Cart
	Rolloff Compactor
	Rolloff Dumpster
	Trash Can
	Trash Can w/Ash Tray

Plans produced by:
ID Plans Corp
05/10/2012
(813) 657-2545




© 2012

The dumpster site plan identifies the location and sizes of dumpsters, together with the name of the dumpster companies and the locations of trash cans, ash urns and grease traps.

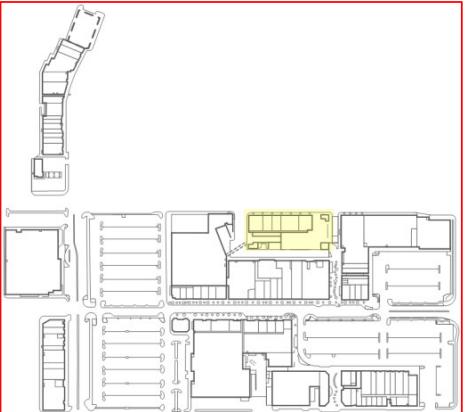


Fifth Level

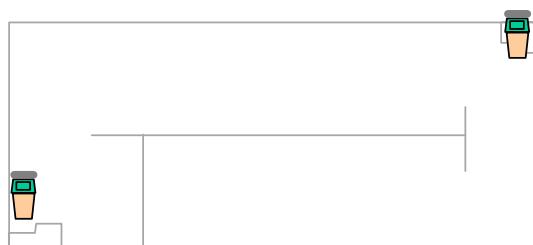


Fourth Level



Third Level

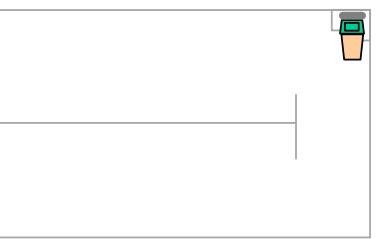

Second Level

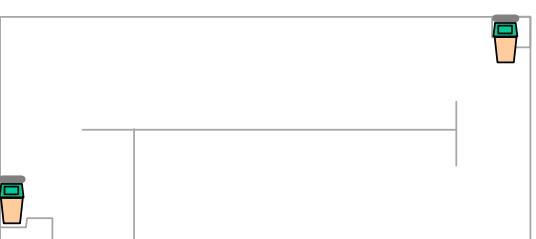

First Level

Dumpster

Page 2 of 3

 Trash Can w/Ash Tray


Plans produced by:
ID Plans Corp

05/10/2012
(813) 657-2545



© 2012





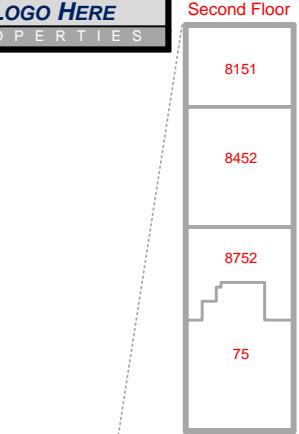


Grease Collection Company: Big Sky Enterprise (G)
Telephone Number: 800-479-7993

Waste Collection Company: Allied Waste (AW)
Telephone Number: 650-756-1130

Waste Collection Company: Superior (S)
Telephone Number: 800-773-4570

The dumpster site plan identifies the location and sizes of dumpsters, together with the name of the dumpster companies and the locations of trash cans, ash urns and grease traps.

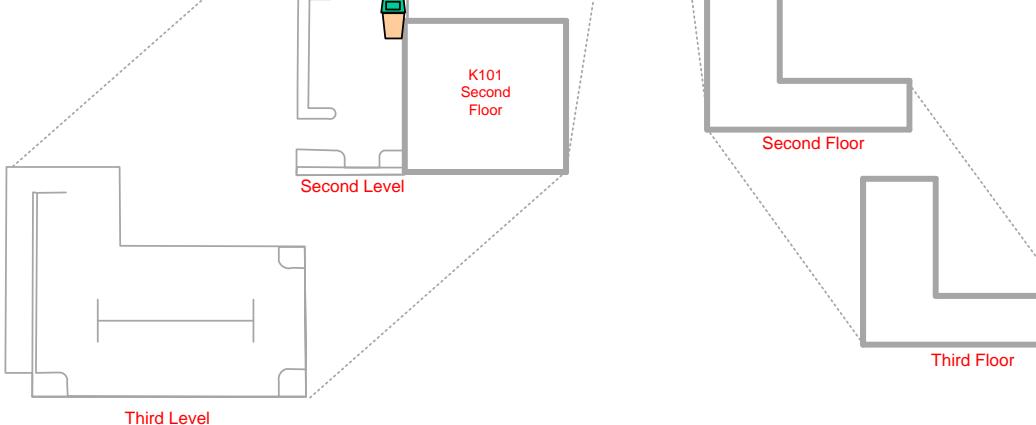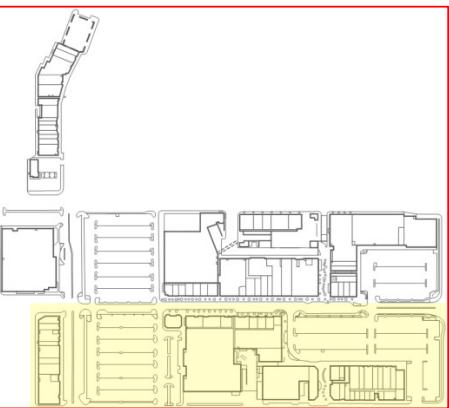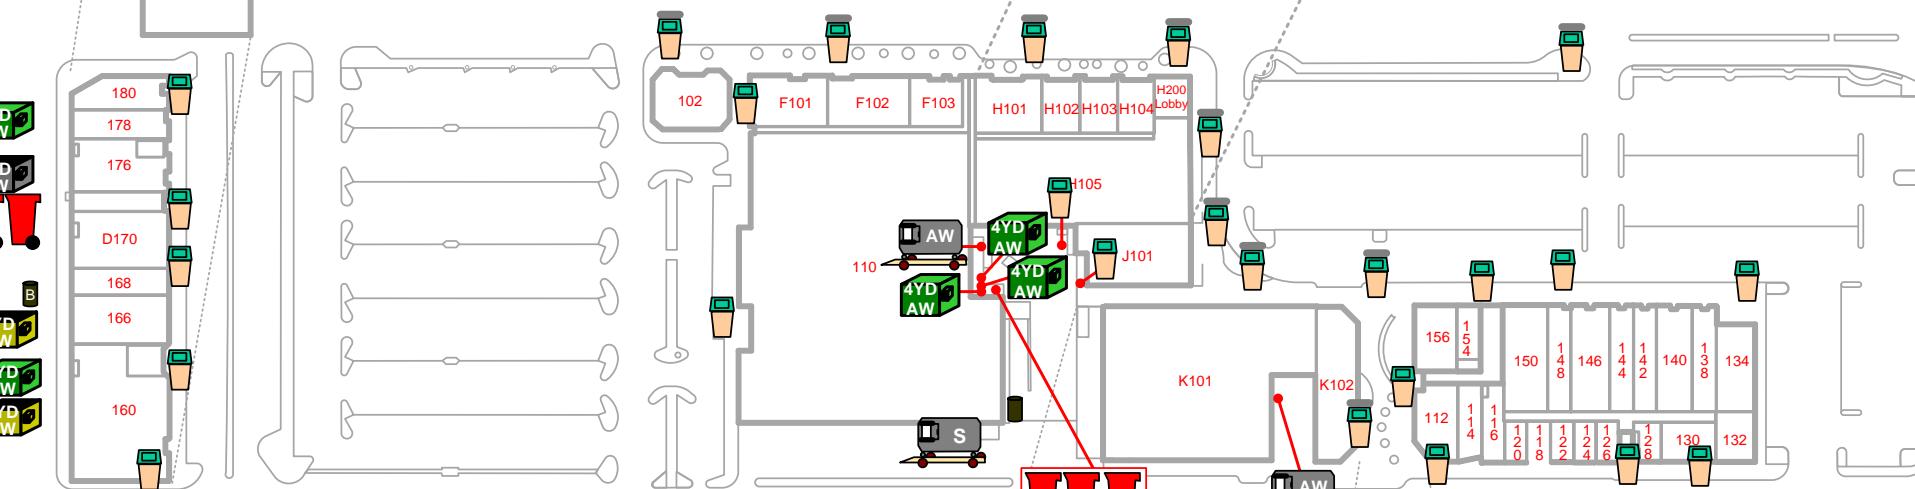

Plans produced by:
ID Plans Corp
05/10/2012
(813) 657-2545



© 2012

Dumpster	
Page 3 of 3	
	1YD Dumpster
	2YD Dumpster
	Cardboard Dumpster
	Garbage Cart
	Grease Container
	Rolloff Compactor
	Trash Can
	Trash Can w/Ash Tray



The electrical site plan details all electric meters matched with the spaces they operate and the corresponding tenant name and the meter number. It also locates outside receptacles, phone booths and telephone numbers.


Electric Meter Information							
Reference #	Space #	Tenant Name	Meter #	Reference #	Space #	Tenant Name	Meter #
1	214	KING WAH RESTAURANT	1006530183	37	S102	CLAIRES	490R98
2	218	AVAILABLE	6T5948	38	S101	FURNITURE GALLERY	1004464961
3	HOUSE	LIGHTING	1006530181	39	028	BANANA ISLAND	51246T
4	220	MARTIAL ARTS	1006498116	40	S103	AVAILABLE	5939T6
5	214	KING WAH RESTAURANT	1003708755	41	HOUSE	LIGHTING	36058T
6	212	KUMON LEARNING CENTER	83R051	42	S104	AVON	4T8179
7	A210	AVAILABLE	882R55	43	022	DALY CITY OPTOMETRY	6T4527
8	208	BANGKOK GARDEN	T27767	44	HOUSE	311 LAKE MERCED BLVD.	668R67
9	204	UNITED STATES POSTAL OFFICE	65T782	45	028	BANANA ISLAND	1607R7
10	196	TIMES SALON	329317	46	034	PARTY WAREHOUSE	1004464763
11	A198	H&R BLOCK	758T72	47	032	HOLLYWOOD VIDEO	359T60
12	202	MANNY'S HAIRCUT	356253	48	S106	GAMESTOP	T05007
13	200	GENESIS DENTAL	355946	49	038	BEVERLY'S	10R085
14			291176*	50		ADDRESS 283	1004460803
15	188	WESTLAKE COIN LAUNDRY	355953	51		ADDRESS 284	758T76
16	194	SUBWAY	W01323	52		INACTIVE	759T36
17	192	QUICKLY	45060T	53	S402	LE HO & COMPANY	639T29
18	188	WESTLAKE COIN LAUNDRY	926N90	54	050	DSW SHOES	1003019972
19			NO METER	55	R101	STARBUCKS	1003020052
20	186	ARCO	5P4900	56	R103A	JAMBA JUICE	31P731
21	185	BURLINGTON COAT FACTORY	1004464204	57	044	DAPNE'S GREEK CAFÉ	1004460793
22	OVO	HOME DEPOT	1004391145	58	043	GEOGETTE'S OF WESTLAKE	P21518
23	HOUSE	LIGHTING/ELEVATORS	1004464762	59	R104	WESTLAKE VISION CENTER	X18124
24			NO METER	60	046	BASKIN ROBBINS	1003709126
25	W106	LITTLE FIRE POT/DIM SUM BAKERY	1003653559	61	R102	AT&T	63P805
26			NO METER	62		ADDRESS 318 SUITE 270	1003744457
27			NO METER	63			NO METER
28	W106	LITTLE FIRE POT/DIM SUM BAKERY	10003693016	64	045	SLIDERS DINER	5P6634
29			NO METER	65	045	SLIDERS DINER	21P732
30			NO METER	66			NO METER
31	W101	MASSAGE ENVY SALON	22P028	67	HOUSE	SECOND LEVEL	1004464759
32	W102	WESTLAKE NAIL SALON	1003745032	68	055	WALGREENS	C09058
33			NO METER	69	HOUSE	LIGHTING	82R237
34	W106	LITTLE FIRE POT/DIM SUM BAKERY	1003653412	70	057	GNC	1003648255
35		ADDRESS 478	1003143782	71	P101	T.J. MAXX	1004450810
36	W104	AVAILABLE	86P119				

Plans produced by:
ID Plans Corp
05/10/2012
(813) 657-2545





© 2012



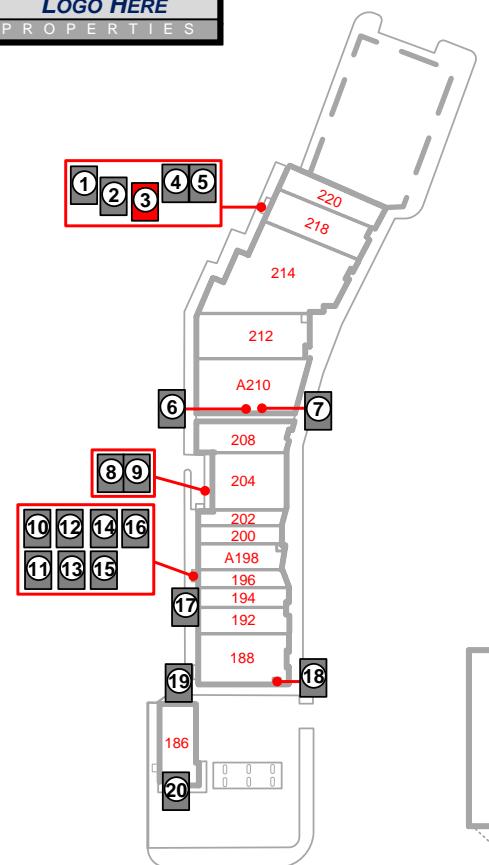

The electrical site plan details all electric meters matched with the spaces they operate and the corresponding tenant name and the meter number. It also locates outside receptacles, phone booths and telephone numbers.

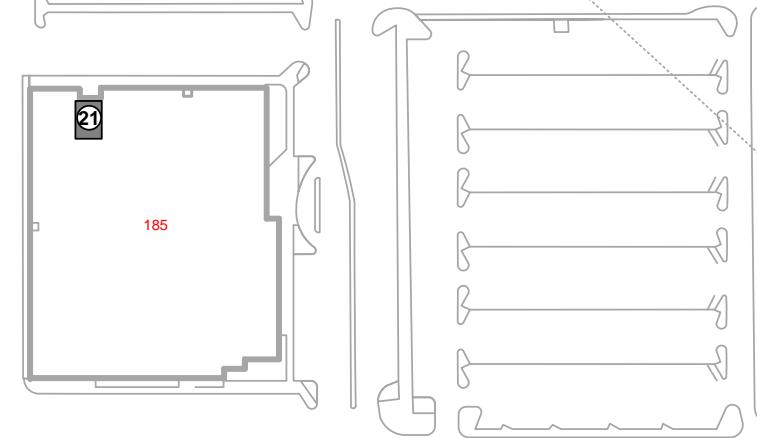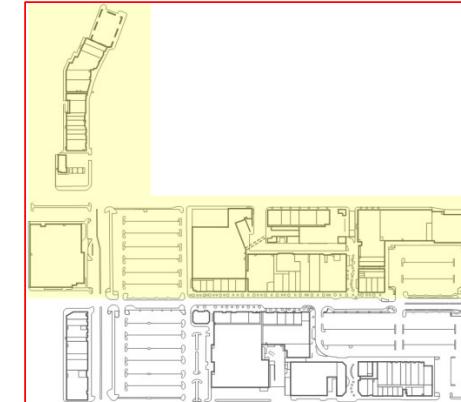

Power Company: Gas & Electric Company
Telephone Number: 800-555-1000

The electrical site plan details all electric meters matched with the spaces they operate and the corresponding tenant name and the meter number. It also locates outside receptacles, phone booths and telephone numbers.


Electric Meter Information							
Reference #	Space #	Tenant Name	Meter #	Reference #	Space #	Tenant Name	Meter #
72	75	2ND FLOOR	1003867954	111	H102	GOOD FEET	34508R
73	180	US BANK	0M6350	112	H103	COLOR ME MINE	M15659
74	178	PHO HUY NH HIEP 3	44657T	113			NO METER
75	166	HSBC	1003739780	114	K102	SLEEP TRAIN	1P9351
76	8452	SETON MEDICAL CENTER	1004460813	115	J101	SAN MATEO CREDIT UNION	62P776
77	176	PATELCO CREDIT UNION	416499	116	HOUSE	LIGHTING	1004464915
78	D170	BANK OF AMERICA	1003152199	117			NO METER
79	D170	BANK OF AMERICA	9N1450	118	K101	ROSS DRESS FOR LESS	1003743619
80	D170	BANK OF AMERICA	P67590	119	134	CHIPOTLE MEXICAN GRILL	5P8588
81			NO METER	120	120	WESTLAKE SHOE REPAIR	21R032
82	168	TOKYO TERIY KIJA PANES CUISINE	1006527125	121		ADDRESS 48	4301R4
83	160	CHASE	1004454649	122	116	STRUCTURE HAIR	6T5810
84	160	CHASE	1004459842	123	154	WESTLAKE HEARING AID CENTER	5T6040
85	HOUSE	LIGHTING	1003203536	124	114	CIGARETTES R CHEAPER	6T5820
86			NO METER	125	118	WESTLAKE ART GALLERY	5T7543
87	110	SAFEWAY	E000401	126	112	WESTLAKE LIQUORS	33M239
88	110	SAFEWAY	1004464963	127	126	TANIS KITCHEN	5T7540
89			NO METER	128	124	MAGIC TOUCH BEAUTY SALON	6T4976
90	102	88 RICE BOWL	62P773	129		INACTIVE	6T5027
91	T101	SHENG KEE BAKERY	1003138304	130	129	WESTLAKE COFFEE SHOP	7T5881
92	T103	AVAILABLE	1003020651	131		MEDICAL BUILDING	10R084
93	T102	AVAILABLE	1003020652	132	HOUSE	LIGHTING	1003020803
94	T106	DAI ICHI	1003020796	133			NO METER
95	T105	LOBELLA	1003020645	134	142	RED WING SHOES	8T3837
96	T104	KICK CITY	1004020655	135	144	UPS STORE	8T3667
97	HOUSE	LIGHTING	02R639	136	146	BANK OF THE WEST	64T936
98	T107	YOGURT CITY	1003020800	137	148	BROASTER CHICKEN	1006478228
99	F102	GERRY'S GRILL	34506R	138	140	RADIO SHACK	5T7541
100			NO METER	139	138	SUPER CUTS	725T73
101	F103	BURGERMEISTERS HAMBURGERS	76M291	140	132	NATIONS GIANT HAMBURGERS	X05030
102	F101	KANA JANPANESE CUISINE	21P953	141	122	PULIDO'S TAILOR	2T9636
103			NO METER	142			NO METER
104	H105	TRADER JOE'S	1P8758	143	128	ELITE HAIR SALON	8T3838
105			NO METER	144	128	ELITE HAIR SALON	4T7495
106	H200	COST PLUS WORLD MARKET	1004577672	145	150	T-MOBILE	1003708747
107	H101	VERIZON WIRELESS	47634R	146	130	DANCO REALTY	8T3864
108			NO METER	147	HOUSE	PYLON SIGN	1003662367
109	H104	MIKI	M13670	148		SPRINT	1004389287
110	HOUSE	LIGHTING	M15445				

Plans produced by:
ID Plans Corp
05/10/2012
(813) 657-2545



© 2012




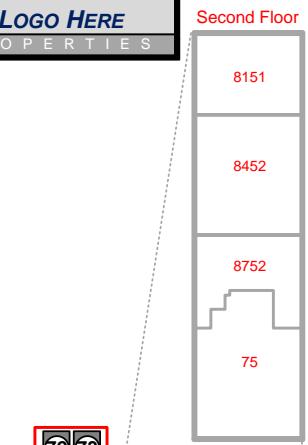

The electrical site plan details all electric meters matched with the spaces they operate and the corresponding tenant name and the meter number. It also locates outside receptacles, phone booths and telephone numbers.

Electrical
Page 4 of 7


	Electrical Outlet
	House Electric Meter with Number

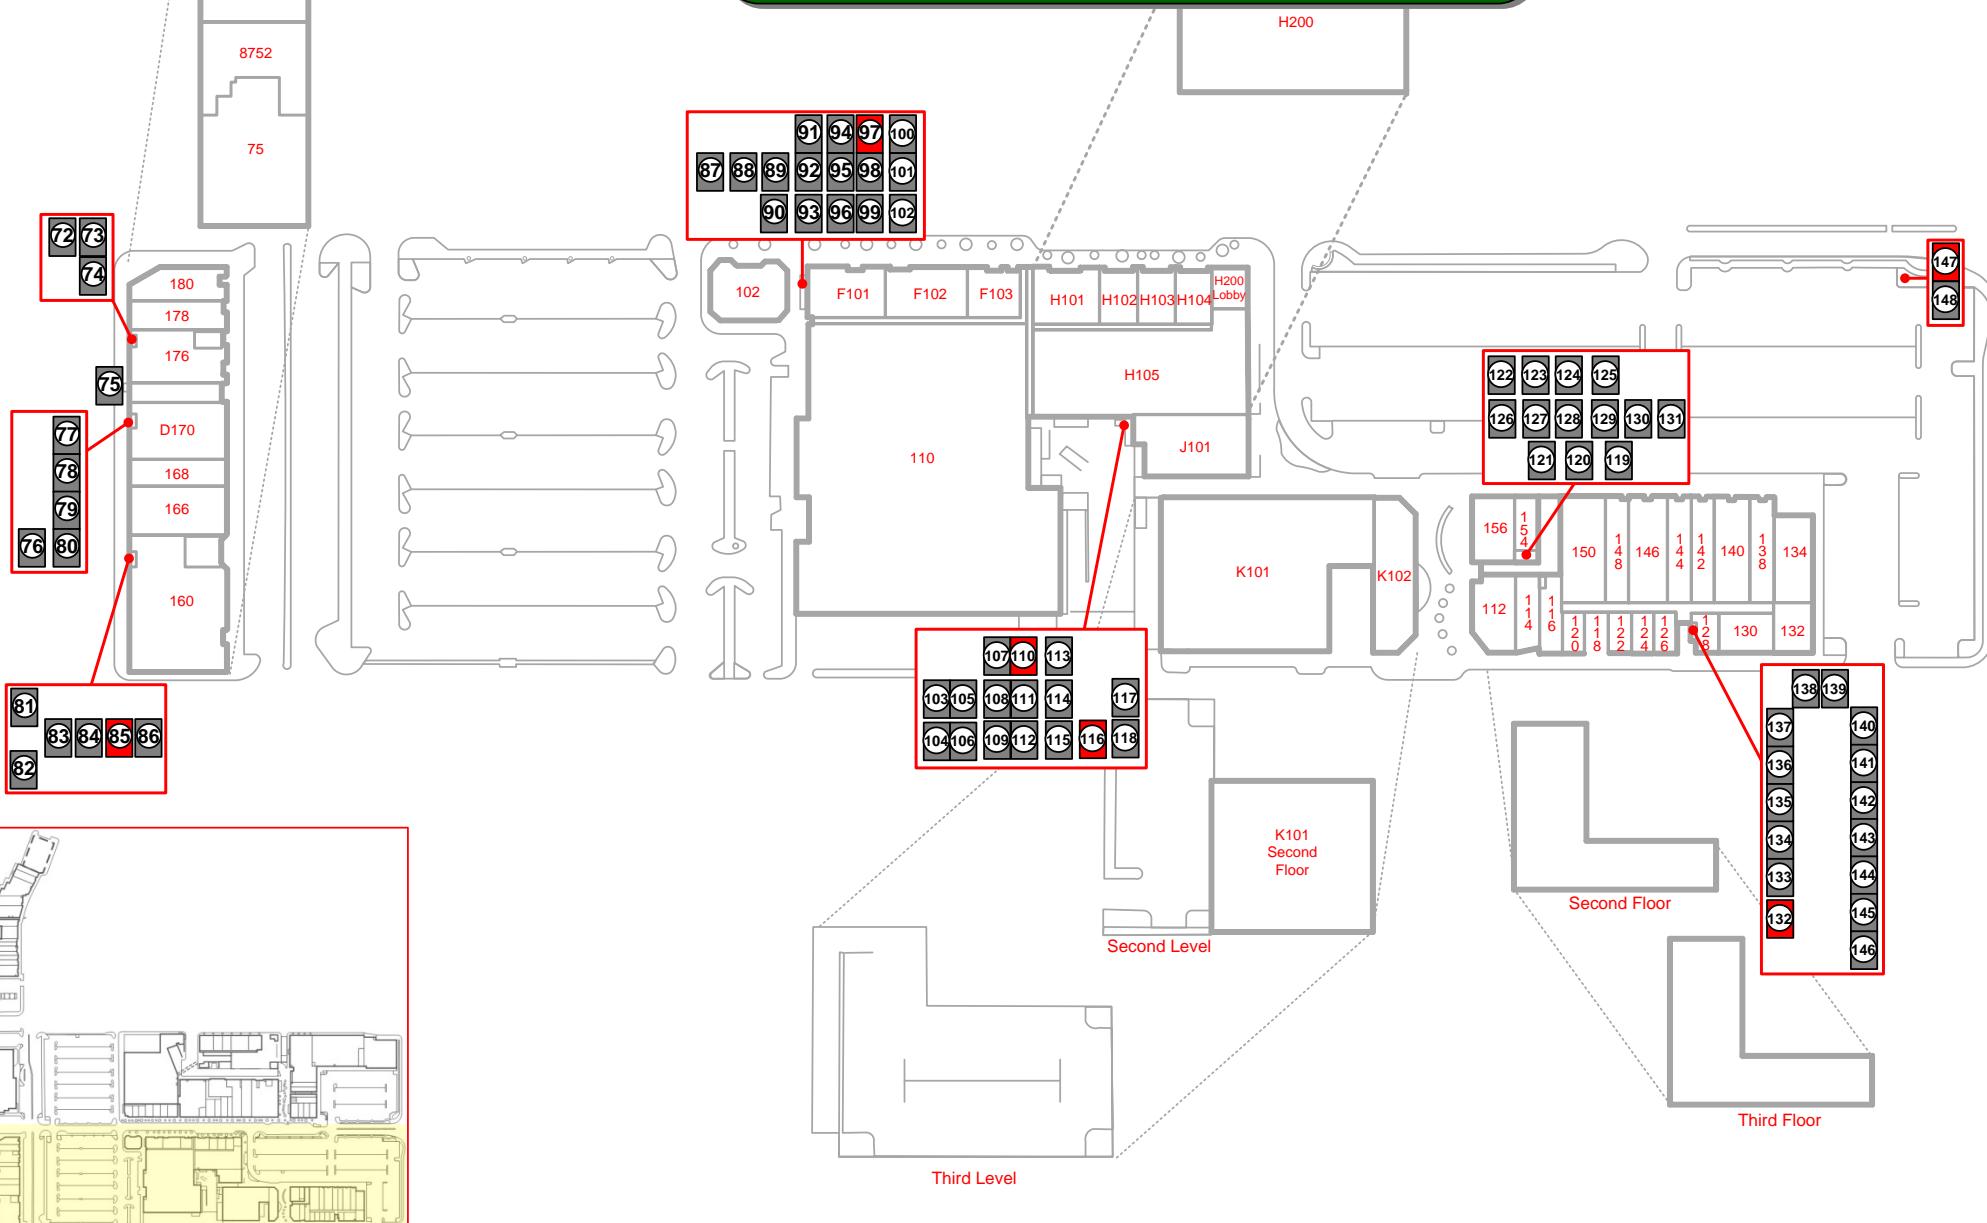


Plans produced by:
ID Plans Corp
05/10/2012
(813) 657-2545



© 2012

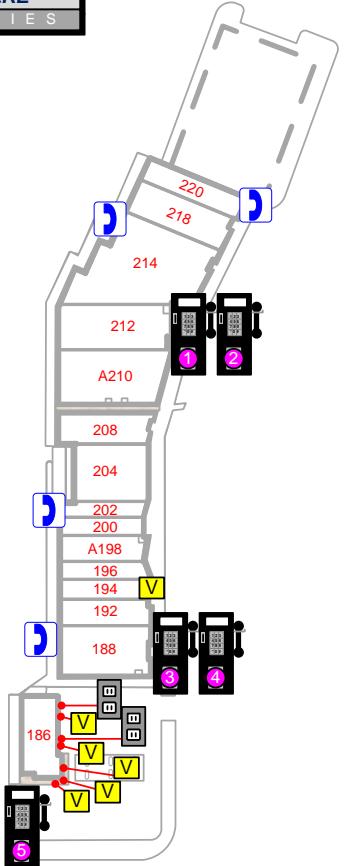

The electrical site plan details all electric meters matched with the spaces they operate and the corresponding tenant name and the meter number. It also locates outside receptacles, phone booths and telephone numbers.

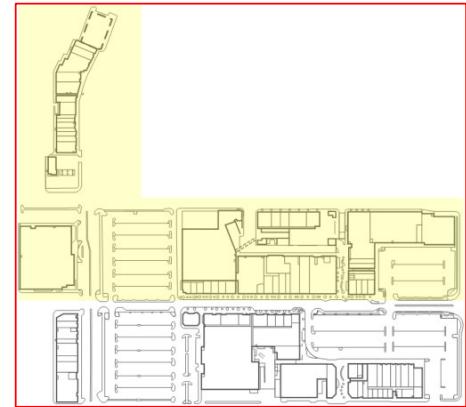

Electrical
Page 5 of 7

	Electric Manhole Cover
	Electrical Outlet
	Electrical Outlet on Light Pole
	Generator
	Pay Telephone
	Telephone Junction Box
	Transformer
	Video Camera

Pay Telephone Number Service Provider


1	650-991-8839	Pay Phones, 800-500-0000
2	650-991-7283	Pay Phones, 800-500-0000
3	650-758-6537	Pay Phones, 800-500-0000
4	No Information	Pay Phones, 800-500-0000
5	650-756-4767	Pay Phones, 800-500-0000
6	650-994-9955	Pay Phones, 800-500-0000
7	650-994-9957	Pay Phones, 800-500-0000






Plans produced by:
ID Plans Corp
05/10/2012
(813) 657-2545




© 2012

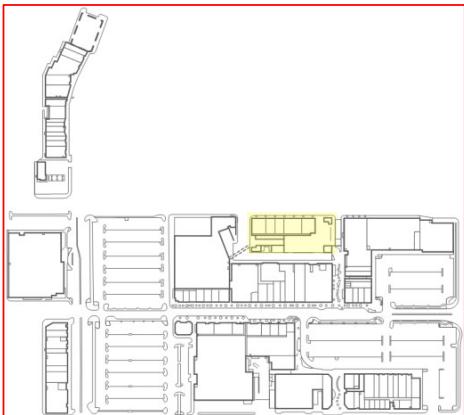


The electrical site plan details all electric meters matched with the spaces they operate and the corresponding tenant name and the meter number. It also locates outside receptacles, phone booths and telephone numbers.

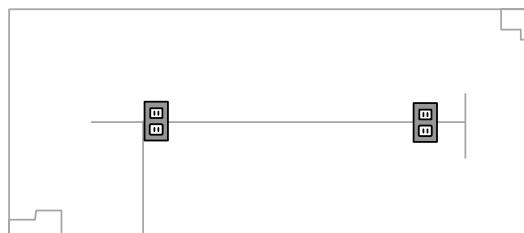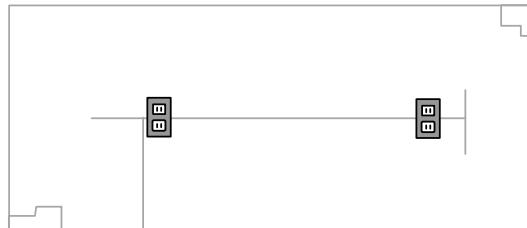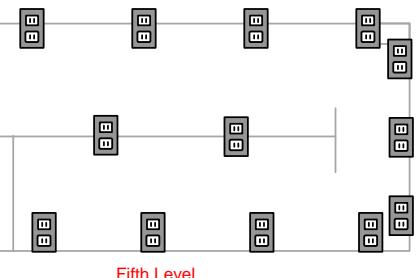

Third Level

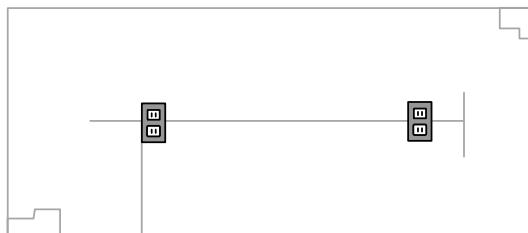

Second Level

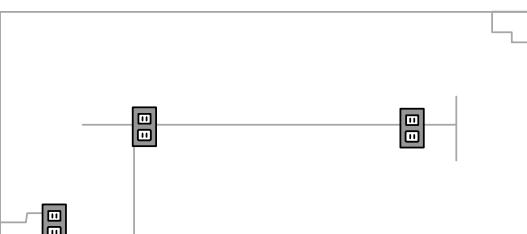


First Level


Electrical Outlet

Plans produced by:
ID Plans Corp
05/10/2012
(813) 657-2545



© 2012

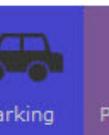

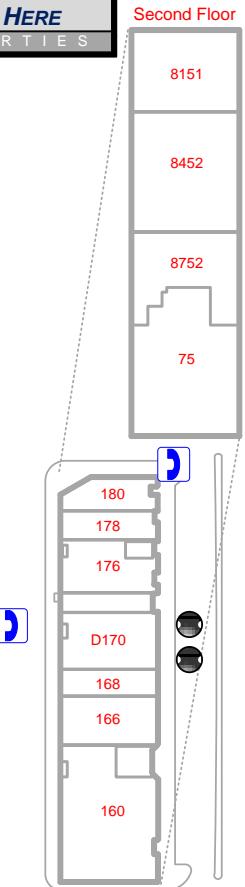




The electrical site plan details all electric meters matched with the spaces they operate and the corresponding tenant name and the meter number. It also locates outside receptacles, phone booths and telephone numbers.

Pay Telephone Number Service Provider

8 650-991-9836 Pay Phones, 800-500-000
9 650-991-9834 Pay Phones, 800-500-000

Electrical
Page 7 of 7

	Electric Manhole Cover
	Electrical Outlet
	Electrical Outlet on Light Pole
	Pay Telephone
	Telephone Junction Box
	Transformer
	Video Camera

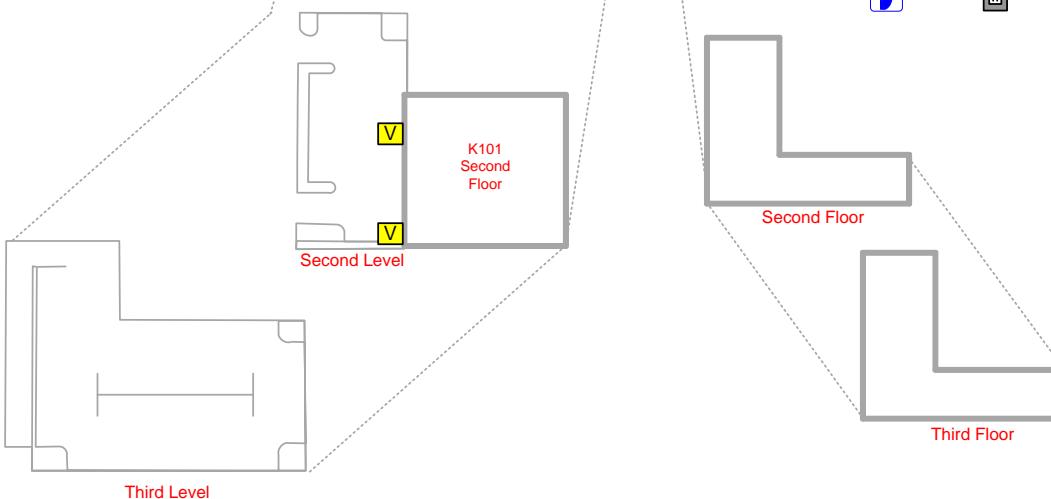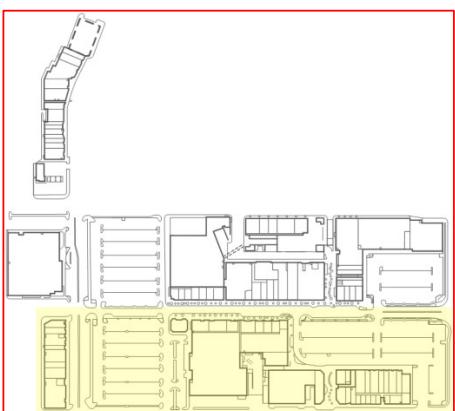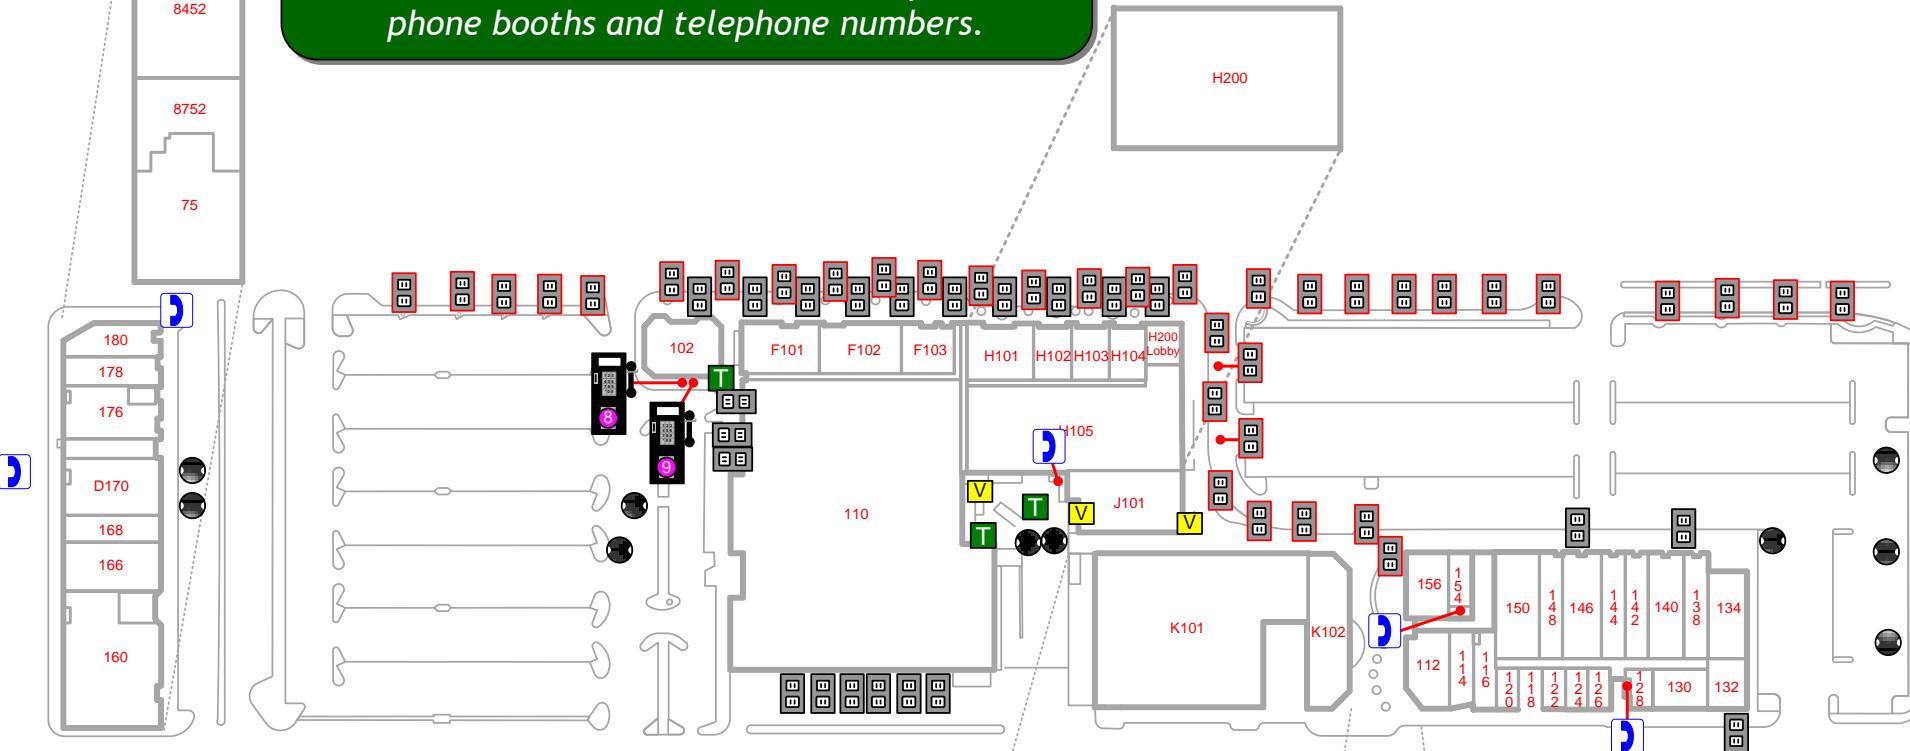

Plans produced by:
ID Plans Corp
05/10/2012
(813) 657-2545



© 2012

The emergency response site plan is a compilation of the electrical, fire and water site plans, for quick, easy-access in case of any emergency situation.



EMERGENCY CONTACTS		
Architects	Universal Design	800-555-1234
Building inspector	US Inspectors	800-555-5678
Electric Generators	Alpine Electric	800-555-4321
Fire		911
First Responder		911
General Contractors	Sunshine Contracting	888-555-9876
General site cleanup	John's Maintenance	888-555-9999
Police		911
Roofers	Reliable Roofing	888-555-4433
Security	ABC Alarm	888-555-1212
Structural Engineers	Design Source	888-555-3443
Utilities		
Electric	Gas & Electric Company	800-555-1000
Gas	Gas & Electric Company	800-555-1000
Water	City Dept. of Public Works	888-225-5300

Plans produced by:
ID Plans Corp
05/10/2012
(813) 657-2545



© 2012

The emergency response site plan is a compilation of the electrical, fire and water site plans, for quick, easy-access in case of any emergency situation.

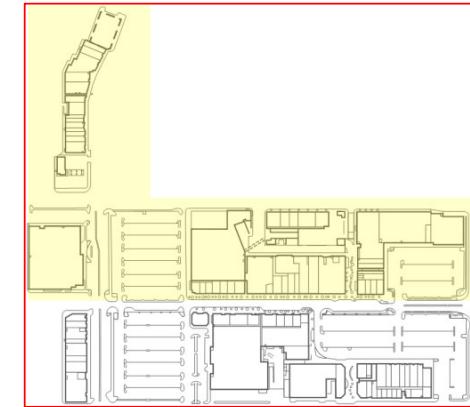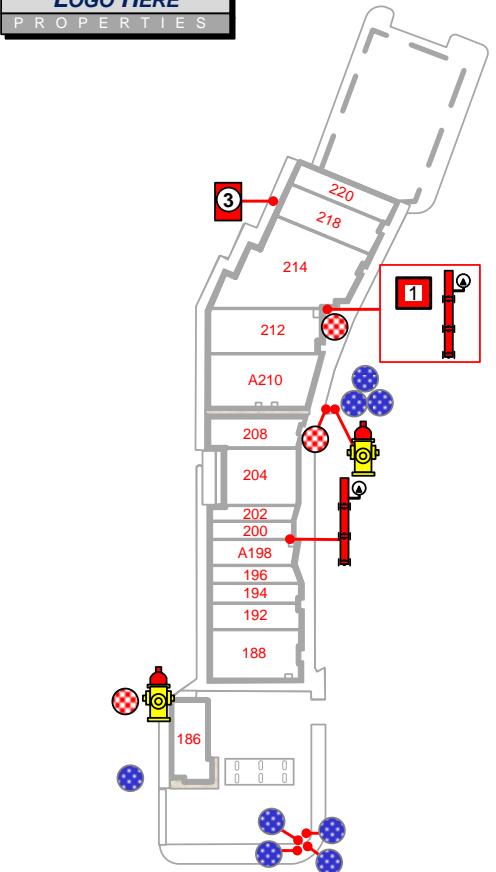


ID Plans Mall

Emergency Response

Page 2 of 3

Electric Meter Information				
Reference #	Plot #	Tenant Name	Meter #	
3	HOUSE	LIGHTING	1006530181	
23	HOUSE	LIGHTING/ELEVATORS	1004464762	
41	HOUSE	LIGHTING	36058T	
44	HOUSE	LIGHTING	668R67	
67	HOUSE	LIGHTING	1004464759	
69	HOUSE	LIGHTING	82R237	

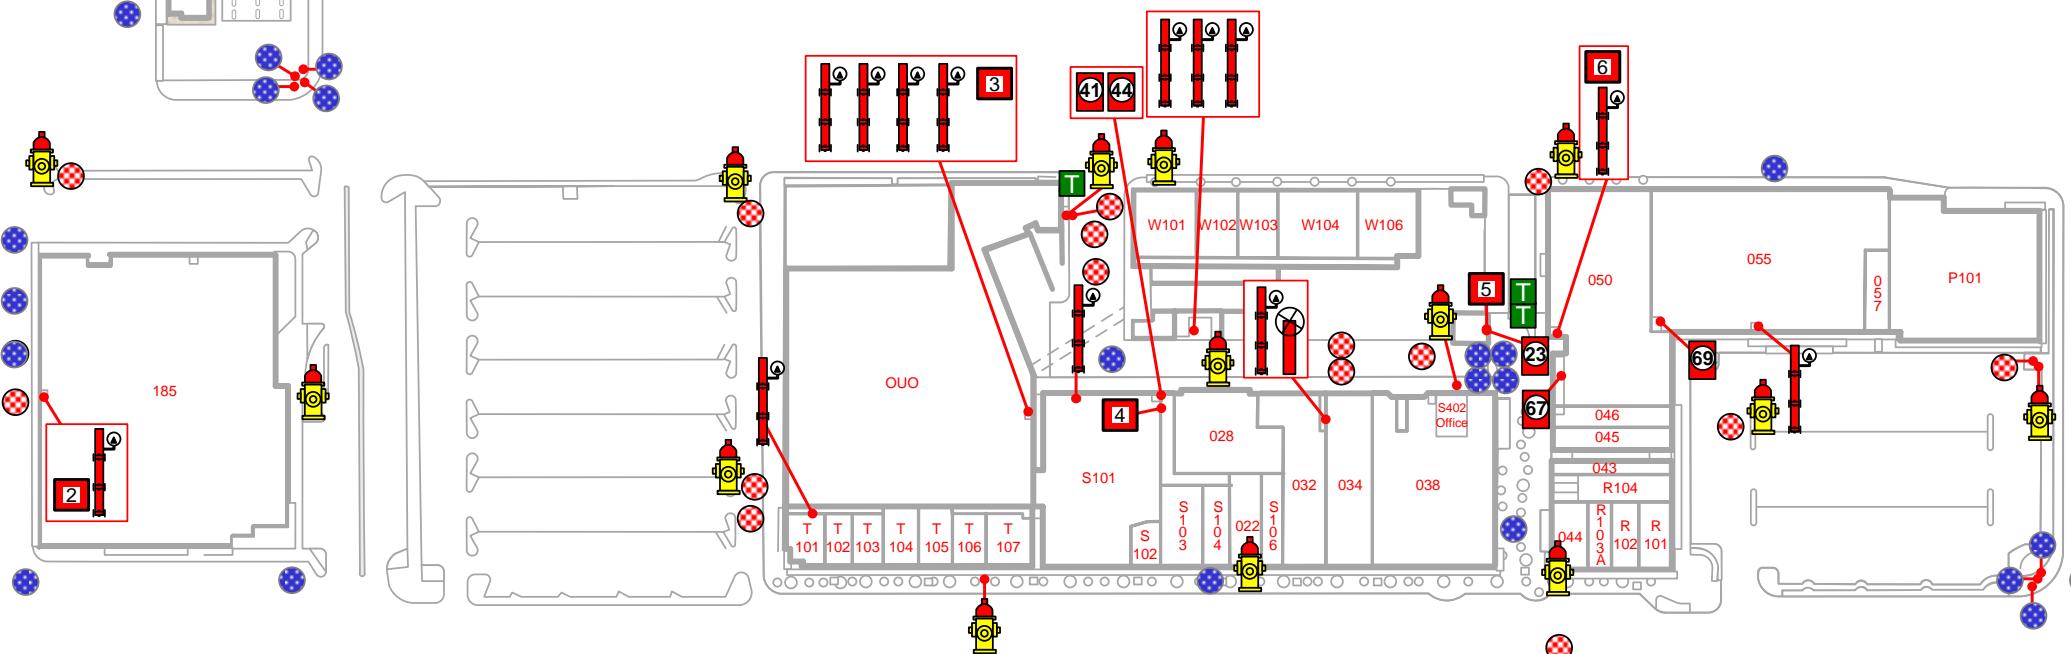


Plans produced by:
ID Plans Corp
05/10/2012
(813) 657-2545



© 2012

The fire site plan identifies the locations of all fire hydrants, risers, valves and fire riser rooms, if present.

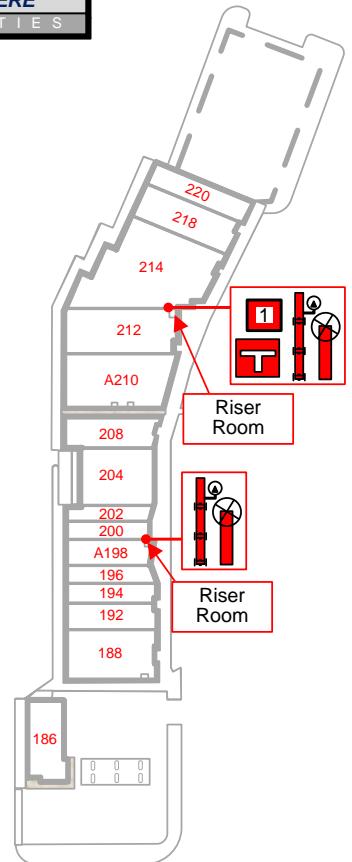

Fire Alarm Control Panel Information



1

Ademco
Vista32FB

Monitoring Company: [Stanley Security](#)
Telephone Number: [877-555-4968](#)
Service Company: [Aquamatic Fire Protection](#)
Telephone Number: [800-555-FIRE](#)

Fire Alarm Control Panel Information




2

ADT
Focus

Monitoring Company: [ADT](#)
Telephone Number: [800-555-2727](#)
Service Company: [Aquamatic Fire Protection](#)
Telephone Number: [800-555-FIRE](#)

Fire Alarm Control Panel Information

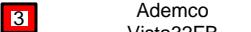


3

Ademco
Vista32FB

Monitoring Company: [ADT](#)
Telephone Number: [800-555-2727](#)
Service Company: [Cosco Fire Protection](#)
Telephone Number: [800-555-7984](#)

Fire Alarm Control Panel Information

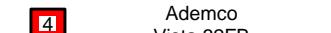

4

Ademco
Vista 32FB

Monitoring Company: [Stanley Security](#)
Telephone Number: [877-555-4968](#)
Service Company: [Aquamatic Fire Protection](#)
Telephone Number: [800-555-FIRE](#)

Fire Alarm Control Panel Information



5

GE
EST Quickstart

Monitoring Company: [Stanley Secuity](#)
Telephone Number: [877-555-4968](#)
Service Company: [Aquamatic Fire Protection](#)
Telephone Number: [800-555-FIRE](#)




Fire Alarm Control Panel Information



6

GE
EST Quickstart

Monitoring Company: [Stanley Secuity](#)
Telephone Number: [877-555-4968](#)
Service Company: [Aquamatic Fire Protection](#)
Telephone Number: [800-555-FIRE](#)

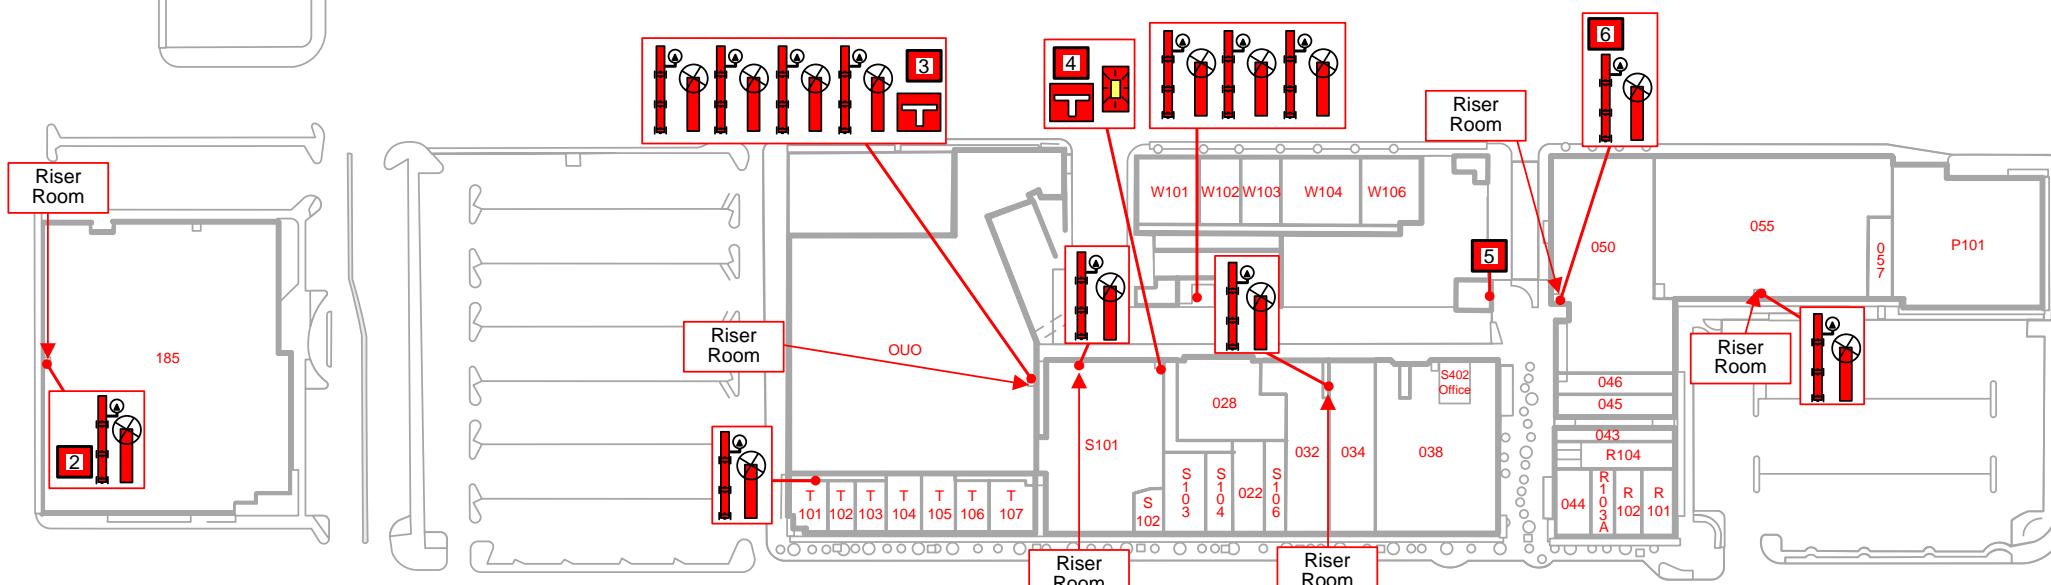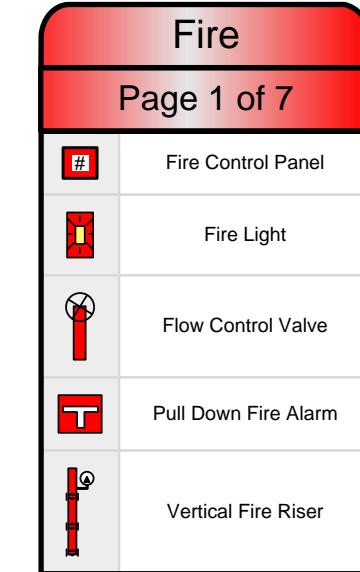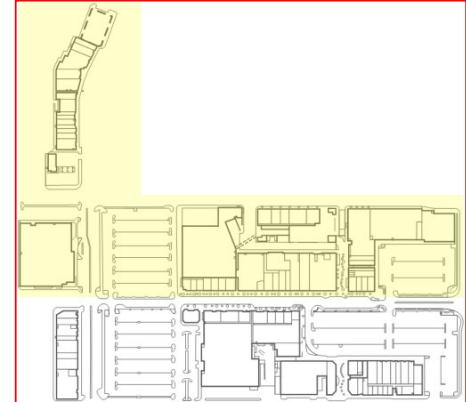


Plans produced by:
ID Plans Corp
05/10/2012
(813) 657-2545




© 2012

The fire site plan identifies the locations of all fire hydrants, risers, valves and fire riser rooms, if present.

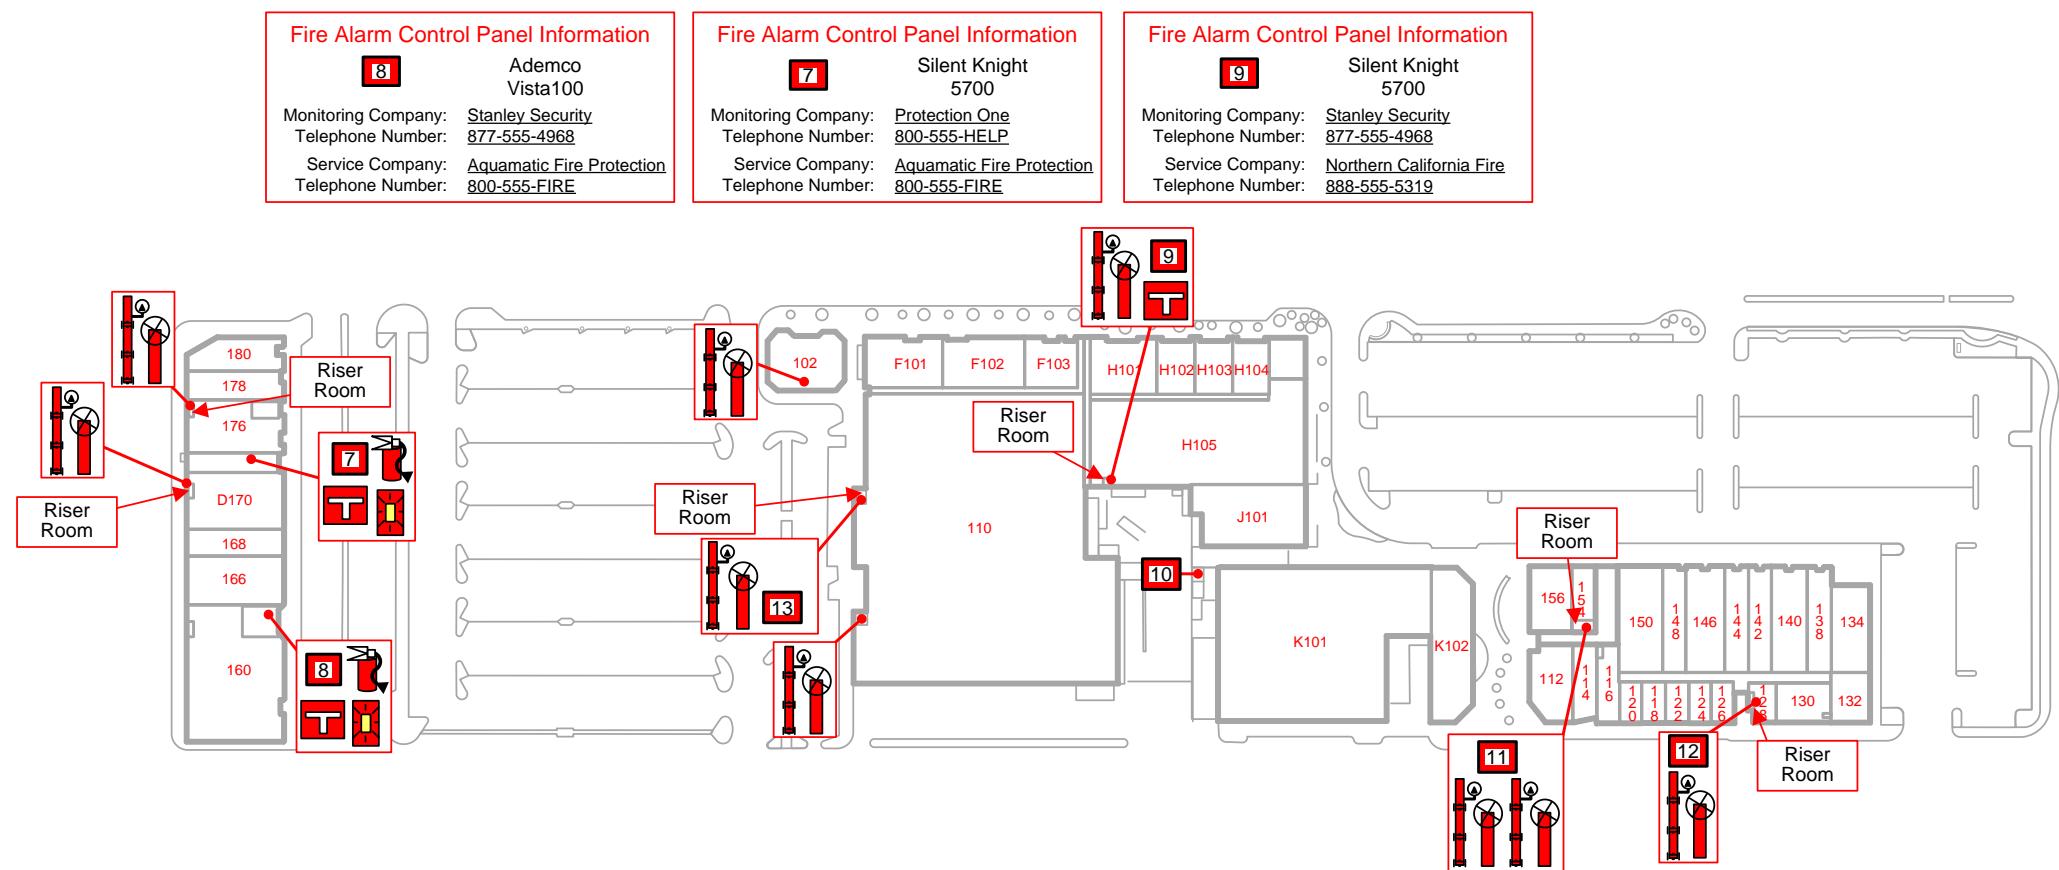

Fire	
Page 2 of 7	
#	Fire Control Panel
	Fire Extinguisher
	Fire Light
	Flow Control Valve
	Pull Down Fire Alarm
	Vertical Fire Riser

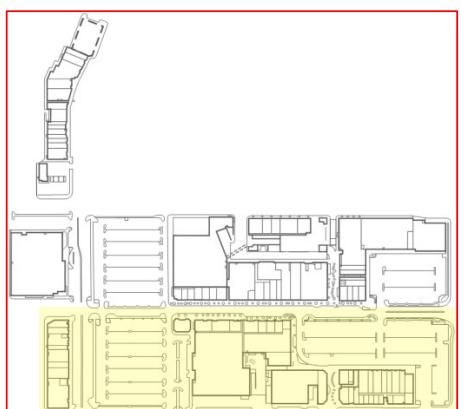


Fire Alarm Control Panel Information	Fire Alarm Control Panel Information
Riser 10: Silent Knight 5808. Monitoring Company: Stanley Security, Telephone Number: 877-555-4968. Service Company: Aquamatic Fire Protection, Telephone Number: 800-555-FIRE.	Riser 12: Ademco 32FB. Monitoring Company: Stanley Security, Telephone Number: 877-555-4968. Service Company: Aquamatic Fire Protection, Telephone Number: 800-497-FIRE.
Riser 11: Ademco Vista100. Monitoring Company: Stanley Security, Telephone Number: 877-555-4968. Service Company: Aquamatic Fire Protection, Telephone Number: 800-555-FIRE.	Riser 13: Silent Knight 5104. Monitoring Company: Fire Plus, Telephone Number: 800-555-1091. Service Company: Aquamatic Fire Protection, Telephone Number: 800-555-FIRE.

Plans produced by:
ID Plans Corp
05/10/2012
(813) 657-2545




© 2012

The fire site plan identifies the locations of all fire hydrants, risers, valves and fire riser rooms, if present.



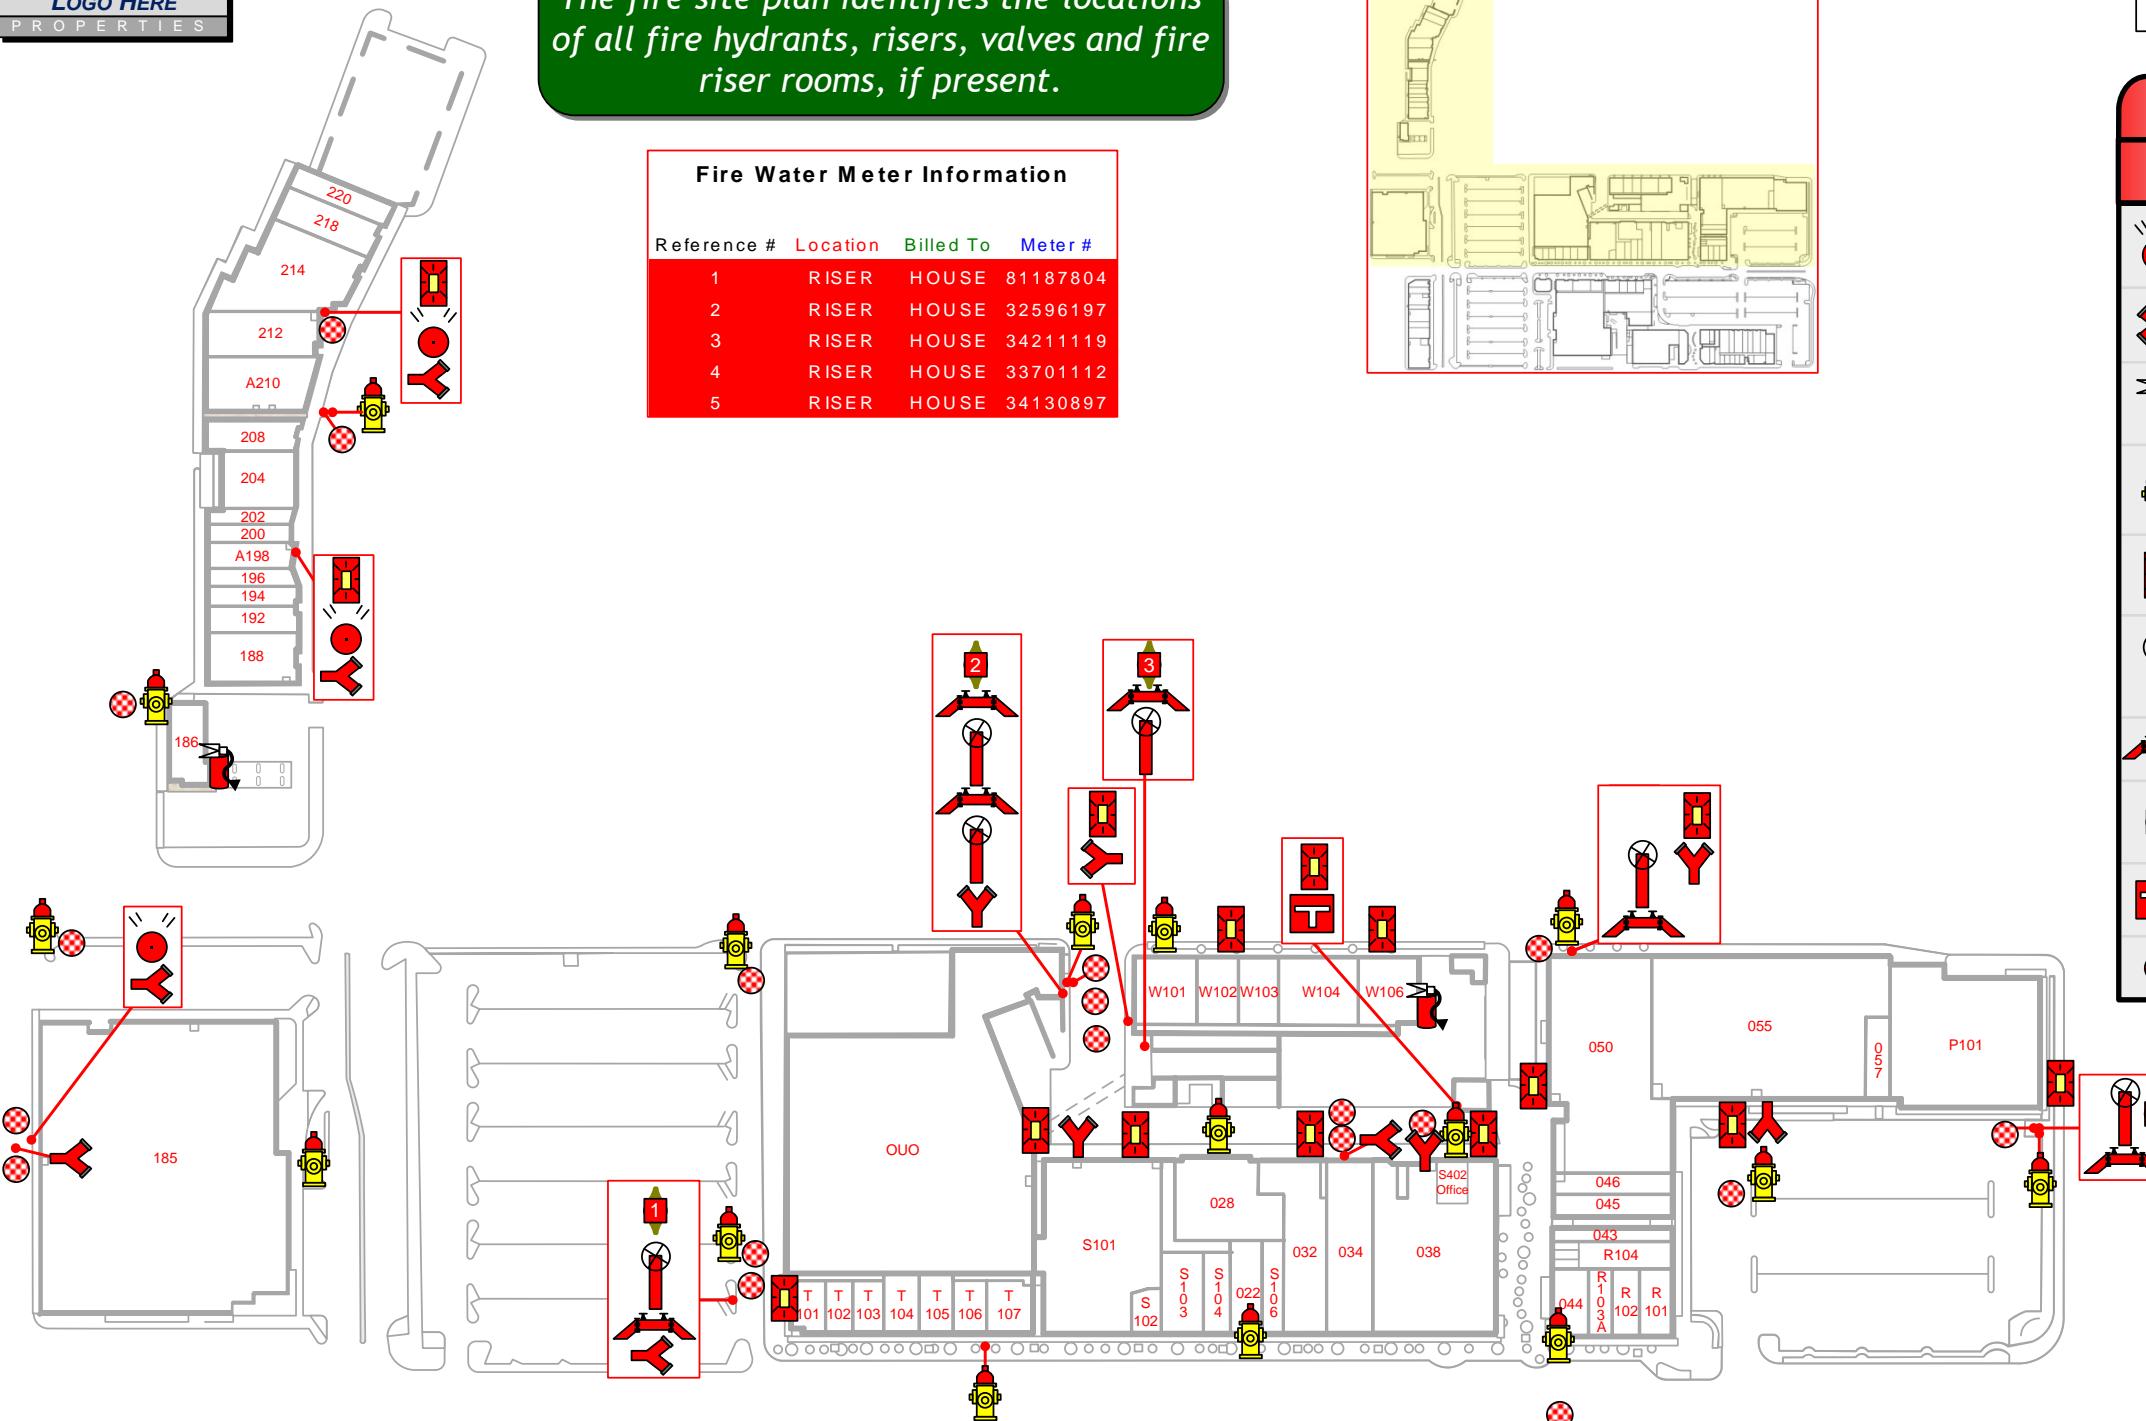


Plans produced by:
ID Plans Corp
05/10/2012
(813) 657-2545

ID Plans Corp. © 2012

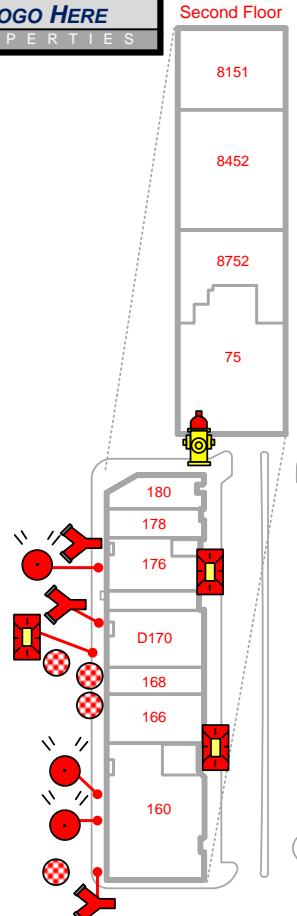

The fire site plan identifies the locations of all fire hydrants, risers, valves and fire riser rooms, if present.

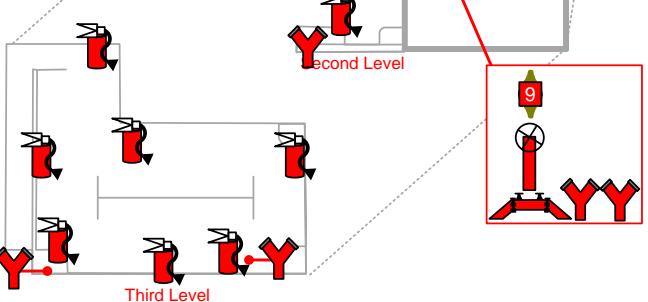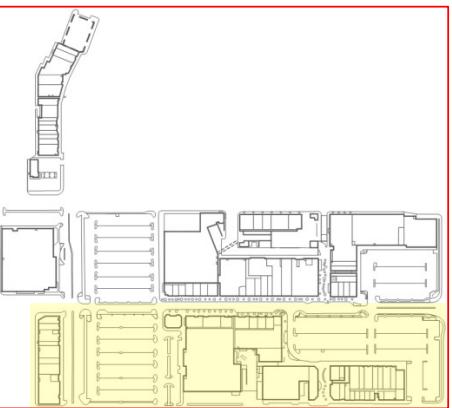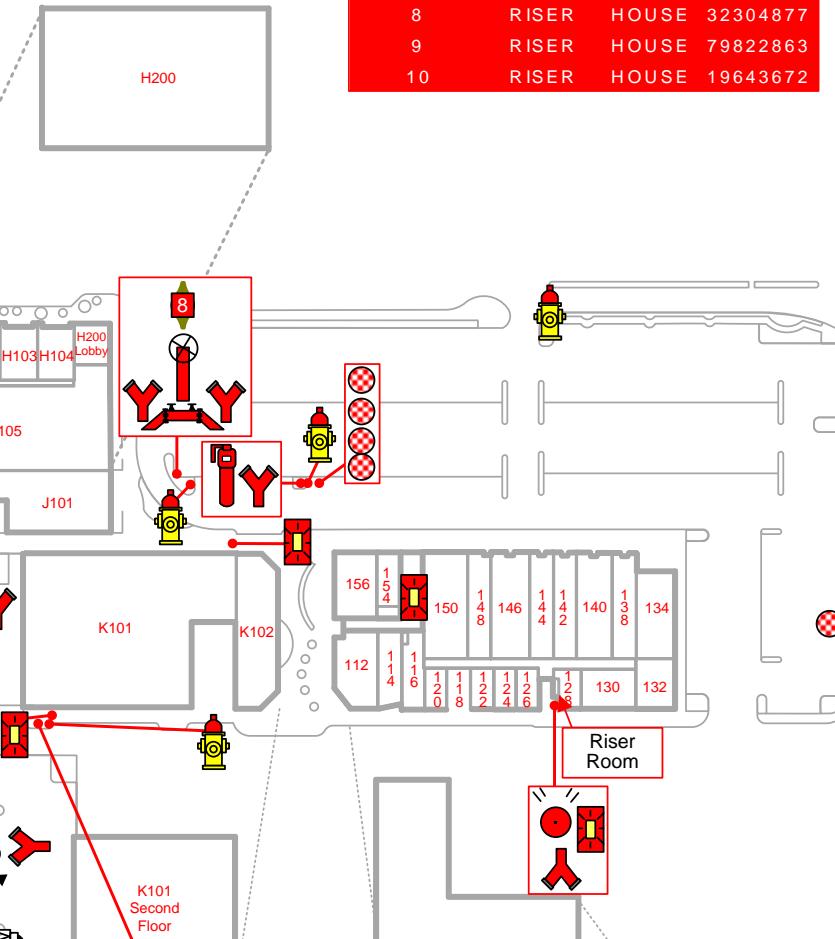

Fire Water Meter Information

Reference #	Location	Billed To	Meter #
6	GROUND	HOUSE	19643672
7	RISER	HOUSE	32304885
8	RISER	HOUSE	32304877
9	RISER	HOUSE	79822863
10	RISER	HOUSE	19643672

Fire

Page 4 of 7




	Fire Bell
	Fire Department Connection
	Fire Extinguisher
	Fire Hydrant
	Fire Light
	Flow Control Valve
	Horizontal Fire Riser
	House Fire Water Meter W/ Number
	Pull Down Fire Alarm
	Water Shutoff Fire Hydrant

Plans produced by:
ID Plans Corp
05/10/2012
(813) 657-2545



© 2012

The fire site plan identifies the locations of all fire hydrants, risers, valves and fire riser rooms, if present.

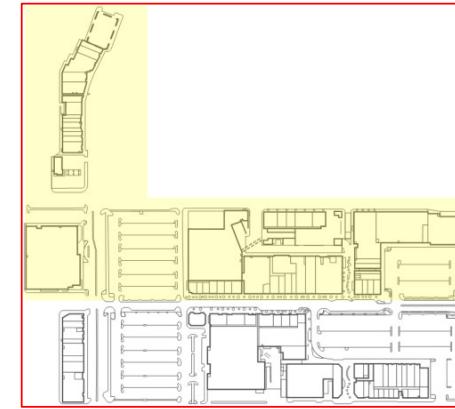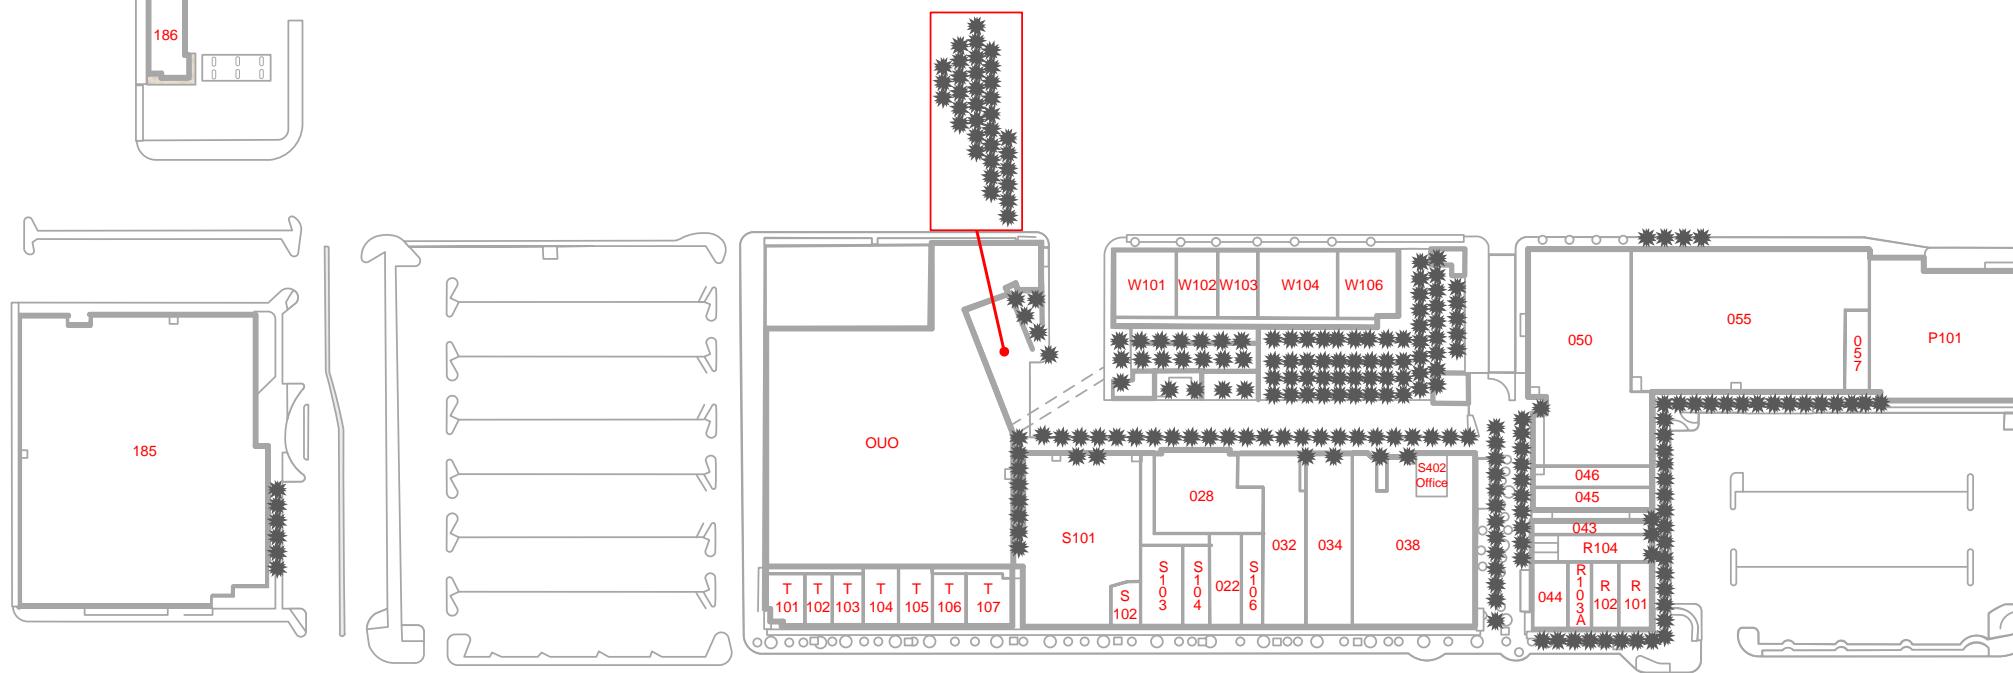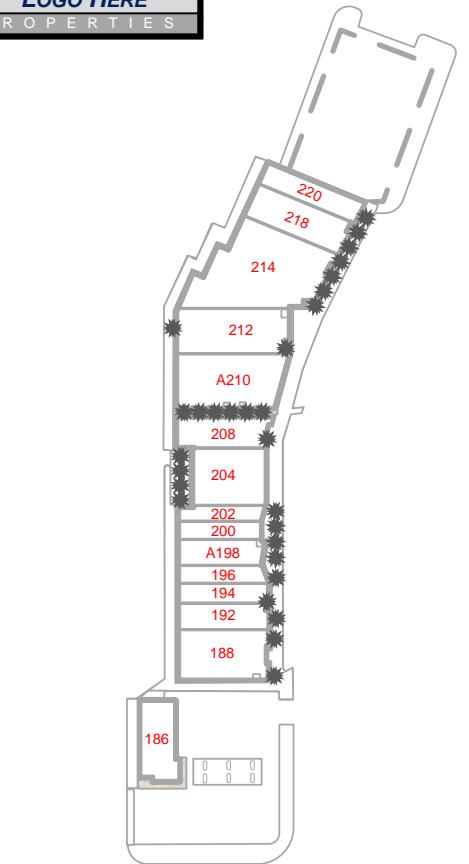

Fire

Page 5 of 7

Fire Sprinkler

Plans produced by:
ID Plans Corp
05/10/2012
(813) 657-2545



© 2012



Basic



Dimensions



Dumpster



Electric



Emergency Response



Fire



Gas



HVAC



Irrigation



Landscape



Lighting



Location



Parking



Pavement



Pylon Sign



Roof



Signage



Space





Storm



Water

The fire site plan identifies the locations of all fire hydrants, risers, valves and fire riser rooms, if present.

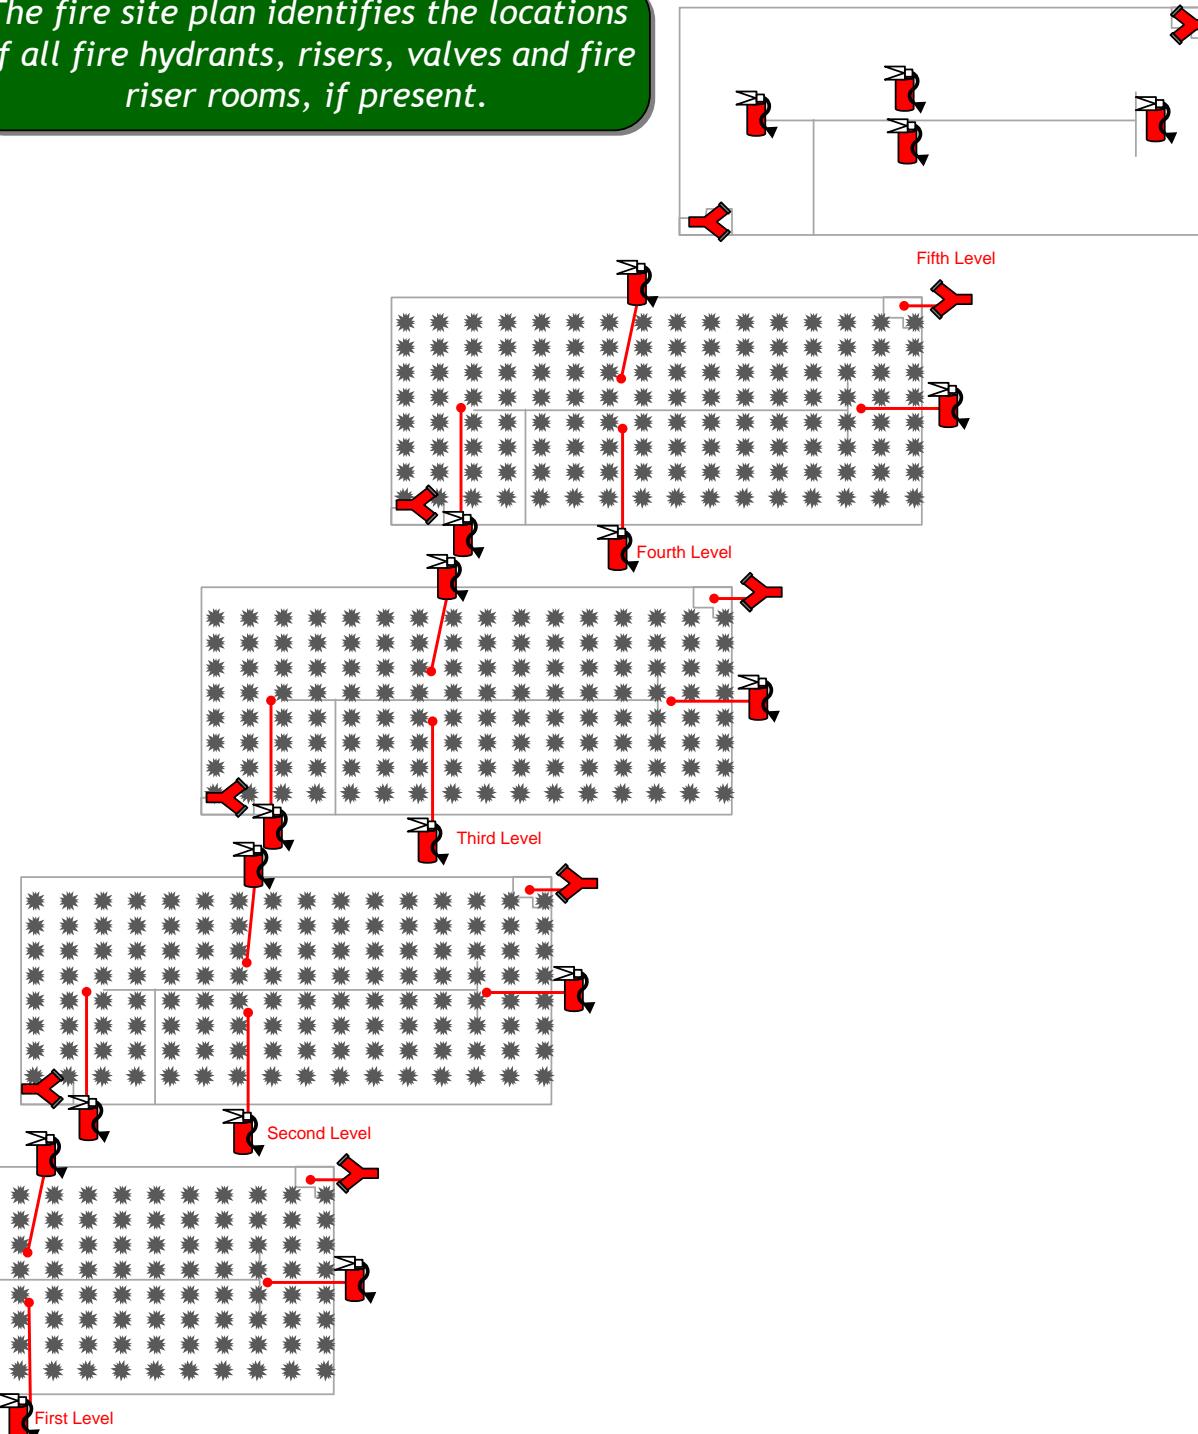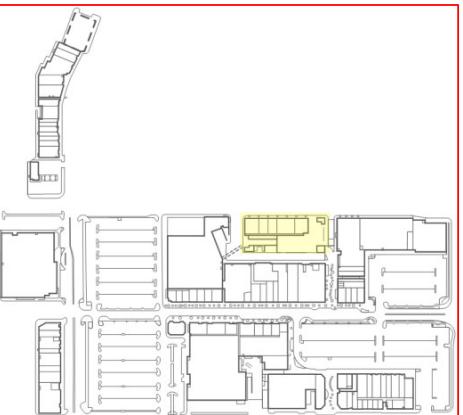

Fire


Page 6 of 7

	Fire Department Connection
	Fire Extinguisher
	Fire Sprinkler

Plans produced by:
ID Plans Corp
05/10/2012
(813) 657-2545







© 2012

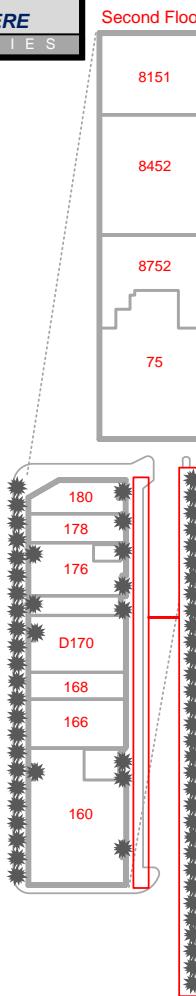

The fire site plan identifies the locations of all fire hydrants, risers, valves and fire riser rooms, if present.

Fire


Page 7 of 7

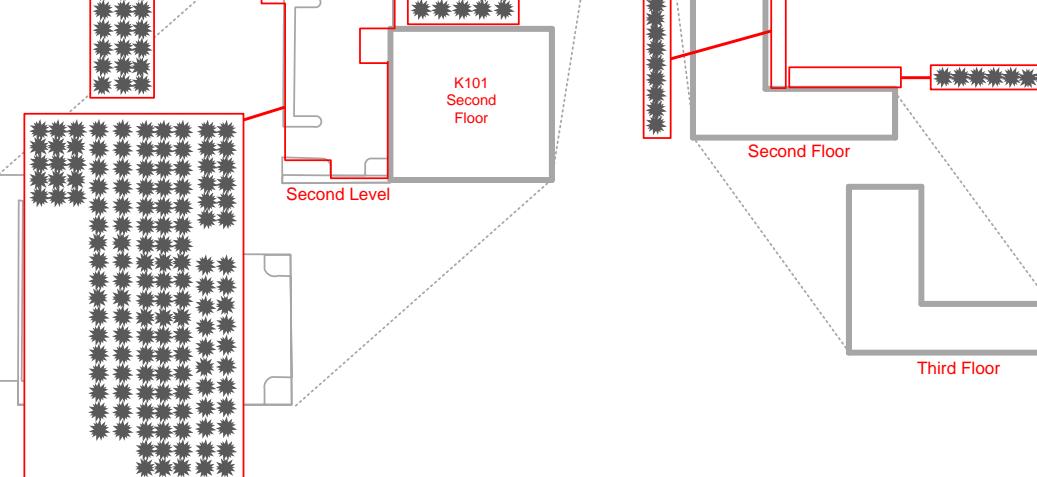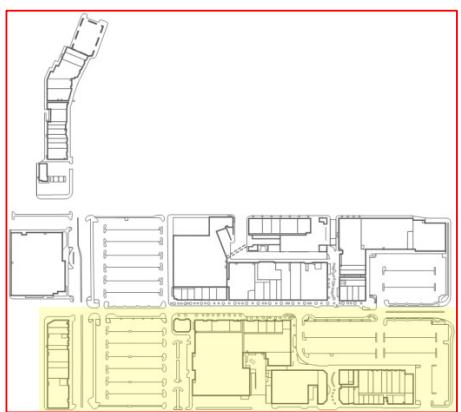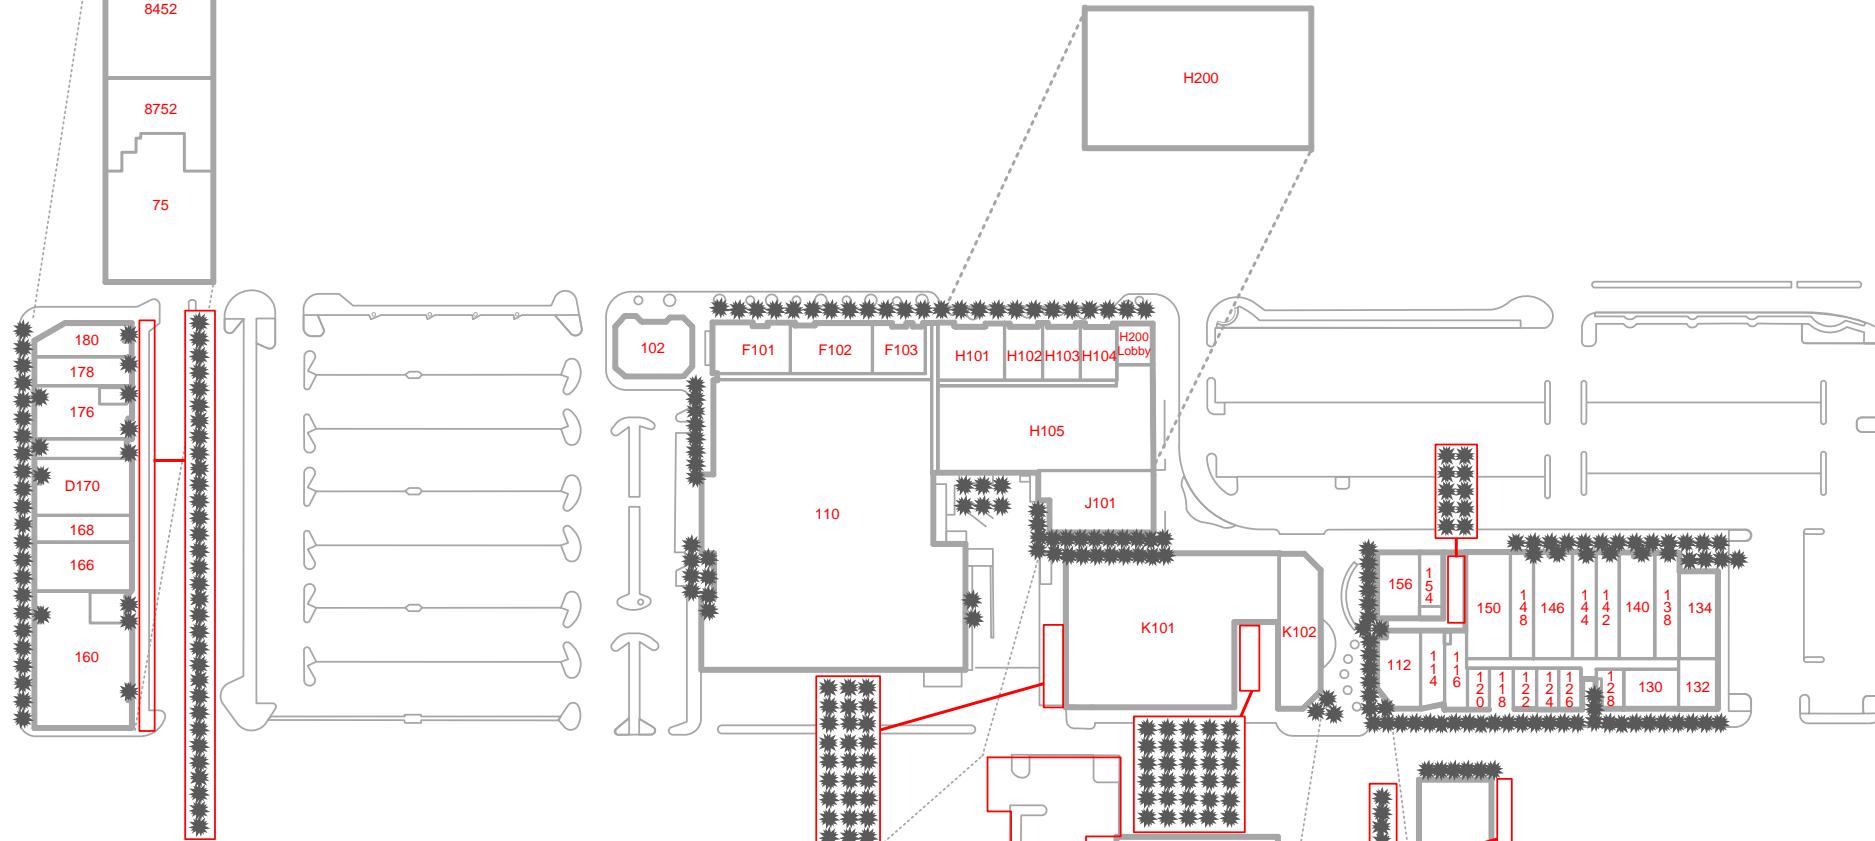 

Plans produced by:
ID Plans Corp
05/10/2012
(813) 657-2545



© 2012

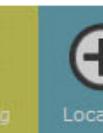

The gas site plan identifies the locations of all gas meters, the spaces they operate and the tenant, as well as gas shut-offs.

Gas Meter Information						
Reference #	Space #	Tenant Name	Meter #	Reference #	Space #	Tenant Name
1			NO METER	33		
2	218	INACTIVE	30467789	34	W 106	LITTLE FIRE POT/DIM SUM BAKERY
3	214	KING WAH RESTAURANT	45581954	35		NO METER
4	214	KING WAH RESTAURANT	33999823	36		NO METER
5	A210	AVAILABLE	792213Z	37		NO METER
6	207	KUMON LEARNING CENTER	712905C	38		NO METER
7	208	BANGKOK GARDEN	800214C	39		NO METER
8	204	UNITED STATES POST OFFICE	451260R	40	S101	FURNITURE GALLERY
9	202	MANNY'S HAIRCUT	962270C	41	028	BANANA ISLAND
10	A198	H&R BLOCK	60724582	42		NO METER
11	194	SUBWAY	34778634	43		NO METER
12			NO METER	44		INACTIVE
13	200	GENESIS DENTAL	57141414	45	034	PARTY WAREHOUSE
14	196	TIMES SALON	44364463	46	032	HOLLYWOOD VIDEO
15	192	QUICKLY	3746692	47	044	DAPHNE'S GREEK CAFE
16			NO METER	48		NO METER
17	188	WESTLAKE COIN LAUNDRY	30465259	49	043	GEORGETTE'S OF WESTLAKE
18			NO METER	50		INACTIVE
19	185	BURLINGTON COAT FACTORY	38463029	51	045	SLIDER'S DINER
20	T107	YOGURT CIRCLE	51462422	52		NO METER
21	T105	LOBELLA	52419554	53		INACTIVE
22	T102	AVAILABLE	48606338	54		ADDRESS 355 S. MAYFAIR
23	T101	SHENG KEE	47383039	55		NO METER
24			NO METER	56		ADDRESS 375 S. MAYFAIR
25	T106	TOKYO SUSHI/DAI ICHI	51471486	57		5138682X
26	T104	KICK CITY	48606327	58		ADDRESS 375 S. MAYFAIR
27	T103	AVAILABLE	52728302	59	050	51386819
28	OVO	HOME DEPOT	48492180	60	038	INACTIVE
29			NO METER	61	057	DSW SHOES
30			NO METER	62	055	36887070
31			NO METER	63	P101	BEVERLY'S
32			NO METER			60679148
			NO METER			GNC
			NO METER			34664047
			NO METER			WALGREENS
			NO METER			60549892
			NO METER			T.J. MAXX
			NO METER			60420750

Gas Company: Gas & Electric Company
Telephone Number: 800-555-1000




Plans produced by:
ID Plans Corp
05/10/2012
(813) 657-2545



© 2012



The gas site plan identifies the locations of all gas meters, the spaces they operate and the tenant, as well as gas shut-offs.

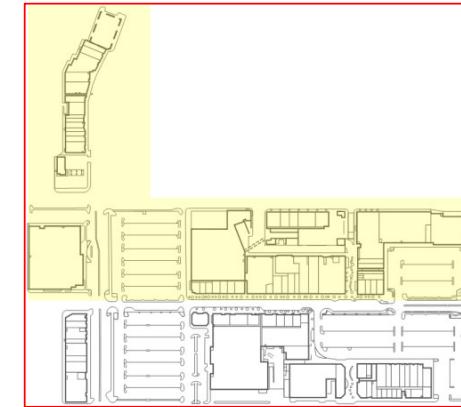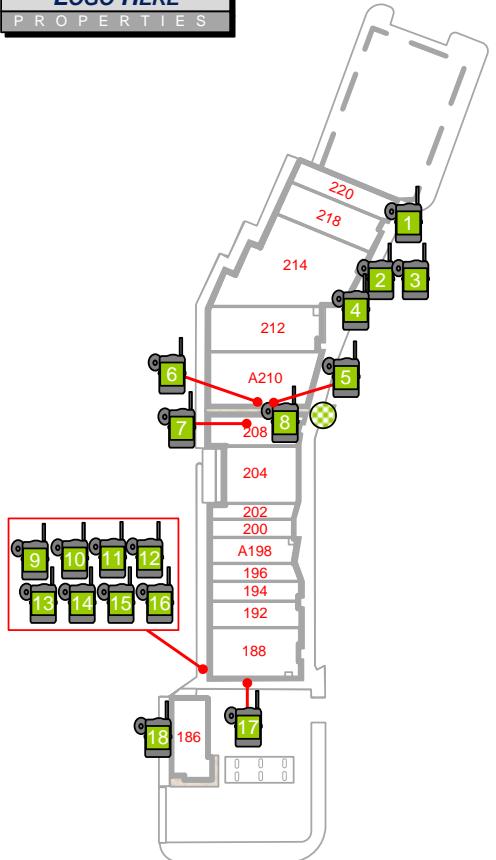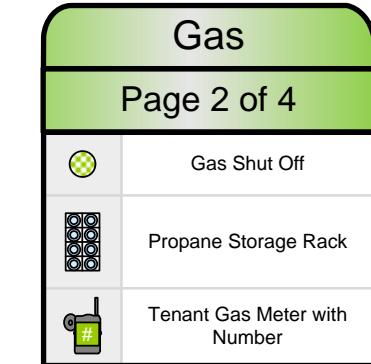

Plans produced by:
ID Plans Corp
05/10/2012
(813) 657-2545



© 2012

The gas site plan identifies the locations of all gas meters, the spaces they operate and the tenant, as well as gas shut-offs.

Gas

Page 3 of 4

Gas Meter Information							
Reference #	Space #	Tenant Name	Meter #	Reference #	Space #	Tenant Name	Meter #
64	178	PHO HUYNG HIEP 3	60159337	93		NOT ACTIVE	60679019
65			NO METER	94	110	SAFEWAY	36006025
66			NO METER	95			NO METER
67	75	2ND FLOOR	56181378	96			NO METER
68			NO METER	97			NO METER
69	8452	SETON MEDICAL CENTER	42694113	98			NO METER
70	176	PATELCO CREDIT UNION	29105175	99	156	WESTLAKE COFFEE SHOP	908035Z
71	D170	BANK OF AMERICA	3256241X	100		BOILER - 48 PARK PLAZA	54046509
72	8151	KAISER PERMANANTE HEARING CENTER	36892053	101			NO METER
73	166	HSBC	3325728X	102			NO METER
74	168	TOKYO TERIYAKI JAPANESE CUISINE	37439644	103			NO METER
75	160	CHASE	42645295	104			NO METER
76	F103	BURGERMEISTERS HAMBURGERS	60274191	105			NO METER
77	F103	BURGERMEISTERS HAMBURGERS	60107682	106	132	NATIONS GIANT HAMBURGERS	50136031
78	F101	KANA JAPANESE CUISINE	60159382	107	150	T-MOBILE	35610872
79	F102	GERRY'S GRILL	60159377	108	134	CHIPOTLE MEXICAN GRILL	60189869
80	F101	KANA JAPANESE CUISINE	60112972	109	144	UPS STORE	34744501
81	102	88 RICE BOWL	46299946	110	138	SUPERCUTS	46728484
82	H101	VERIZON WIRELESS	60153293	111	142	RED WING SHOES	32162867
83	H102	GOOD FEET	60161279	112			NO METER
84	H103	COLOR ME MINE	60138729	113			NO METER
85	H104	MIKI	60161264	114			NO METER
86	H200	COST PLUS WORLD MARKET	36879854	115	120	WESTLAKE SHOE REPAIR	48691500
87	H105	TRADER JOES	36892944	116	126	TANI'S KITCHEN	25452603
88			NO METER	117	146	BANK OF THE WEST	25807265
89			NO METER	118	148	BROASTER CHICKEN	44770220
90			NO METER	119	122	PULIDO'S TAILOR	28341654
91	K101	ROSS DRESS FOR LESS	60112974	120	130	DANCAREAL REAL ESTATE	3976873X
92			NO METER	121	128	ELITE HAIR SALON	3961781X
				122			NO METER

Gas Company: Gas & Electric Company
Telephone Number: 800-555-1000

Plans produced by:

ID Plans Corp



05/10/2012

(813) 657-2545



© 2012



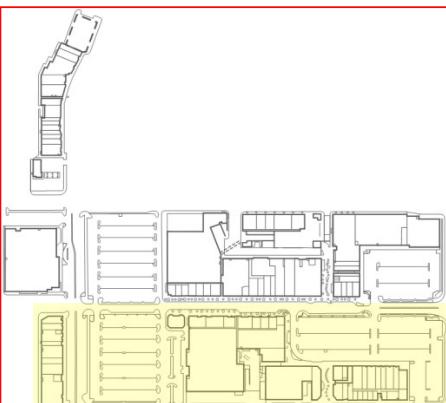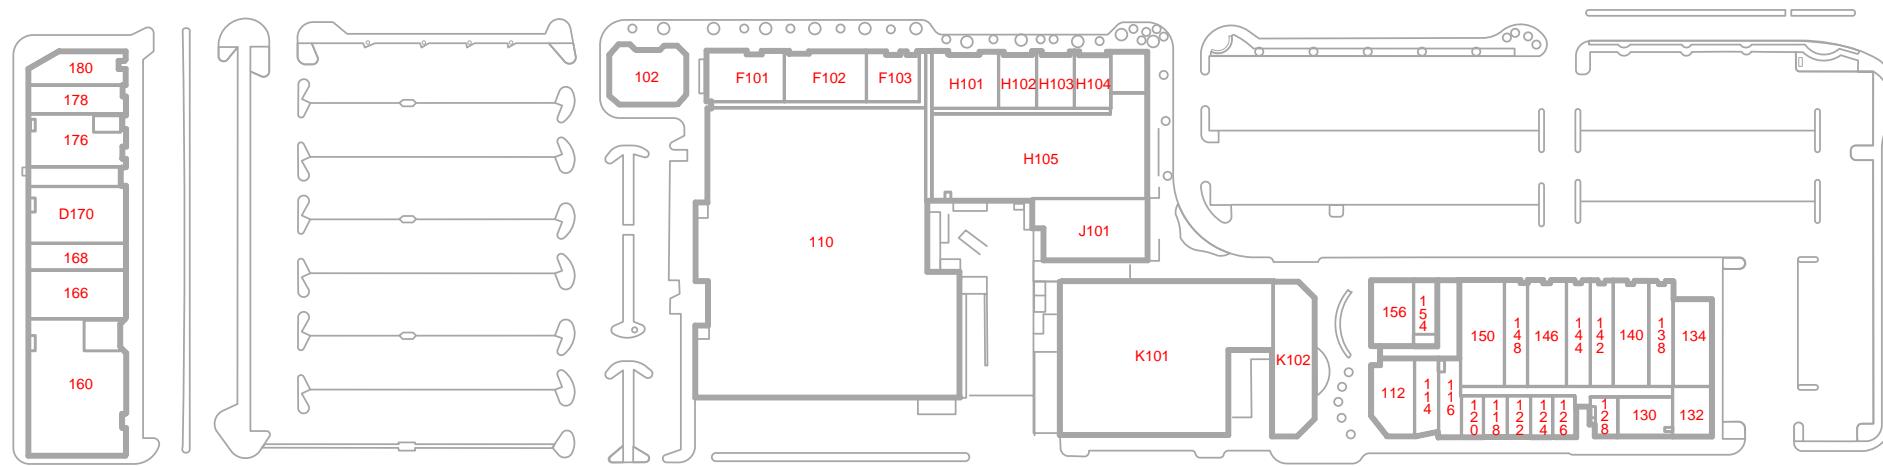

Plans produced by:

ID Plans Corp

05/10/2012

(813) 657-2545



© 2012



The HVAC site plan identifies HVAC unit locations, model numbers and serial numbers, which are located on the identification plate.

HVAC Units & Information												
Unit #	Manufacturer	Model #	Tonnage	Serial #	Year	Unit #	Manufacturer	Model #	Tonnage	Serial #	Year	
1	YORK	D1NA042N03606C	3.5	NGNM085343	2004	23	TRANE	YCD301C4HACA	25	537100672D	2005	
2	YORK	D1NA042N03606C	3.5	NGNM085342	2004	24	TRANE	YHC048A4RHA20D0C0A2B4A200	4	534100711L	2005	
3	CARRIER	48GSN060115501	5	3804G52409	2004	25	TRANE	YHC048A4RHA20D0C0A2B4A200	4	534100237L	2005	
4	AH ARCTIC CIRCLE	US670H	Evap. Coil	D06245986	2006	26	TRANE	YHC036A4RHA22D0C0A2B4A200	3	536102126L	2005	
5	FRASER JOHNSTON	NO INFORMATION	--	NO INFORMATION	--	27	TRANE	YHC060A4RLA23D0C0A2B4A200	5	536100247L	2005	
6	FRASER JOHNSTON	NO INFORMATION	--	NO INFORMATION	--	28	AH ARCTIC CIRCLE	UD320H	Evap. Coil	H06011108	2006	
7	FRASER JOHNSTON	NO INFORMATION	--	NO INFORMATION	--	29	CARRIER	48TMD007-601HE	6	0307G20458	2007	
8	FRASER JOHNSTON	NO INFORMATION	--	NO INFORMATION	--	30	CARRIER	48GSN060090601	5	4906G12294	2006	
9	FRASER JOHNSTON	NO INFORMATION	--	NO INFORMATION	--	31	CARRIER	48GSN060090601	5	3606G22128	2006	
10	CARRIER	48GSN048115511	4	3407G12402	2007	32	CARRIER	48GSN060090601	5	4206G11745	2006	
11	YORK	TCGD36S21S2A	3	W0F9919584	1997	33	CARRIER	48GSN060090601	5	3606G22131	2006	
12	CARRIER	48ESN042060501	3.5	5008G20536	2008	34	CARRIER	48GSN060090601	5	4606G31028	2006	
13	AH ARCTIC CIRCLE	US440H	Evap. Coil	D05205780	2005	35	CARRIER	48GSN060090601	5	3606G22129	2006	
14	AH ARCTIC CIRCLE	US440H	Evap. Coil	G05061706	2005	36	TRANE	NO INFORMATION	--	NO INFORMATION	--	
15	AH ARCTIC CIRCLE	NO INFORMATION	--	NO INFORMATION	--	37	TRANE	TTA240B300BD	20	N44505XAH	1998	
16	AH ARCTIC CIRCLE	NO INFORMATION	--	NO INFORMATION	--	38	BDP	548CPX036000ACAA	3	3493G85892	1993	
17	TRANE	YCD301C4HACA	25	537100660D	2005	39	LENNOX	CHP16-953-1Y	7.5	NO INFORMATION	--	
18	TRANE	TFH151C400CB	12.5	537100564D	2005	40	BDP	581APV090125AAAA	7.5	3394G30627	1994	
19	TRANE	YCD301C4HACA	25	537100677D	2005	41	BDP	581APV090125AAAA	7.5	3394G30626	1994	
20	TRANE	YCD301C4HACA	25	537100682D	2005	42	BDP	581APV048074AAAA	4	2594G20763	1994	
21	TRANE	YCD301C4HACA	25	537100643D	2005	43	AH ADOBE AIR	US940B	Evap. Coil	J01001073	2001	
22	TRANE	YCD301C4HACA	25	537100611D	2005	44	AH ADOBE AIR	H582/682	Evap. Coil	1136220	--	

Plans produced by:

ID Plans Corp

05/10/2012



(813) 657-2545




© 2012



The HVAC site plan identifies HVAC unit locations, model numbers and serial numbers, which are located on the identification plate.

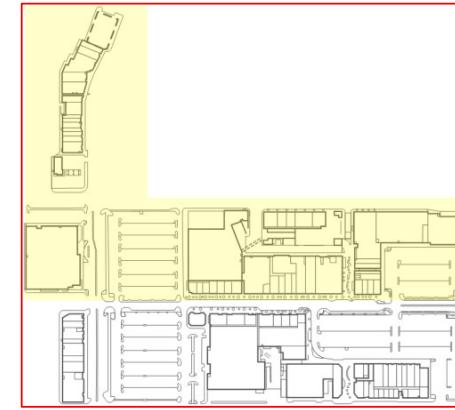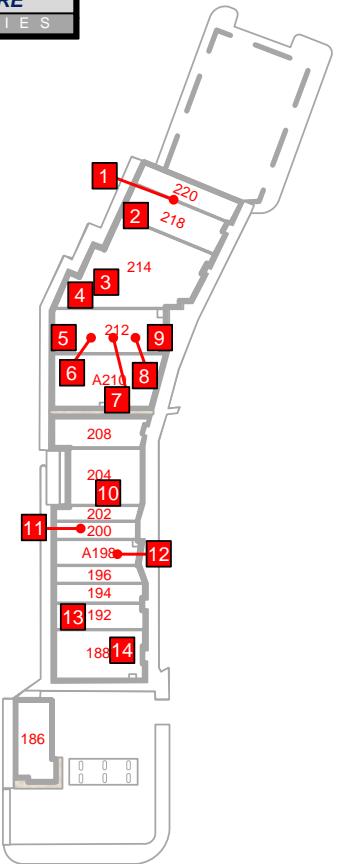

HVAC Unit # and Location

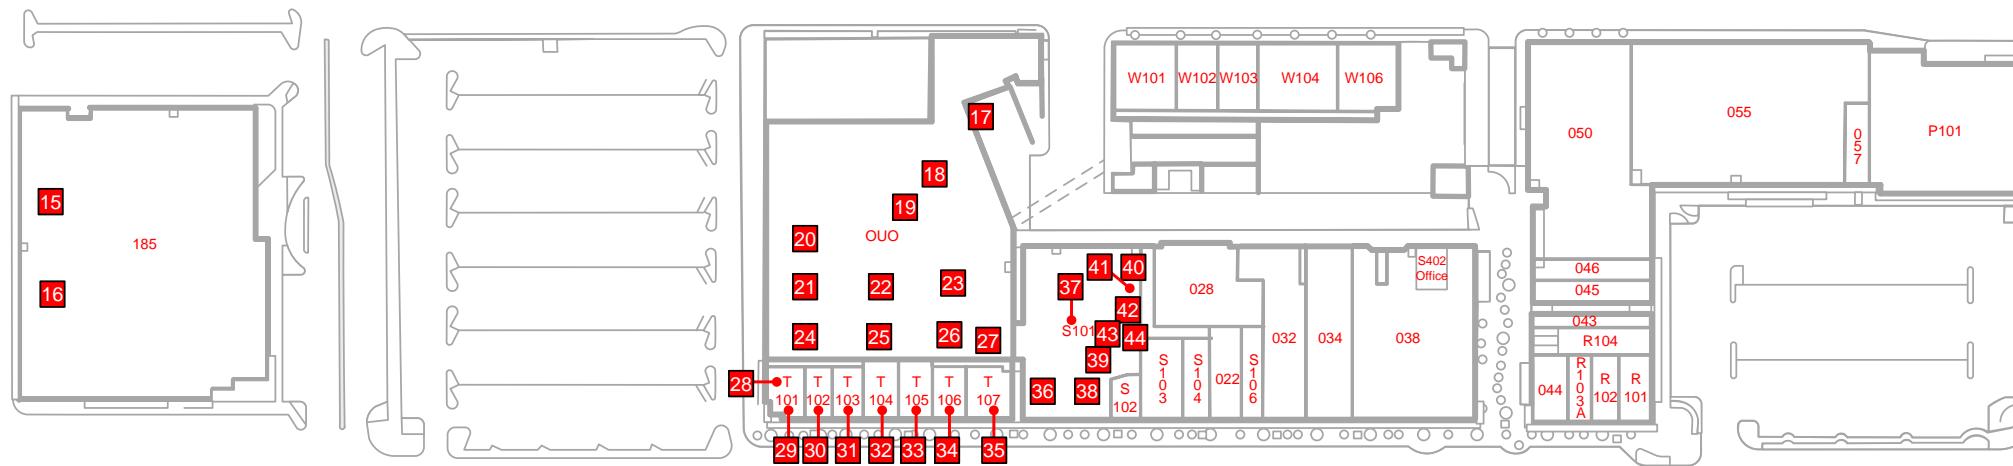

Plans produced by:
ID Plans Corp
05/10/2012
(813) 657-2545



© 2012



The HVAC site plan identifies HVAC unit locations, model numbers and serial numbers, which are located on the identification plate.

HVAC Units & Information											
Unit #	Manufacturer	Model #	Tonnage	Serial #	Year	Unit #	Manufacturer	Model #	Tonnage	Serial #	Year
45	BDP	581APV072074AAAA	6	3194G20457	1994	67	LENNOX	LGC090S2BM2Y	7.5	5607A03726	2007
46	CARRIER	50JS-060-501	5	1706G12327	2006	68	LENNOX	LGC090S2BM2Y	7.5	5607A03723	2007
47	LENNOX	CHP15-653-3Y	5	5188D13717	1988	69	LENNOX	LGC090S2BM2Y	7.5	5607A03727	2007
48	CARRIER	50JS-048-501	4	0806G31161	2006	70	LENNOX	LGC090S2BM2Y	7.5	5607A03728	2007
49	BDP	580DPV072074AAAA	6	4295G20543	1995	71	LENNOX	LGC090S2BM2Y	7.5	5607A03725	2007
50	BDP	580DPV120180ABAA	10	3595G30001	1995	72	LENNOX	LGC090S2BM2Y	7.5	5607A03724	2007
51	HEIL	PGAC36D1HC	3	L973543912	1997	73	TRANE	YCD121C3LCAA	10	M39101230D	1997
52	HEIL	PGAC36D1HC	3	L973827419	1997	74	TRANE	YCD121C3LCAA	10	M39101231D	1997
53	CARRIER	50SZ-030-301	2.5	1207G31318	2007	75	TRANE	YCD061C3HABF	5	P43103275D	1999
54	CARRIER	50SZ-024-301	2	4307G21216	2007	76	CARRIER	25HCR336A300	3	3606E23513	2006
55	HEIL	PGAC36D1HC	3	L973827377	1997	77	CARRIER	48SDN024060311CU	2	4207G41016	2007
56	LENNOX	TPA060S2N41Y	5	5806C30396	2006	78	CARRIER	48HJD007G-B651HQ	6	4507G20487	2007
57	CARRIER	25HBR348A300	4	0706E20160	2006	79	CARRIER	48HJD012G-B671HQ	10	4207G40600	2007
58	CARRIER	25HBR324A300	2	0806E12587	2006	80	CARRIER	48HJD012G-B671HQ	10	4207G40601	2007
59	TRANE	2TWA0072A3000AB	6	6075P032F	2006	81	CARRIER	25HBR318A330	1.5	1007E32148	2007
60	TRANE	2TWA0072A3000AB	6	6075P0M2F	2006	82	CARRIER	25HBR318A330	1.5	0407E17568	2007
61	TRANE	TWA090A300FB	7.5	6123MGKAD	2006	83	CARRIER	48HJD012G-B671HQ	10	4207G40603	2007
62	AH ARCTIC CIRCLE	ES630H	Evap. Coil	B06284164	2006	84	CARRIER	48HJL005G-B651HQ	4	4207G50506	2007
63	TRANE	TCC018F100BG	1.5	52043M02H	2005	85	CARRIER	48HJD012G-B671HQ	10	4207G40598	2007
64	CARRIER	50TCQA06A2A5A0A0A0	5	2809G203099	2009	86	CARRIER	48HJL005G-B651HQ	4	4207G50505	2007
65	CARRIER	24ACA448A300	4	3806E01182	2006	87	CARRIER	48HJD012G-B671HQ	10	4207G40599	2007
66	LENNOX	LGC072S2BSY	6	5607A04124	2007	88	CARRIER	48HJD012G-B671HQ	10	4207G40602	2007


Plans produced by:
ID Plans Corp
05/10/2012
(813) 657-2545



© 2012



The HVAC site plan identifies HVAC unit locations, model numbers and serial numbers, which are located on the identification plate.

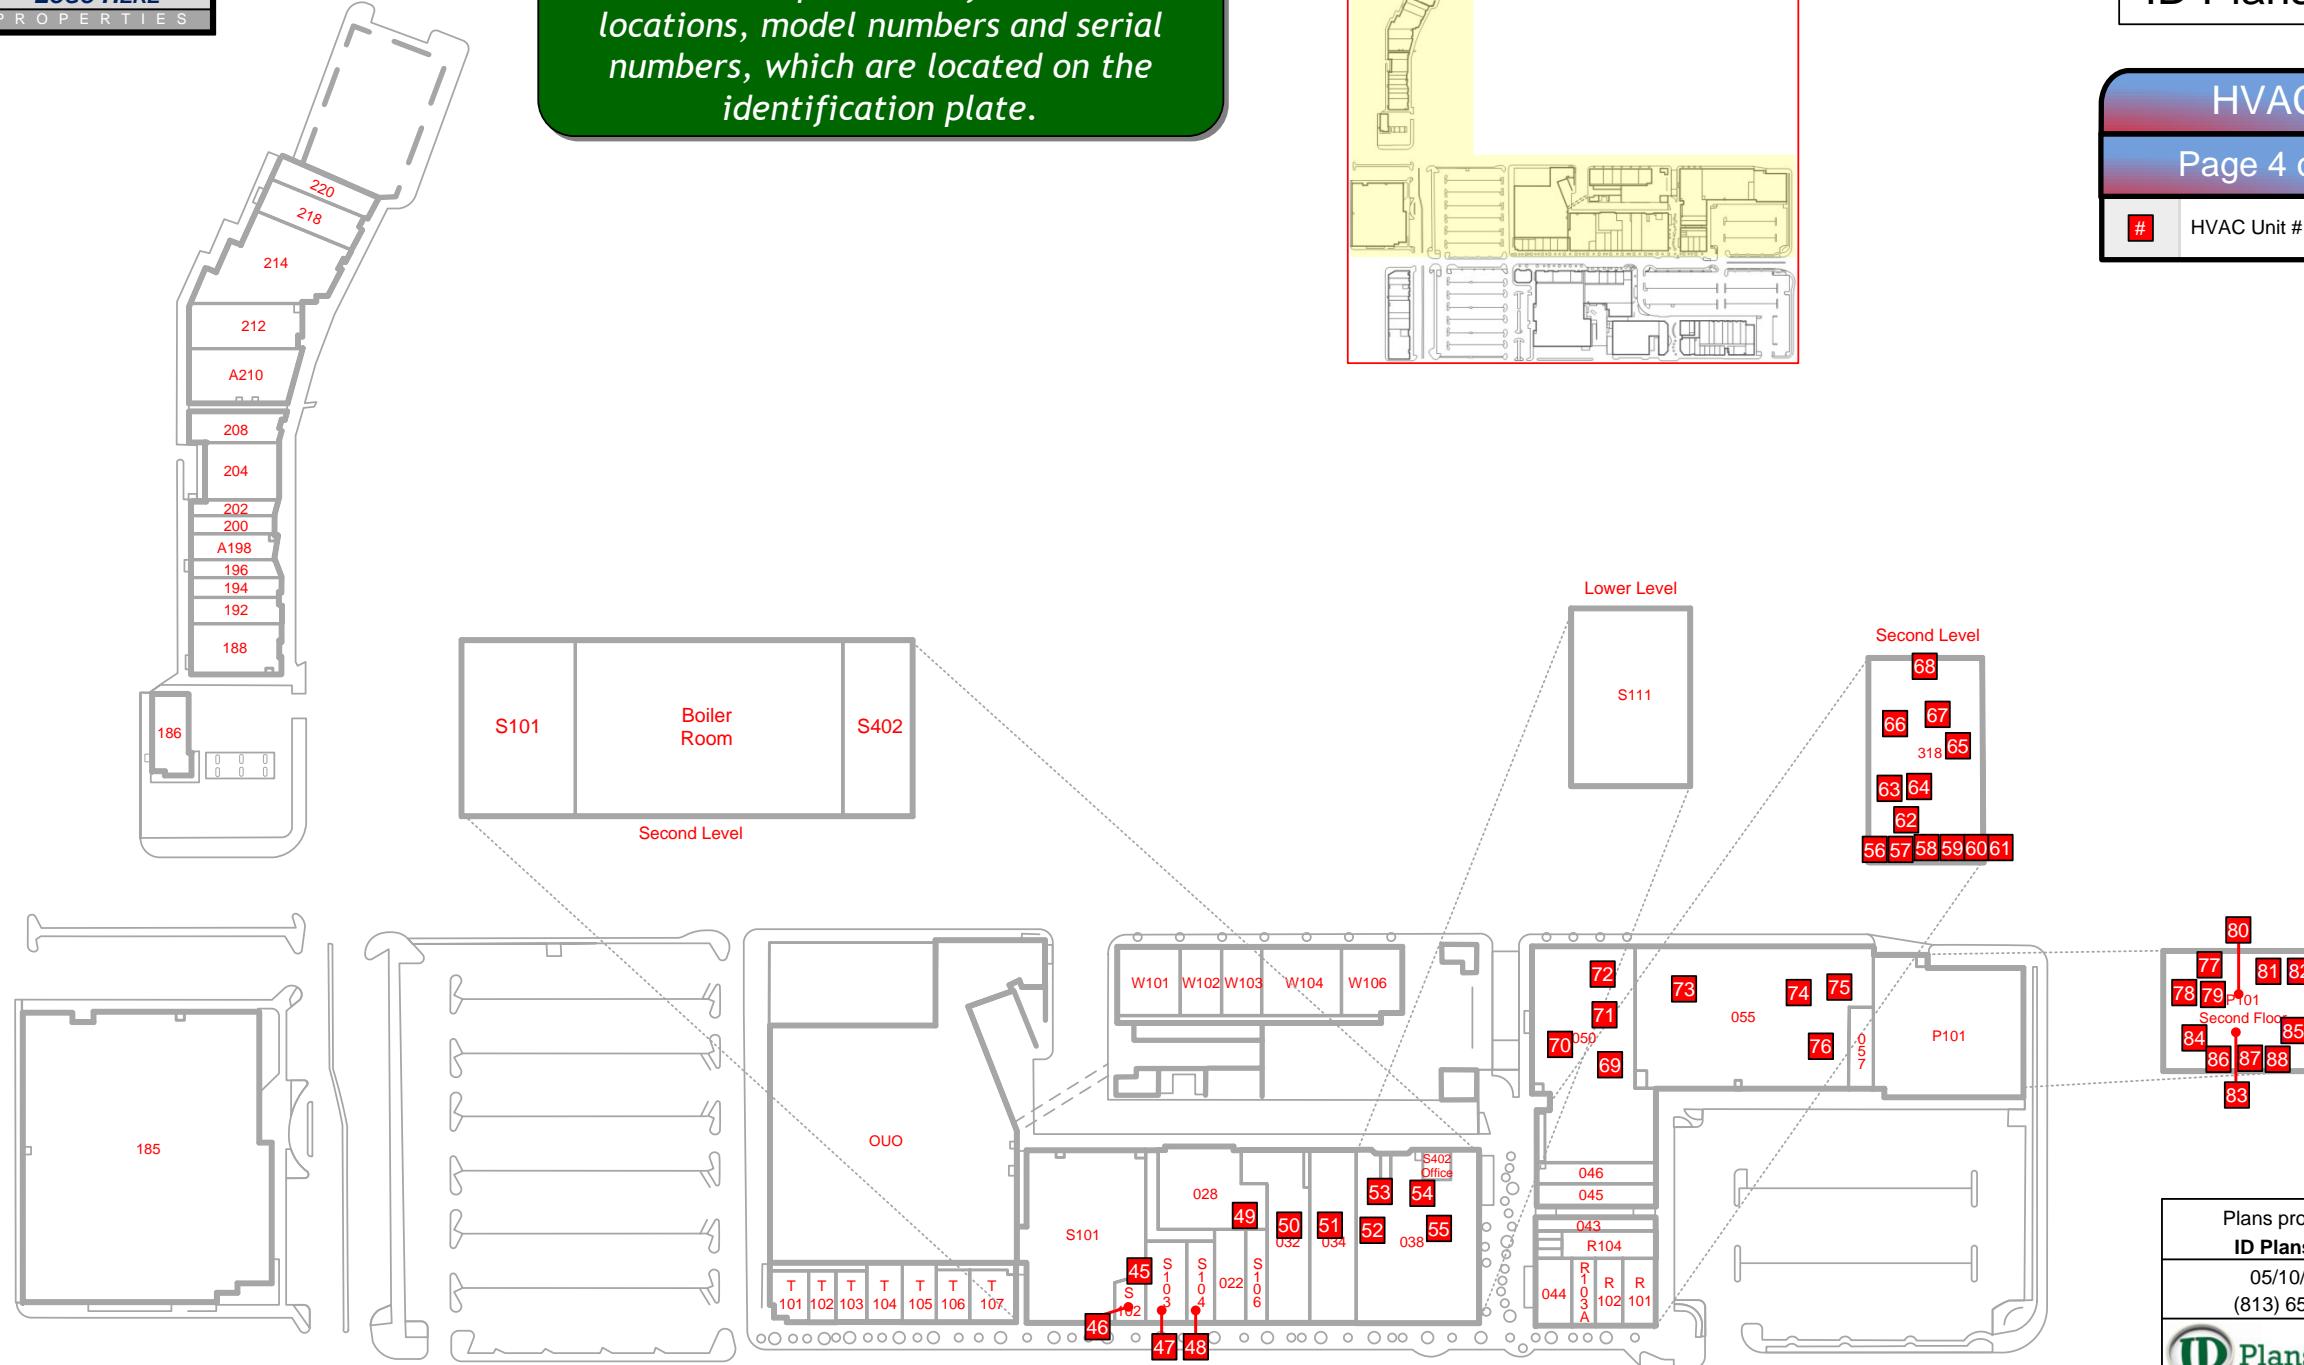

The HVAC site plan identifies HVAC unit locations, model numbers and serial numbers, which are located on the identification plate.

HVAC Units & Information

Unit #	Manufacturer	Model #	Tonnage	Serial #	Year	Unit #	Manufacturer	Model #	Tonnage	Serial #	Year
89	CARRIER	48GXN030060301	2.5	3600G10101	2000	115	CARRIER	48GSN036060501	3	4100G14527	2000
90	CARRIER	48GSN018040301	1.5	1601G11341	2001	116	CARRIER	48GSN036060501	3	4100G14524	2000
91	AH/ESSICK	5500SD/N55S	Evap. Coil	PC56924	--	117	CARRIER	48TCDD12A2G5A0A0A0	10	2409G20462	2009
92	CARRIER	48GXN024040301		0701G10114	2001	118	CARRIER	48GSN036060501	3	4100G14525	2000
93	PAYNE	PH10JA048-A	4	2901E04204	2001	119	CARRIER	50JX-024-301	3	5100G10502	2000
94	CARRIER	38HDC018341	1.5	1201X03533	2001	120	CARRIER	48GSN036060501	4	4100G10223	2000
95	CARRIER	48GXN030060301	2.5	1001G10265	2001	121	CARRIER	48GSN048090501	4	4100G10123	2000
96	CARRIER	48GXN030060301	2.5	1001G10266	2001	122	CARRIER	38YRA060300	5	3595E01759	1995
97	CARRIER	38EH060330	5	4588E00059	1988	123	CARRIER	38BRC030320	2.5	3704E07706	2004
98	CARRIER	48GXN024040301	2	0701G10116	2001	124	CARRIER	38BRB042300	3.5	1095E24437	1995
99	CARRIER	48GXN030060301	2.5	0201G14674	2001	125	CARRIER	38BRC048370	4	3404E15299	2004
100	TRANE	2TWB0042A1000AB	3.5	43833KC4F	2004	126	CARRIER	48GSN048090501	4	4100G10120	2000
101	TRANE	2TWB0042A1000AB	3.5	43834BN4F	2004	127	CARRIER	48GSN036060501	3	4100G14526	2000
102	CARRIER	48HJE004-541	3	1405G10308	2005	128	CARRIER	48GSN048090501	4	2200G10032	2000
103	CARRIER	48HJD007-551	6	0206G30407	2006	129	CARRIER	48GSN036060501	3	4100G10228	2000
104	CARRIER	48HJE004-541	3	1405G10307	2005	130	CARRIER	48GSN060090501	5	4000G14485	2000
105	TRANE	2TWX4048A1000AA	4	4444JX12F	2004	131	YORK	D3CG120N16525J5B	10	NKDM083130	1995
106	TRANE	2TWX4048A1000AA	4	4411LGT2F	2004	132	YORK	D1CG072N0792513	6	NMDM102767	1995
107	TRANE	2TWX4060A1000AA	5	5051UJX2F	2005	133	YORK	D3CG120N16525J5B	10	NKDM083129	1995
108	TRANE	2TWX4060A1000AA	5	5052WEX2F	2005	134	AH ARES	NO INFORMATION	--	NO INFORMATION	--
109	CARRIER	48HJE004-541	3	0306G20416	2006	135	CARRIER	48HJD012-571	10	3306G12050	2006
110	CARRIER	48HJD007-551	6	0206G40293	2006	136	AH ARCTIC CIRCLE	UD670H	Evap. Coil	H06243241	2006
111	CARRIER	48HJE004-541	3	0306G20421	2006	137	AH ARCTIC CIRCLE	UD670H	Evap. Coil	H06243242	2006
112	MITSUBISHI	PUY-A12NHA3	1	95U00550C	2000	138	CARRIER	48HJD006-641	5	0706G10445	2006
113	SANYO	C1852	1.5	28451	--	139	AH ESSICK	7500DD	Evap. Coil	TC42375	--
114	CARRIER	48GSN048090501	4	2200G10047	2000						

Plans produced by:

ID Plans Corp





05/10/2012

(813) 657-2545



© 2012



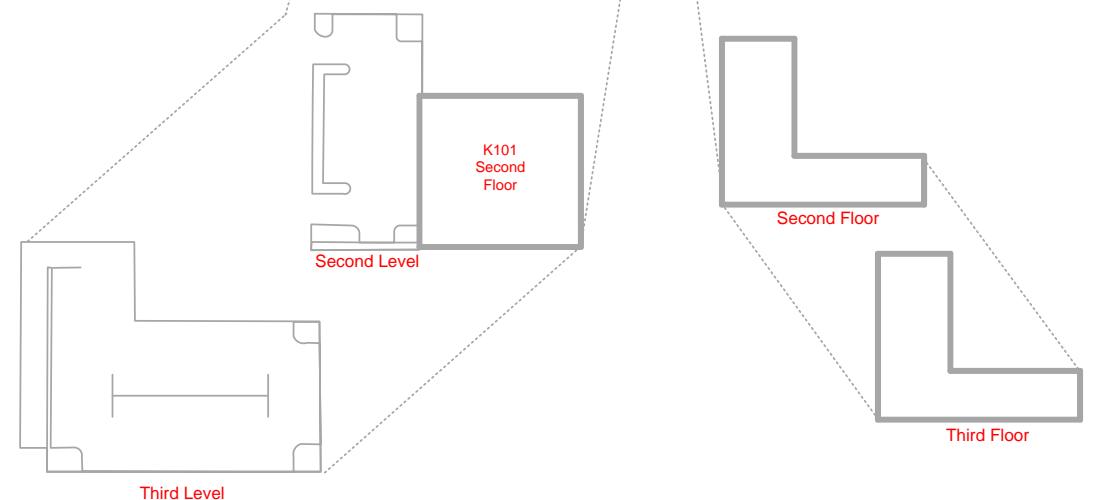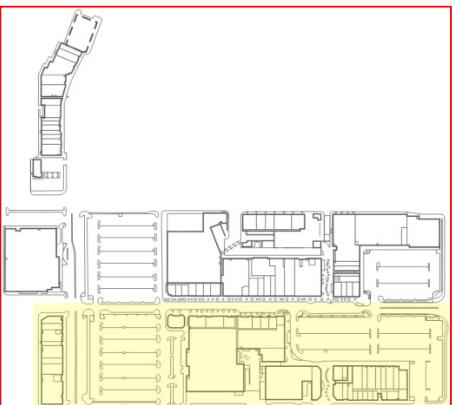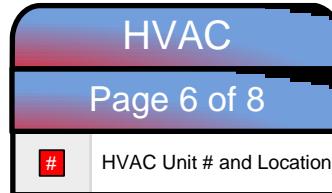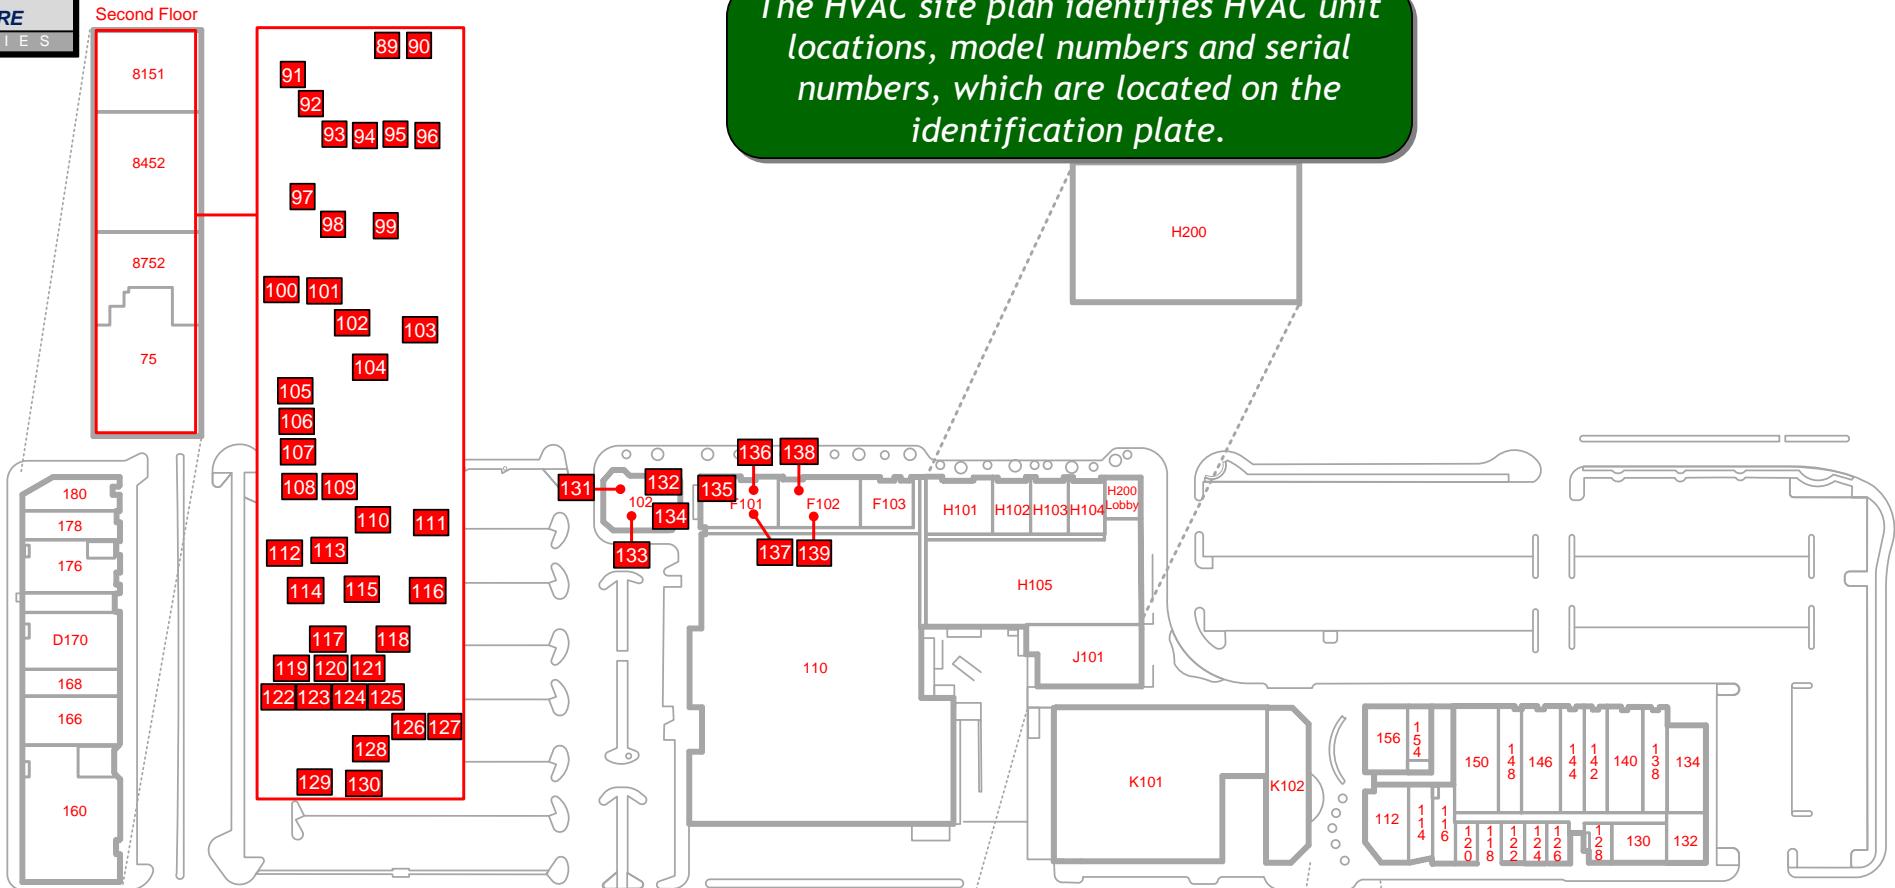

Plans produced by:
ID Plans Corp
05/10/2012
(813) 657-2545



© 2012

The HVAC site plan identifies HVAC unit locations, model numbers and serial numbers, which are located on the identification plate.

HVAC Units & Information												
Unit #	Manufacturer	Model #	Tonnage	Serial #	Year	Unit #	Manufacturer	Model #	Tonnage	Serial #	Year	
140	CARRIER	48HJD005-651	4	0506G50356	2006	166	SANYO	C3672R	3	53262	--	
141	CARRIER	48HJD005-651	4	1306G10357	2006	167	TRANE	WCD180B40AHA	15	613100523D	2006	
142	AH ESSICK	7500SD	Evap. Coil	PC64130	--	168	TRANE	TWE240B400EL	20	6141NNSHD	2006	
143	CARRIER	48GSN048090511	4	1805G51390	2005	169	TRANE	TWE240B400EL	20	6136T09HD	2006	
144	AH ESSICK	ECR3301	Evap. Coil	HD310074	--	170	TRANE	TWE240B400EL	20	6141L5WHD	2006	
145	CARRIER	48GXN060090511	5	0605G20972	2005	171	TRANE	TWA240B400FB	20	6111UCGAD	2006	
146	CARRIER	38AN012320	1	5204Y21208	2004	172	TRANE	TWA240B400FB	20	6105TBPAD	2006	
147	CARRIER	48GXN024060321	2	0705G51206	2005	173	TRANE	TWA240B400FB	20	6092S4NAD	2006	
148	AH ESSICK	ECR3301	Evap. Coil	HD310090	--	174	AH DAYTON	4YC836	Evap. Coil	07C02597	2007	
149	TRANE	YCD360AEHL0A6EB1A000000H00000	30	C03L10375	1988	175	AH DAYTON	4YC836	Evap. Coil	07C02599	2007	
150	TRANE	YSC048A3RLA1F0000000000000000	4	445101442L	2004	176	AH DAYTON	4YC836	Evap. Coil	06J04831	2006	
151	TRANE	YSC048A3RLA1U0000000000000000	4	528101489L	2005	177	AH DAYTON	4YC836	Evap. Coil	07B05292	2007	
152	TRANE	YSC048A3RLA1V0000000000000000	4	529102026L	2005	178	AH DAYTON	4YC836	Evap. Coil	06J04668	2006	
153	TRANE	YSC120A4EMA1S0000000000000000	10	504101653L	2005	179	CARRIER	48TCDD12A2G5A0A0A0	10	3309G30521	2009	
154	TRANE	YSC072A4RLA1MC000C1A00000	6	509101738L	2005	180	CARRIER	48TCLA04A2A5A0A0A0	3	3809G30258	2009	
155	TRANE	YSC120A4RLA1TC100C1A00000	10	509101774L	2005	181	AH CHAMPION	5500DM	Evap. Coil	ZM21282	N/A	
156	TRANE	YSC120A4RLA1TC100C1A00000	10	509101596L	2005	182	LENNOX	TGA090S2BS1Y	7.5	5606J06586	2006	
157	TRANE	YSC060A4ELA1F0000000000000000	5	418102197L	2004	183	LENNOX	TGA060B2BS1Y	5	5606C17844	2006	
158	TRANE	YSC120A4RLA1TC100C1A00000	10	509101834L	2005	184	TRANE	TWA060C300A2	5	L15543HFF	1996	
159	TRANE	YSC120A4RLA1TC100C1A00000	10	509101536L	2005	185	TRANE	YSC072A3ELA39000000000000	6	912100259L	2009	
160	LENNOX	LGC210H2BS2G	17.5	5606F13619	2006	186	TRANE	YHC092A3RMA2PH0C3A2A000B0	7.5	751101475L	2007	
161	LENNOX	LGC210H2BS2G	17.5	5606F13618	2006	187	AH CAPTIVEAIRE	A1-D250-G10	Make Up Air	699419	--	
162	LENNOX	LGC210H2BS2G	17.5	5606F13617	2006	188	TRANE	YHC120A3RMA2TH0C3A2A000B0	10	751101447L	2007	
163	LENNOX	LGC210H2BS2G	17.5	5606F13616	2006	189	AH ARES	SE-1CE2E	Evap. Coil	A2079	--	
164	YORK	E1RD060S46B	5	W0C8689262	1994	190	CARRIER	48HJE004-541	3	0906G50429	2006	
165	YORK	EA120C00A4AA1A	10	NOL7367705	2002							

Plans produced by:

ID Plans Corp



05/10/2012

(813) 657-2545



© 2012




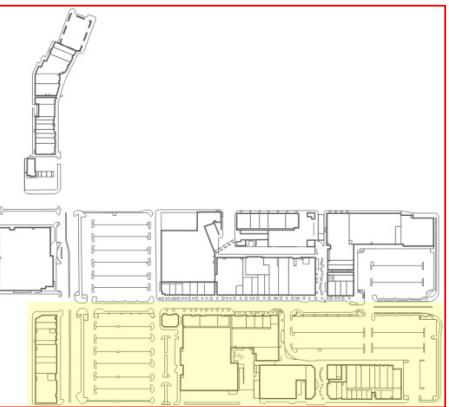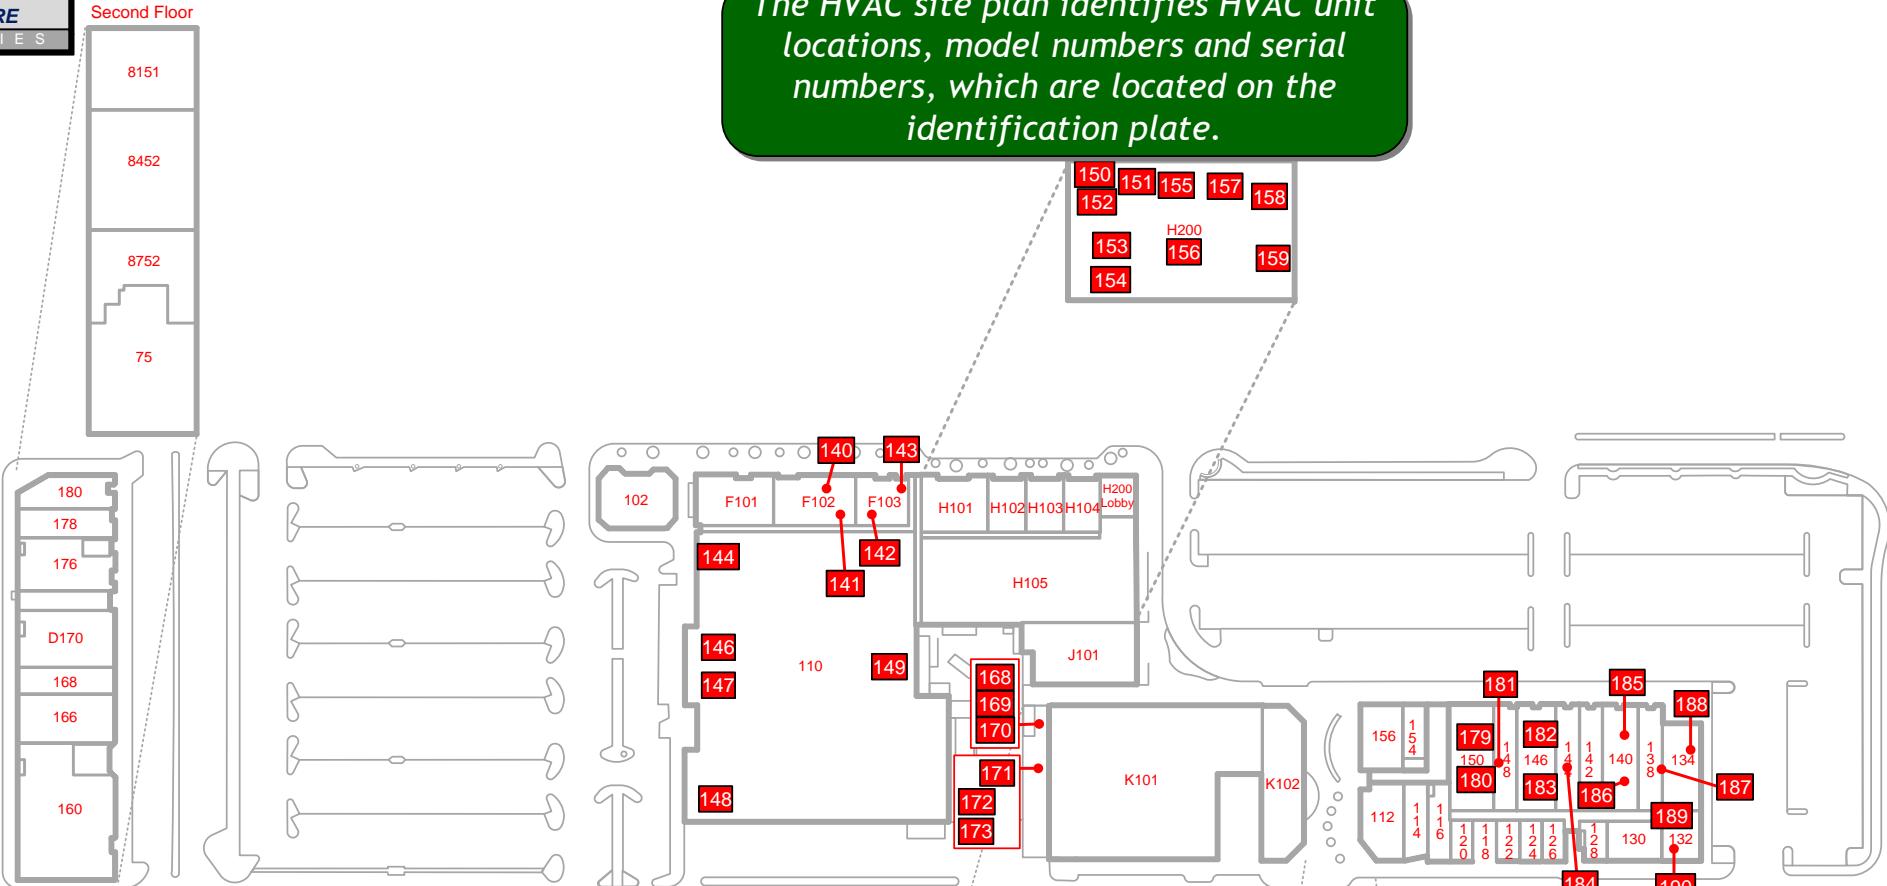

Plans produced by:
ID Plans Corp
05/10/2012
(813) 657-2545






© 2012

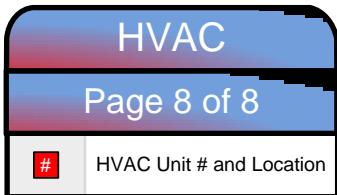


Page 8 of 8

HVAC Unit # and Location

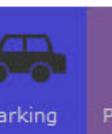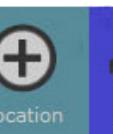

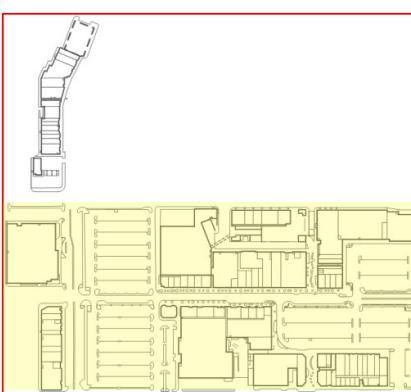

The irrigation site plan identifies the locations of all valves and the zones that they operate. It details underground wire tracking, timer locations and type, as well as the water source.

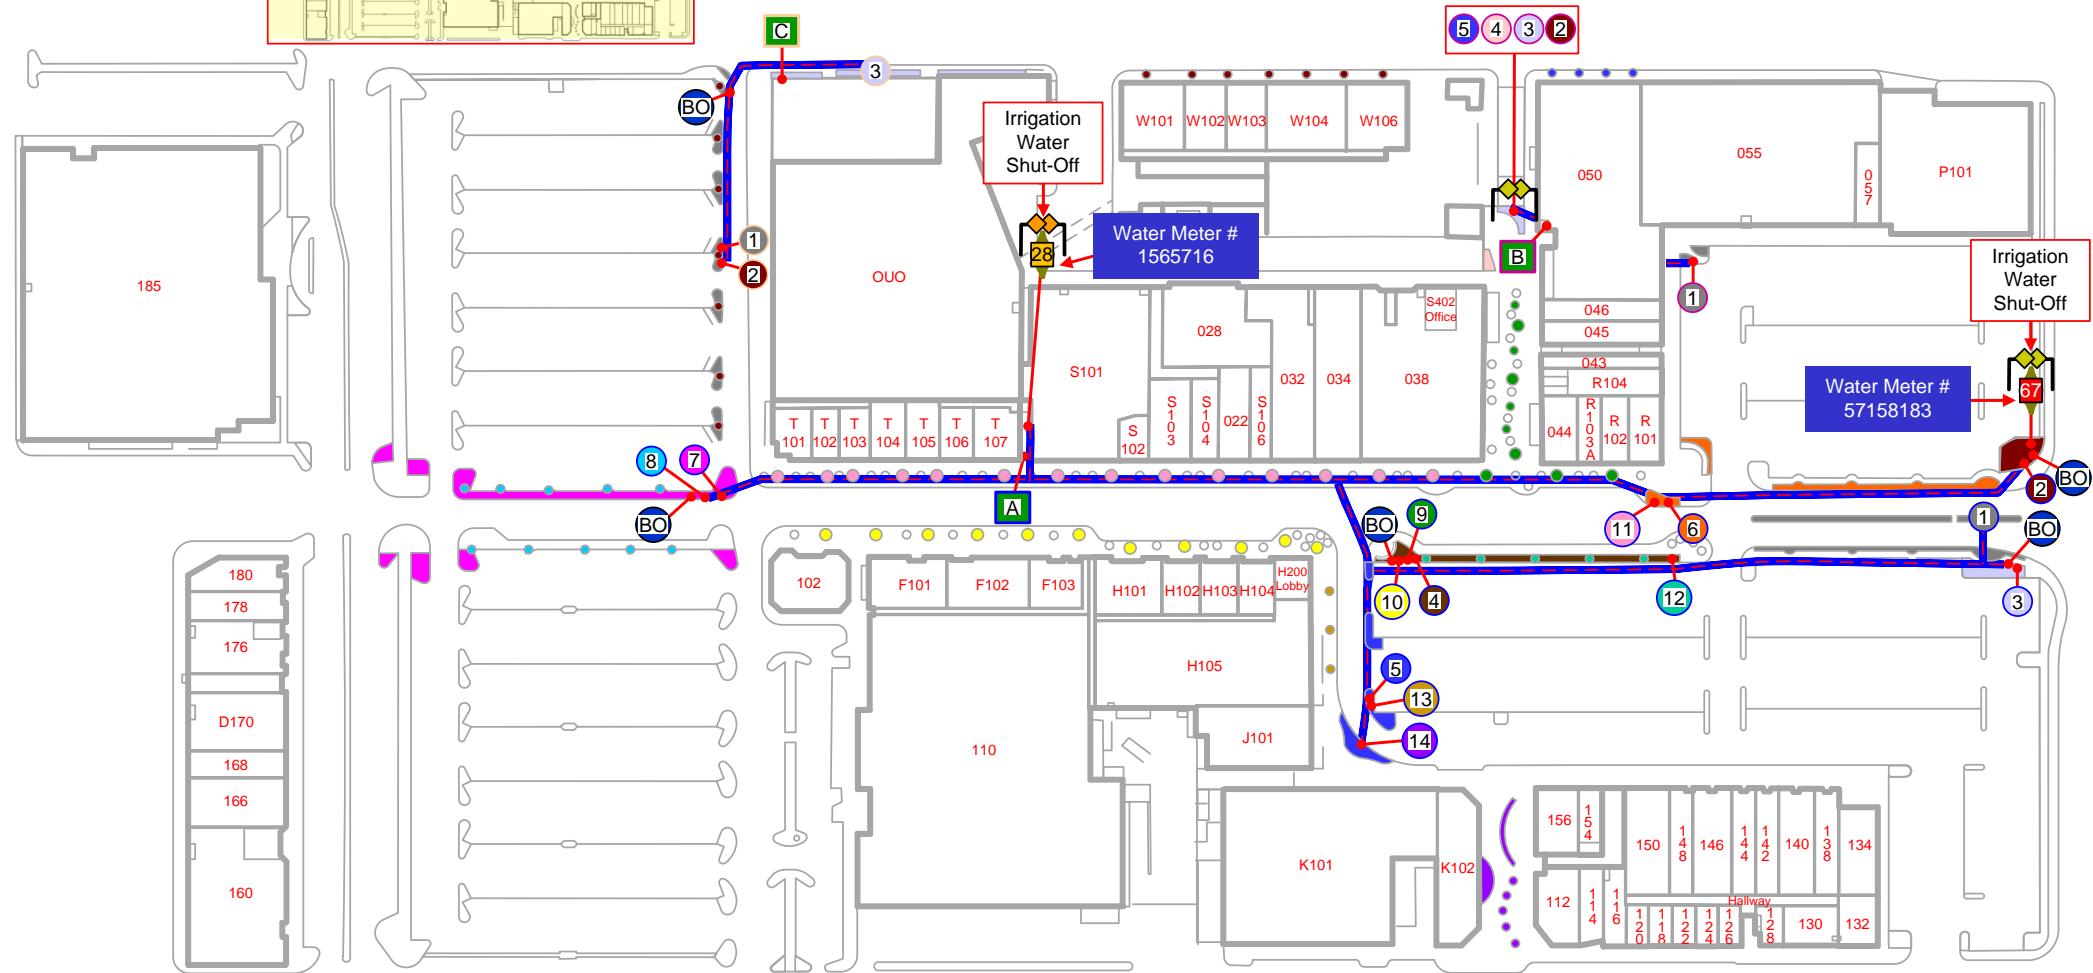

Irrigation Company: _____
Telephone Number: _____

Plans produced by:
ID Plans Corp
05/10/2012
(813) 657-2545




© 2012


Irrigation	
	2" Backflow Preventer
	4" Backflow Preventer
	Blow-out Valve
	House meter with Number
	Irrigation Controller
	Main Water and Wire Path
	Sub Water Meter
	Total Number of Zones
	Zone Valve # and Location

Type of Controller
RainBird ESP-24MC 24 Station / 14 Wired
Irritrol RD 600 6 Station / 5 Wired
Irritrol MS 4 Plus 4 Station / 3 Wired



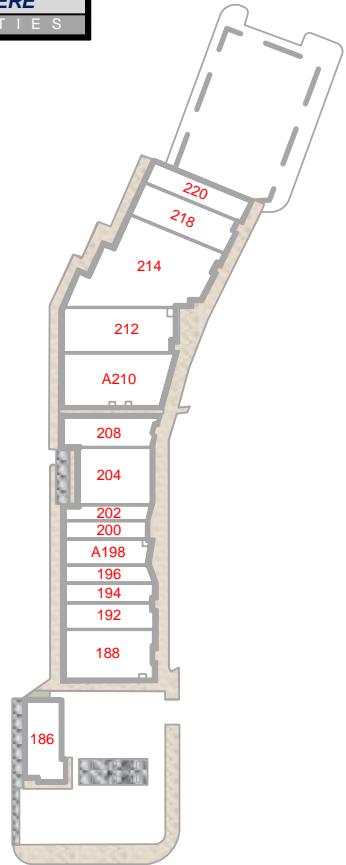


The landscape site plan identifies the hardscape from greenscape, as well as concrete areas and any water areas.

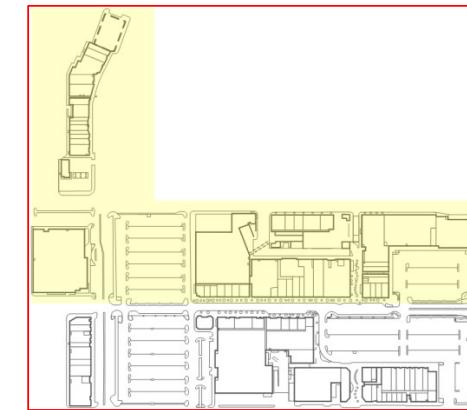

Landscape
Page 1 of 3

ESTIMATED SQUARE FOOTAGE		
Asphalt	[Grey Box]	287,864
Brick Pavers	[Pink Box]	9,290
Concrete	[Grey Box]	24,143
Landscape	[Green Box]	9,227
Sidewalks	[Yellow Box]	88,218

Landscaping Company: Green Landscape
Telephone Number: 888-555-2220


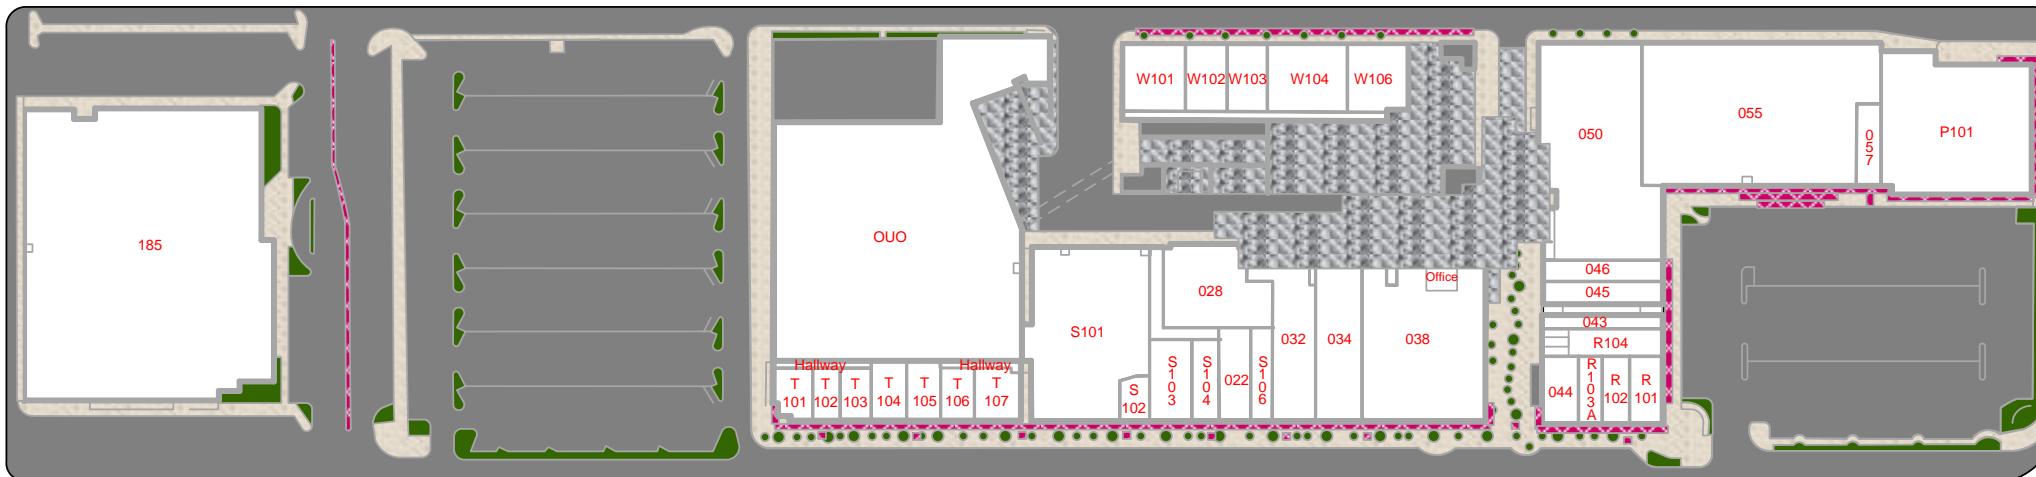


Plans produced by:
ID Plans Corp
05/10/2012
(813) 657-2545




© 2012


The landscape site plan identifies the hardscape from greenscape, as well as concrete areas and any water areas.

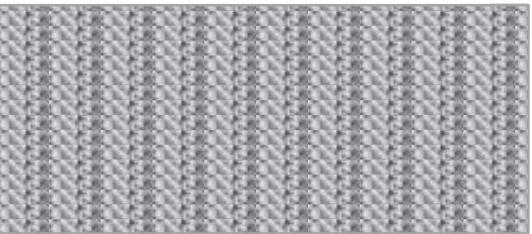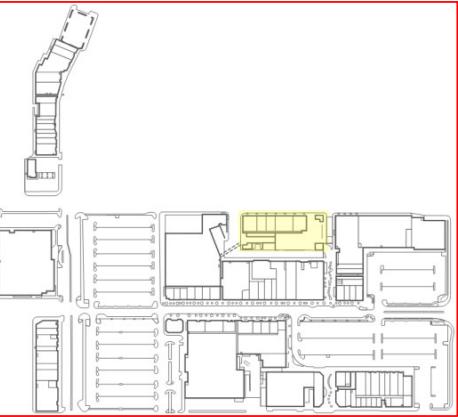


Fifth Level

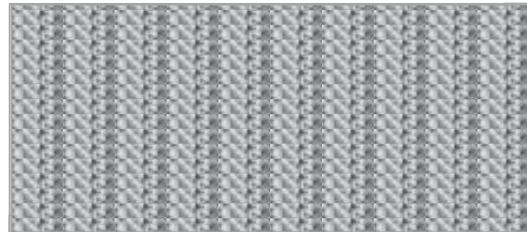


Fourth Level

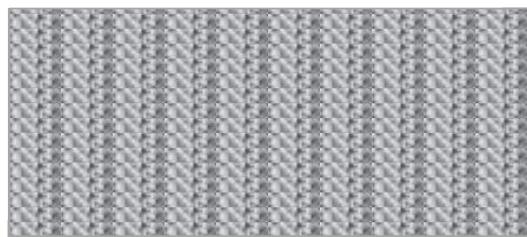

Third Level

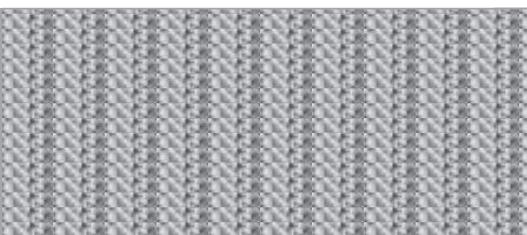

Second Level

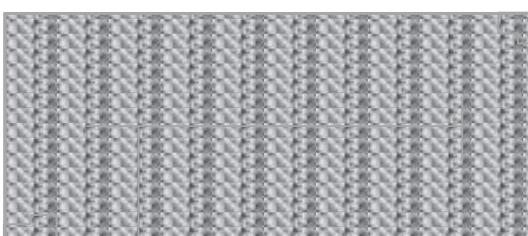

First Level

Landscape

Page 2 of 3

ESTIMATED SQUARE FOOTAGE

Concrete 211,469

Plans produced by:
ID Plans Corp
05/10/2012
(813) 657-2545





© 2012



The landscape site plan identifies the hardscape from greenscape, as well as concrete areas and any water areas.

Landscape
Page 3 of 3

ESTIMATED SQUARE FOOTAGE		
Asphalt		362,228
Brick Pavers		9,403
Concrete		72,812
Landscape		14,293
Mulch		1,389
Shrubs		6,633
Sidewalks		69,878

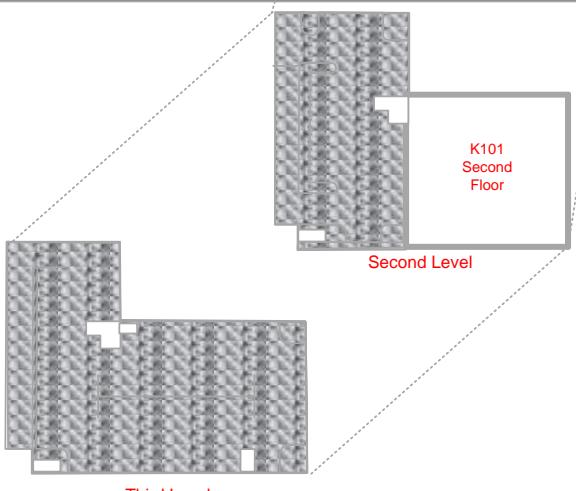
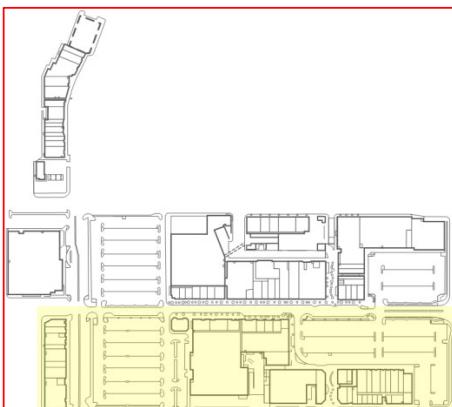


Plans produced by:
ID Plans Corp
05/10/2012
(813) 657-2545



© 2012

The lighting site plan identifies all under-canopy and parking lot lighting. It separates tenant operated from owner operated lighting and details the location, type and voltage of each light. Furthermore, it also identifies meters, photo-cells, contactors, timers and light pole height.

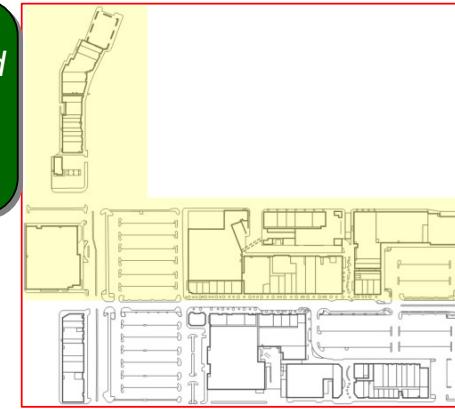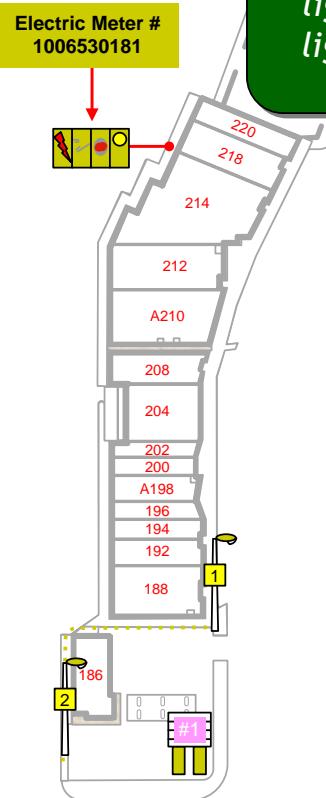


Lighting
Page 1 of 7

	1 Fixture Light Pole
	House Panel
	Lamp Post
	Lighting Contactor
	Photo Cell
	Pole Light Wire Path
	Pylon Sign
	Timer

Gold Lighting Section			
Light Fixture	Symbol	Lighting Type	Line Voltage
Light Pole		400 Watt M.H. Mogul Base	480 Volts
Red Lighting Section			
Light Fixture	Symbol	Lighting Type	Line Voltage
Lamp Post		175 Watt M.H. Medium Base	277 Volts
Light Pole		1000 Watt M.H. Mogul Base	277 Volts

Lighting Contractor: _____
Telephone Number: _____

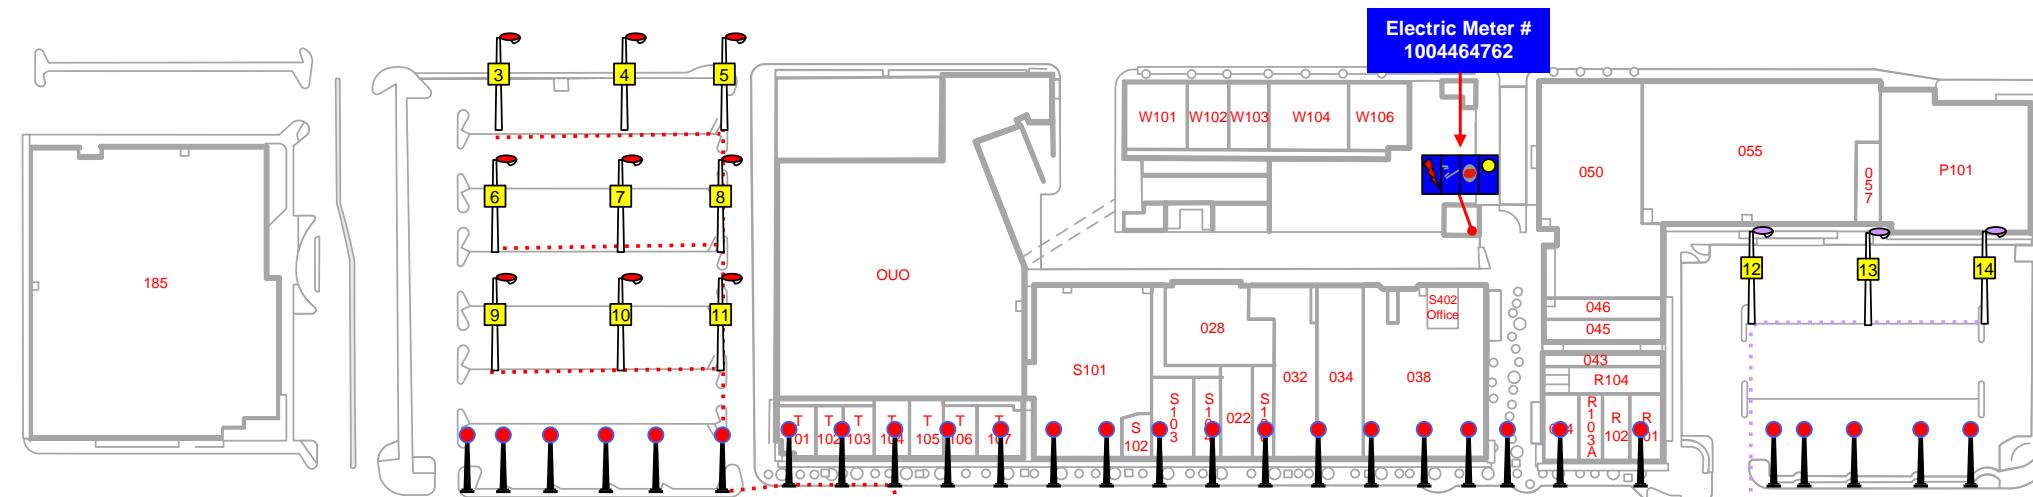



Height of light poles
Measured from ground to fixture:
34'

Plans produced by:
ID Plans Corp
05/10/2012
(813) 657-2545



© 2012



The lighting site plan identifies all under-canopy and parking lot lighting. It separates tenant operated from owner operated lighting and details the location, type and voltage of each light. Furthermore, it also identifies meters, photo-cells, contactors, timers and light pole height.

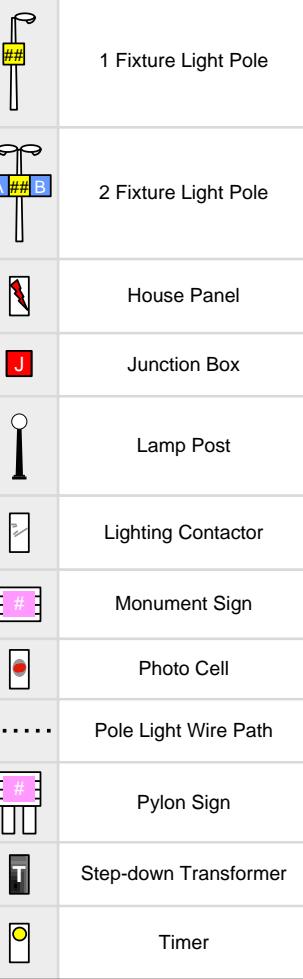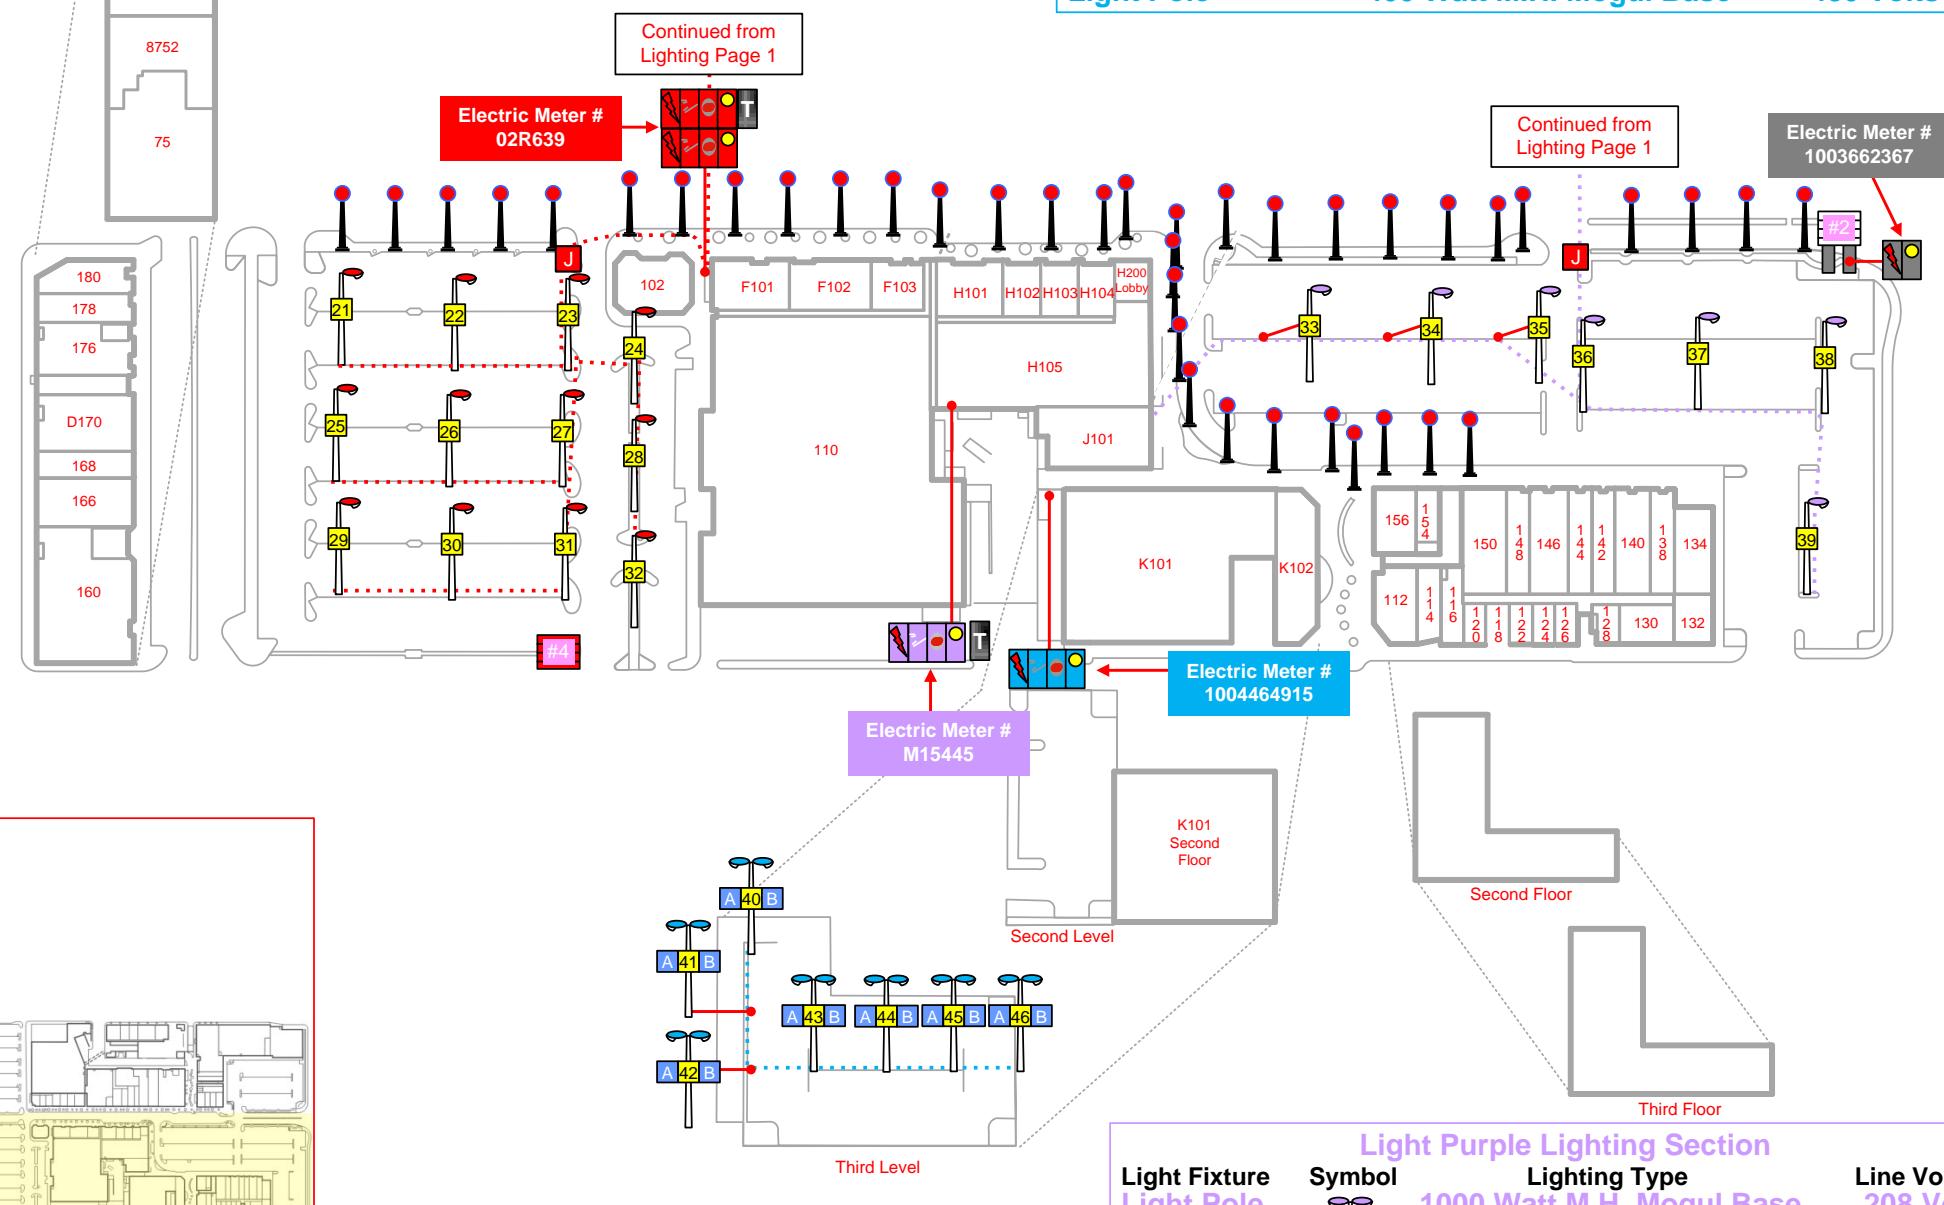


Plans produced by:
ID Plans Corp
05/10/2012
(813) 657-2545

ID Plans Corp.
© 2012


The lighting site plan identifies all under-canopy and parking lot lighting. It separates tenant operated from owner operated lighting and details the location, type and voltage of each light. Furthermore, it also identifies meters, photo-cells, contactors, timers and light pole height.

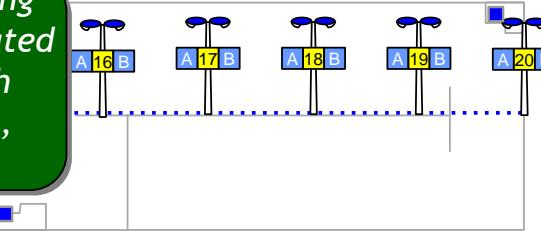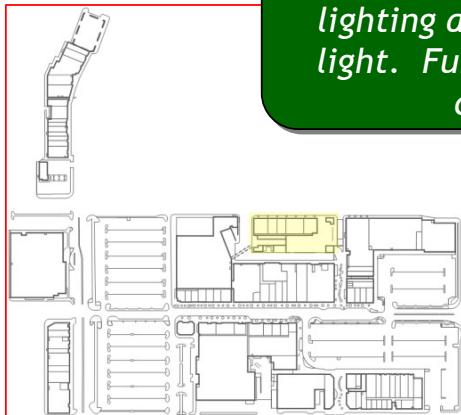


Fifth Level

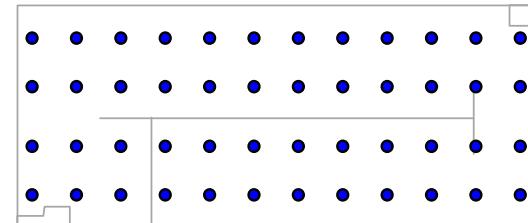


Fourth Level

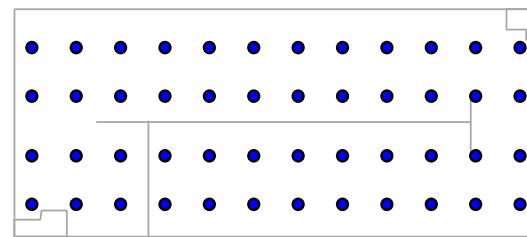

Third Level

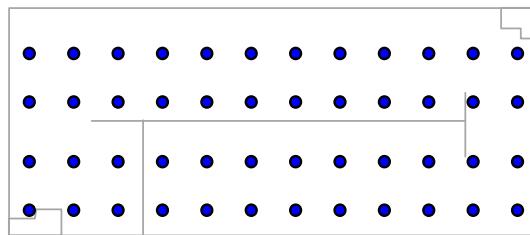

Second Level

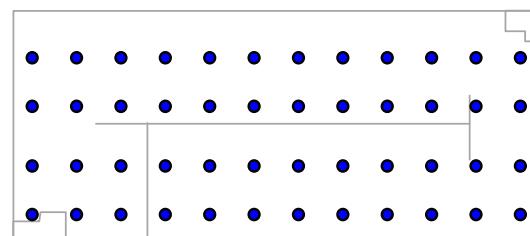

First Level

See Lighting Page 1 for meter location

Electric Meter #
1004464762

Blue Lighting Section		Line Voltage
Light Fixture	Symbol	Lighting Type
Light Pole	●	400 Watt M.H. Mogul Base
Under Canopy	●	100 Watt M.H. Medium Base
Wall Pack	■	32 Watt Fluorescent 2-Pin

Height of light poles

Measured from ground to fixture:

21'

Plans produced by:
ID Plans Corp
05/10/2012
(813) 657-2545



© 2012



The lighting site plan identifies all under-canopy and parking lot lighting. It separates tenant operated from owner operated lighting and details the location, type and voltage of each light. Furthermore, it also identifies meters, photo-cells, contactors, timers and light pole height.

Gold Lighting Section			
Light Fixture	Symbol	Lighting Type	Line Voltage
Under Canopy	●	100 Watt M.H. Medium Base	120 Volts
Under Canopy	○	42 Watt Compact Fluor. Medium Base	120 Volts
Under Canopy	○	75 Watt Incan. Medium Base	120 Volts
Under Canopy	○	23 Watt Compact Fluor. Medium Base	120 Volts
Wall Pack	■	175 Watt M.H. Mogul Base	120 Volts
Wall Pack	■	75 Watt Incan. Medium Base	120 Volts

Purple Lighting Section			
Light Fixture	Symbol	Lighting Type	Line Voltage
Under Canopy	●	100 Watt M.H. Medium Base	120 Volts
Under Canopy	●	75 Watt Incan. Medium Base	120 Volts
Wall Pack	■	70 Watt M.H. Medium Base	120 Volts

Blue Lighting Section			
Light Fixture	Symbol	Lighting Type	Line Voltage
Façade	◆	42 Watt Compact Fluor. 4-Pin Base	277 Volts
Under Canopy	●	100 Watt M.H. Medium Base	277 Volts
Wall Pack	■	175 Watt M.H. Mogul Base	277 Volts
Wall Pack	■	23 Watt Compact Fluor. 2-Pin Base	277 Volts
Wall Pack	■	100 Watt M.H. Medium Base	277 Volts
Wall Pack	■	32 Watt Fluorescent 2-Pin Base	277 Volts

Grey Lighting Section			
Light Fixture	Symbol	Lighting Type	Line Voltage
Façade	◆	70 Watt Halogen 2-Pin Base	120 Volts
Façade	◆	23 Watt Compact Fluor. 4-Pin Base	120 Volts
Under Canopy	●	100 Watt M.H. Medium Base	120 Volts
Under Canopy	●	34 Watt Compact Fluor. Medium Base	120 Volts
Under Canopy	●	32 Watt Compact Fluor. 2-Pin Base	120 Volts
Under Canopy	●	42 Watt Compact Fluor. 4-Pin Base	120 Volts
Under Canopy	●	32 Watt Fluorescent 2-Pin Base	120 Volts
Wall Pack	■	175 Watt M.H. Mogul Base	120 Volts
Wall Pack	■	70 Watt Halogen 2-Pin Base	120 Volts
Wall Pack	■	32 Watt Fluor. 2-Pin Base	120 Volts

Orange Lighting Section			
Light Fixture	Symbol	Lighting Type	Line Voltage
Façade Light	◆	75 Watt Incan. Medium Base	120 Volts
Under Canopy	●	100 Watt M.H. Mogul Base	120 Volts
Wall Pack	■	175 Watt M.H. Mogul Base	120 Volts



Red Lighting Section			
Light Fixture	Symbol	Lighting Type	Line Voltage
Façade	◆	23 Watt Compact Fluor. 4-Pin Base	277 Volts
Under Canopy	●	42 Watt Compact Fluor. 4-Pin Base	120 Volts
Under Canopy	●	70 Watt Halogen 2-Pin Base	120 Volts

Plans produced by:
ID Plans Corp
05/10/2012
(813) 657-2545




© 2012

The lighting site plan identifies all under-canopy and parking lot lighting. It separates tenant operated from owner operated lighting and details the location, type and voltage of each light. Furthermore, it also identifies meters, photo-cells, contactors, timers and light pole height.

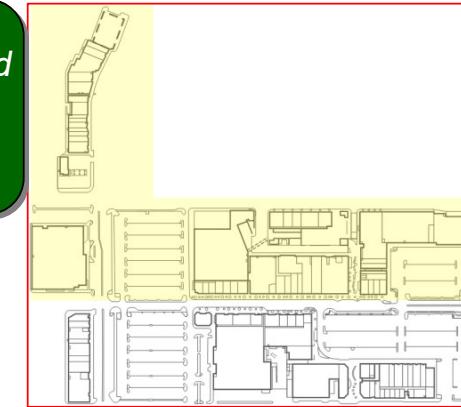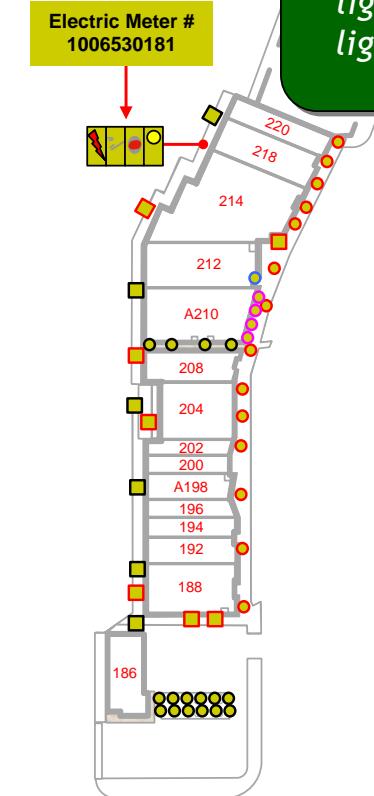

Lighting
Page 5 of 7

	House Panel
	Lighting Contactor
	Photo Cell
	Step-down Transformer
	Timer

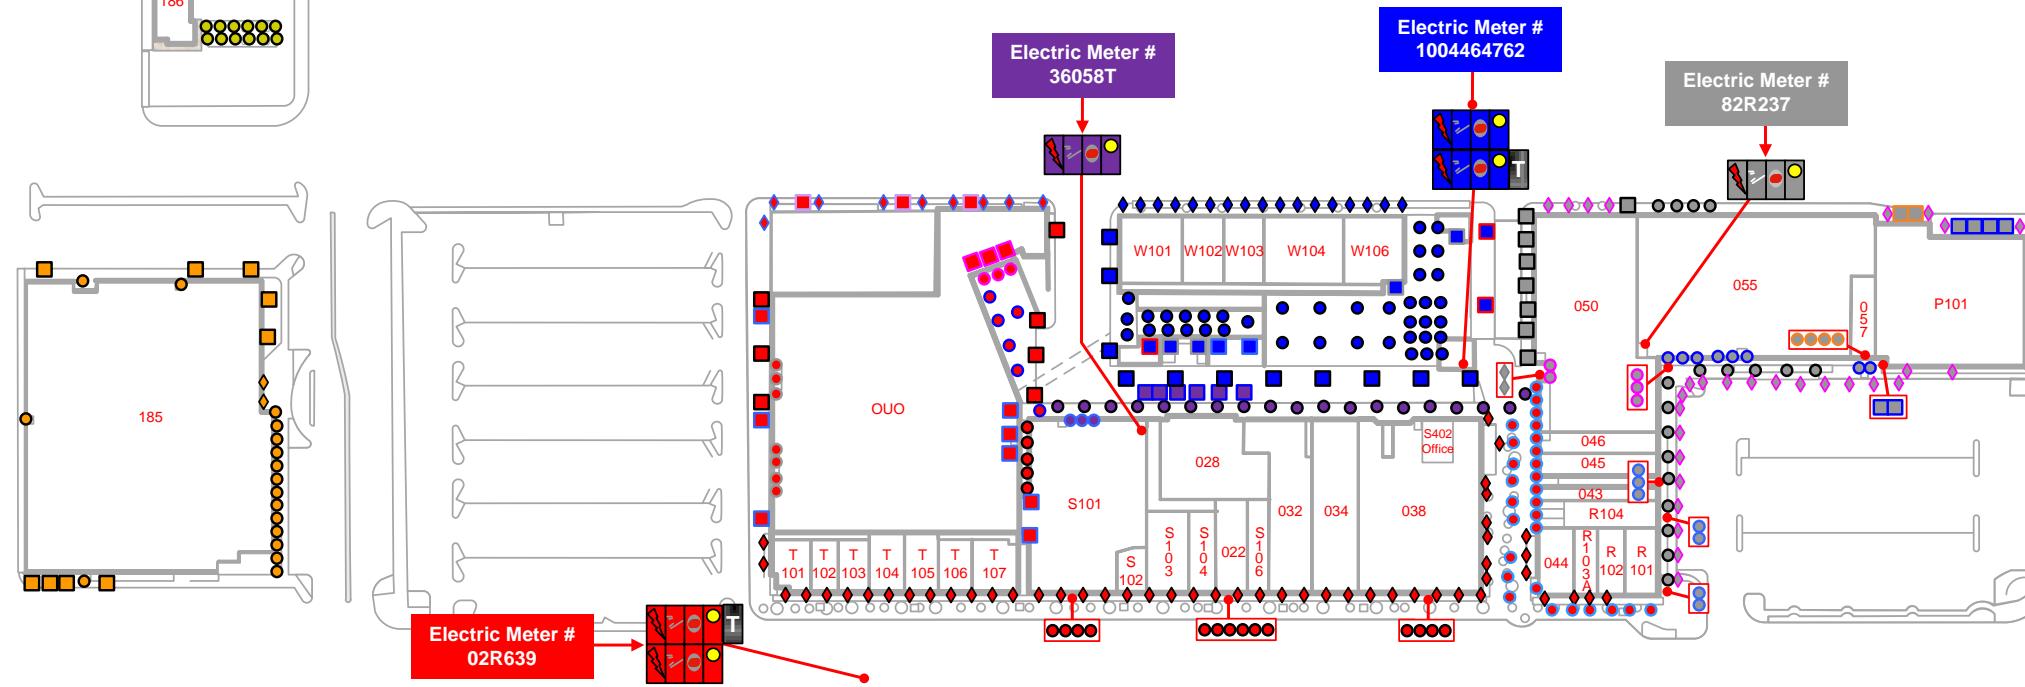

Plans produced by:
ID Plans Corp
05/10/2012
(813) 657-2545



© 2012



The lighting site plan identifies all under-canopy and parking lot lighting. It separates tenant operated from owner operated lighting and details the location, type and voltage of each light. Furthermore, it also identifies meters, photo-cells, contactors, timers and light pole height.

Pink Lighting Section			
Light Fixture	Symbol	Lighting Type	Line Voltage
Under Canopy	●	100 Watt M.H. Medium Base	120 Volts
Under Canopy	●	13 Watt Compact Fluor. 2-Pin Base	120 Volts
Wall Pack	■	175 Watt H.P.S. Mogul Base	120 Volts
Wall Pack	■	23 Watt Compact Fluor. Medium Base	120 Volts
Wall Pack	■	70 Watt M.H. Medium Base	120 Volts

Orange Lighting Section			
Light Fixture	Symbol	Lighting Type	Line Voltage
Façade	◊	70 Watt Halogen 2-Pin Base	120 Volts
Reflector Flood	□	250 Watt M.H. Mogul Base	277 Volts
Under Canopy	○	100 Watt M.H. Medium Base	120 Volts
Under Canopy	○	75 Watt Incan. Medium Base	120 Volts
Under Canopy	●	23 Watt Compact Fluor. Medium Base	120 Volts
Under Canopy	●	50 Watt Halogen Medium Base	120 Volts
Walkway	▲	28 Watt Compact Fluor. Medium Base	120 Volts

Light Purple Lighting Section			
Light Fixture	Symbol	Lighting Type	Line Voltage
Façade	◊	42 Watt Compact Fluor. 4-Pin Base	120 Volts
Under Canopy	●	23 Watt Compact Fluor. 4-Pin Base	277 Volts

Red Lighting Section			
Light Fixture	Symbol	Lighting Type	Line Voltage
Façade	◊	23 Watt Compact Fluor. 4-Pin Base	277 Volts
Façade	◊	26 Watt Compact Fluor. 4-Pin Base	277 Volts
Under Canopy	●	70 Watt M.H. Medium Base	277 Volts
Wall Pack	■	175 Watt H.P.S. Mogul Base	277 Volts

Light Blue Lighting Section			
Light Fixture	Symbol	Lighting Type	Line Voltage
Façade	◊	42 Watt Compact Fluor. 4-Pin Base	277 Volts
Façade	◊	50 Watt Halogen 2-Pin Base	12 Volts
Façade	◊	26 Watt Compact Fluor. 4-Pin Base	277 Volts
Under Canopy	○	70 Watt Halogen 2-Pin Base	277 Volts
Under Canopy	○	100 Watt M.H. Medium Base	277 Volts
Under Canopy	●	100 Watt Halogen 2-Pin Base	277 Volts
Under Canopy	●	38 Watt Fluor. 2-Pin Base	277 Volts

Plans produced by:
ID Plans Corp
05/10/2012
(813) 657-2545




© 2012

The lighting site plan identifies all under-canopy and parking lot lighting. It separates tenant operated from owner operated lighting and details the location, type and voltage of each light. Furthermore, it also identifies meters, photo-cells, contactors, timers and light pole height.

Lighting

Page 7 of 7

	House Panel
	Lighting Contactor
	Photo Cell
	Step-down Transformer
	Timer



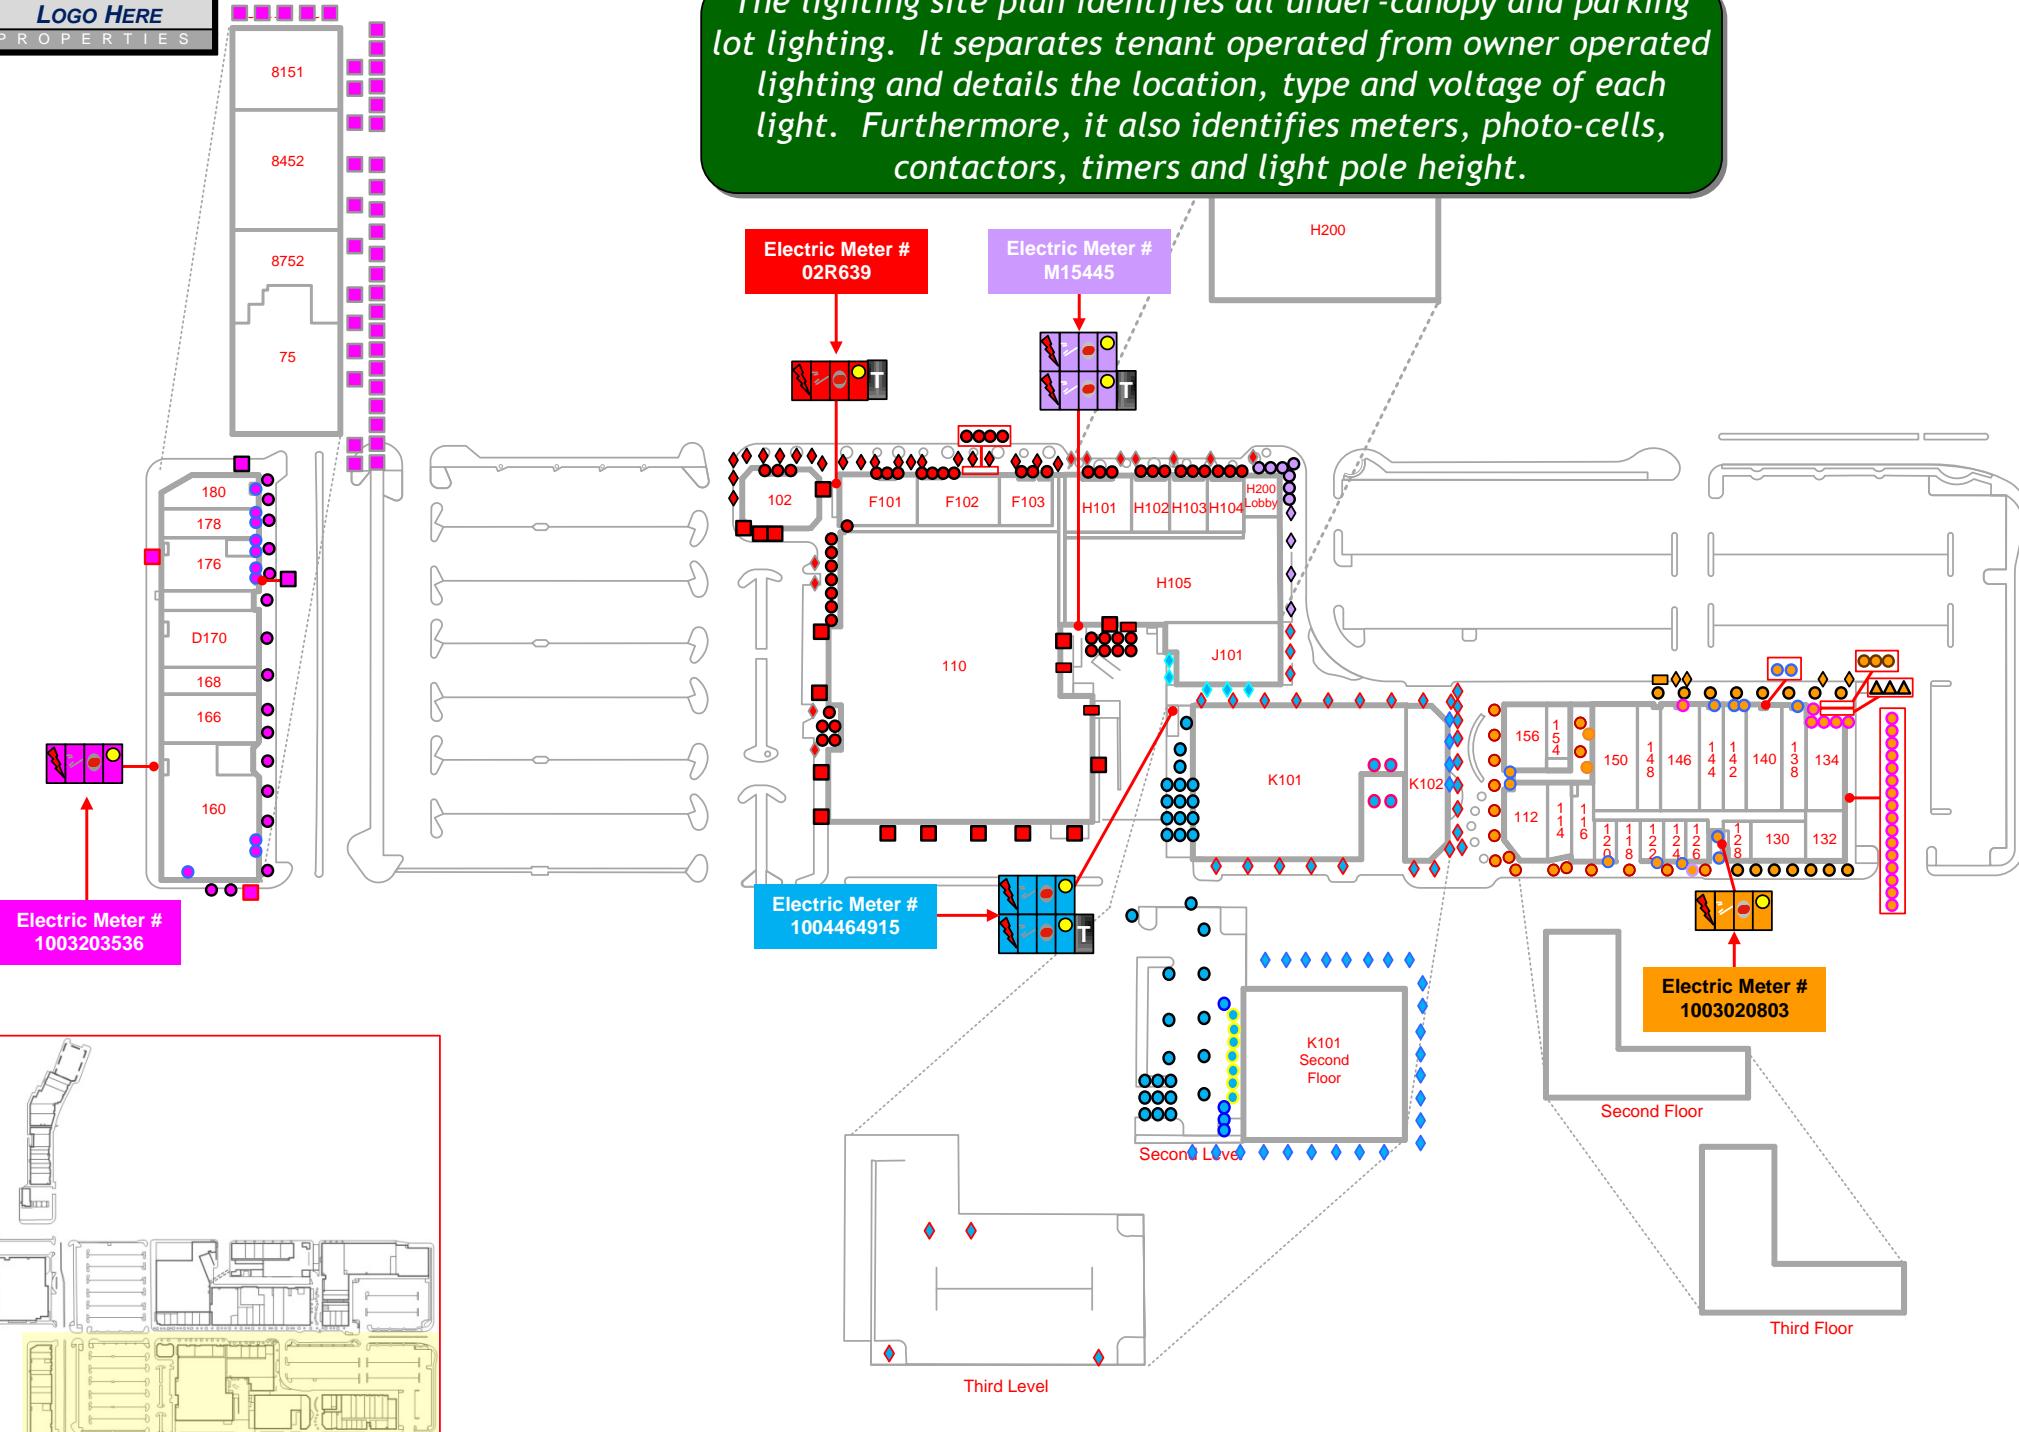


Plans produced by:
ID Plans Corp
05/10/2012
(813) 657-2545



© 2012

The location page provides a map and satellite view of the property, as well as the physical address.

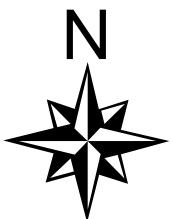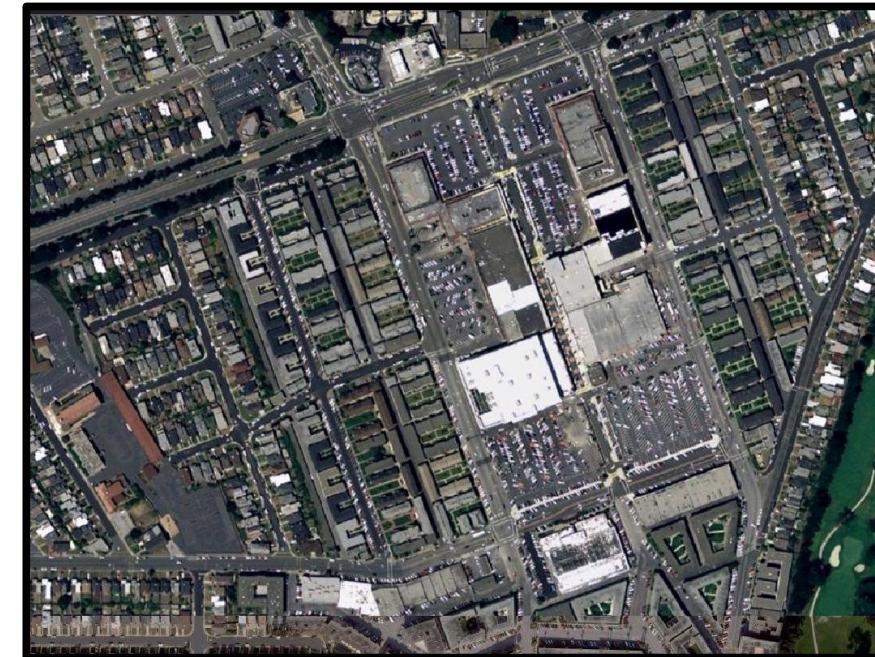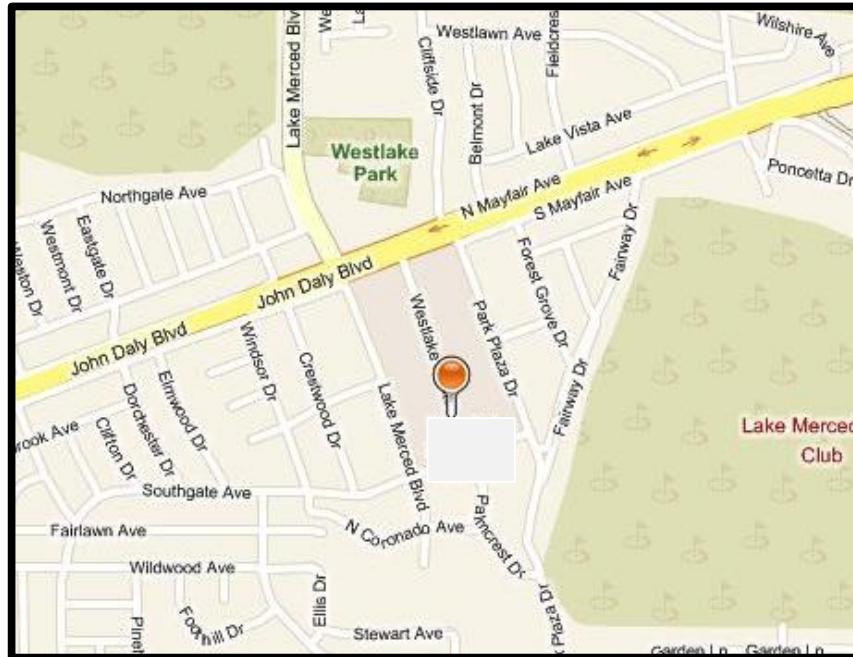

Location Address:
100 Park Plaza Drive
Daly City, CA 94015



Plans produced by:
ID Plans Corp
05/10/2012
(813) 657-2545




© 2012



The parking site plan details the total number of spaces and identifies all disabled spaces and ramps. It also locates speed bumps and other parking related information.

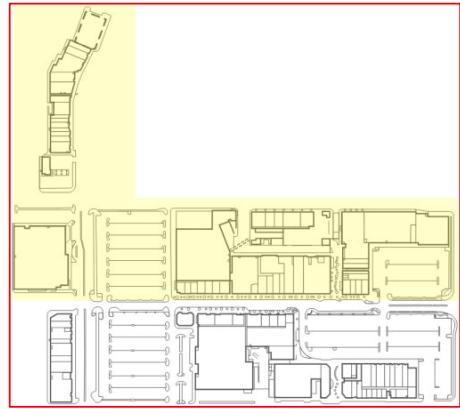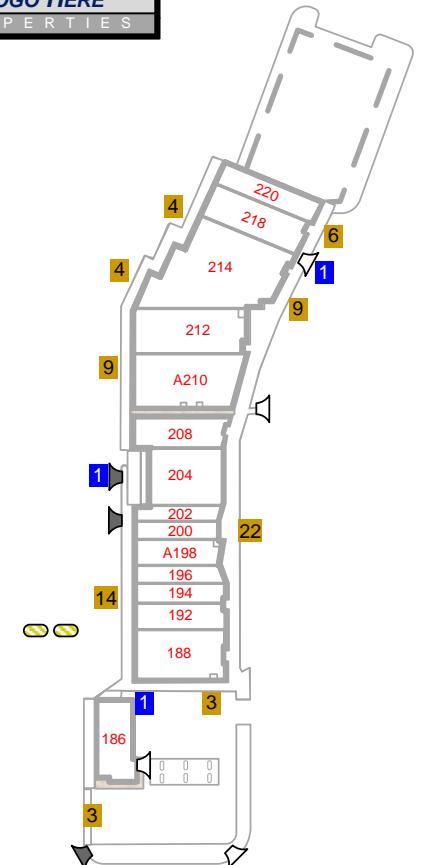

Parking	
Page 1 of 3	
#	Number of Handicapped Parking Spaces
#	Number of Regular Parking Spaces
►	Ramp
■	Shopping Cart Enclosure
○	Speed Bump
30	Total Number of Handicapped Parking Spaces
686	Total Number of Regular Parking Spaces
716	Total Number of Parking Spaces


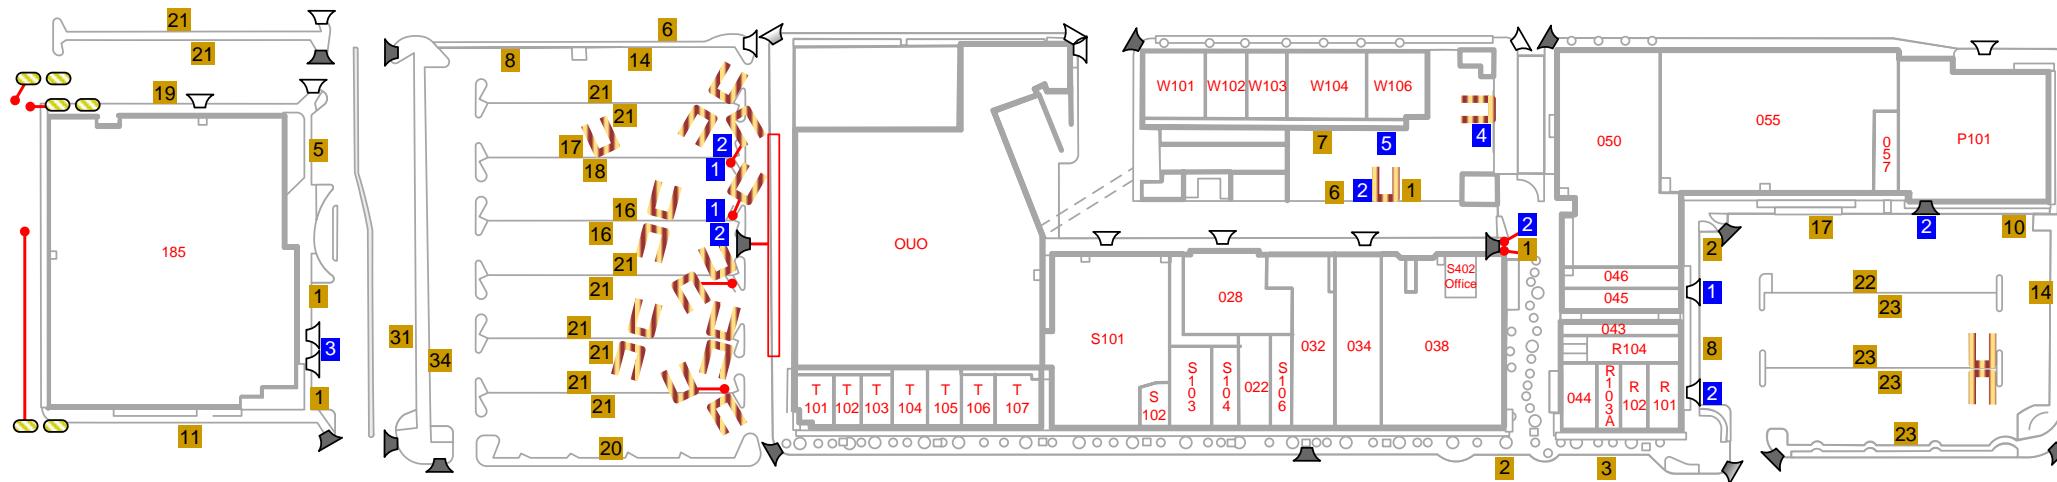


Plans produced by:
ID Plans Corp
05/10/2012
(813) 657-2545




© 2012


The parking site plan details the total number of spaces and identifies all disabled spaces and ramps. It also locates speed bumps and other parking related information.

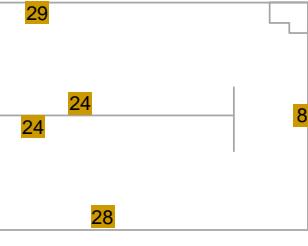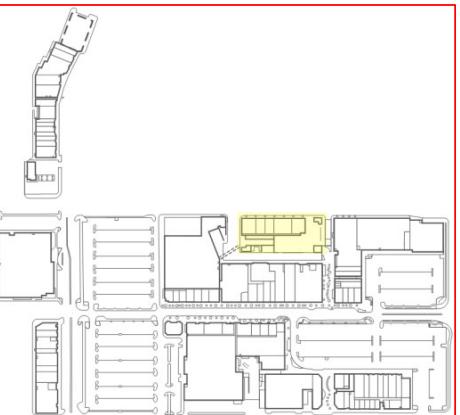


Fifth Level

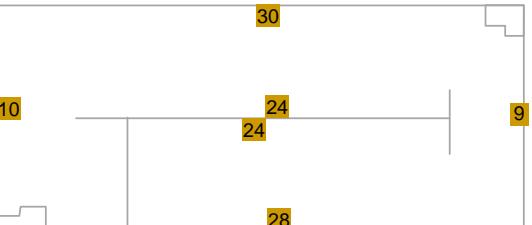


Fourth Level

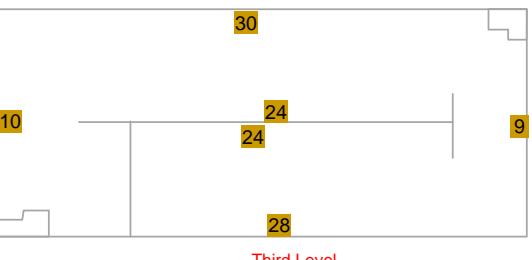

Third Level

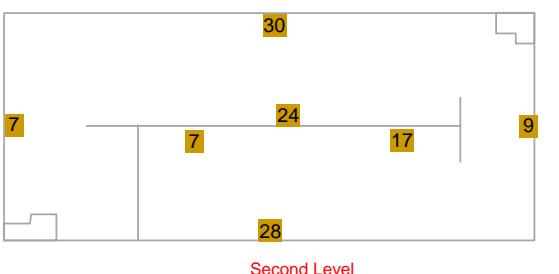

Second Level

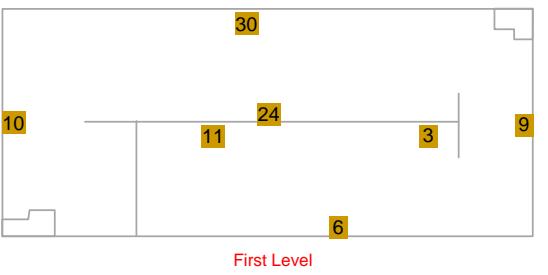

First Level

Parking


Page 2 of 3


#	Number of Regular Parking Spaces
585	Total Number of Regular Parking Spaces
585	Total Number of Parking Spaces

Plans produced by:
ID Plans Corp
05/10/2012
(813) 657-2545





© 2012

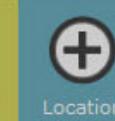

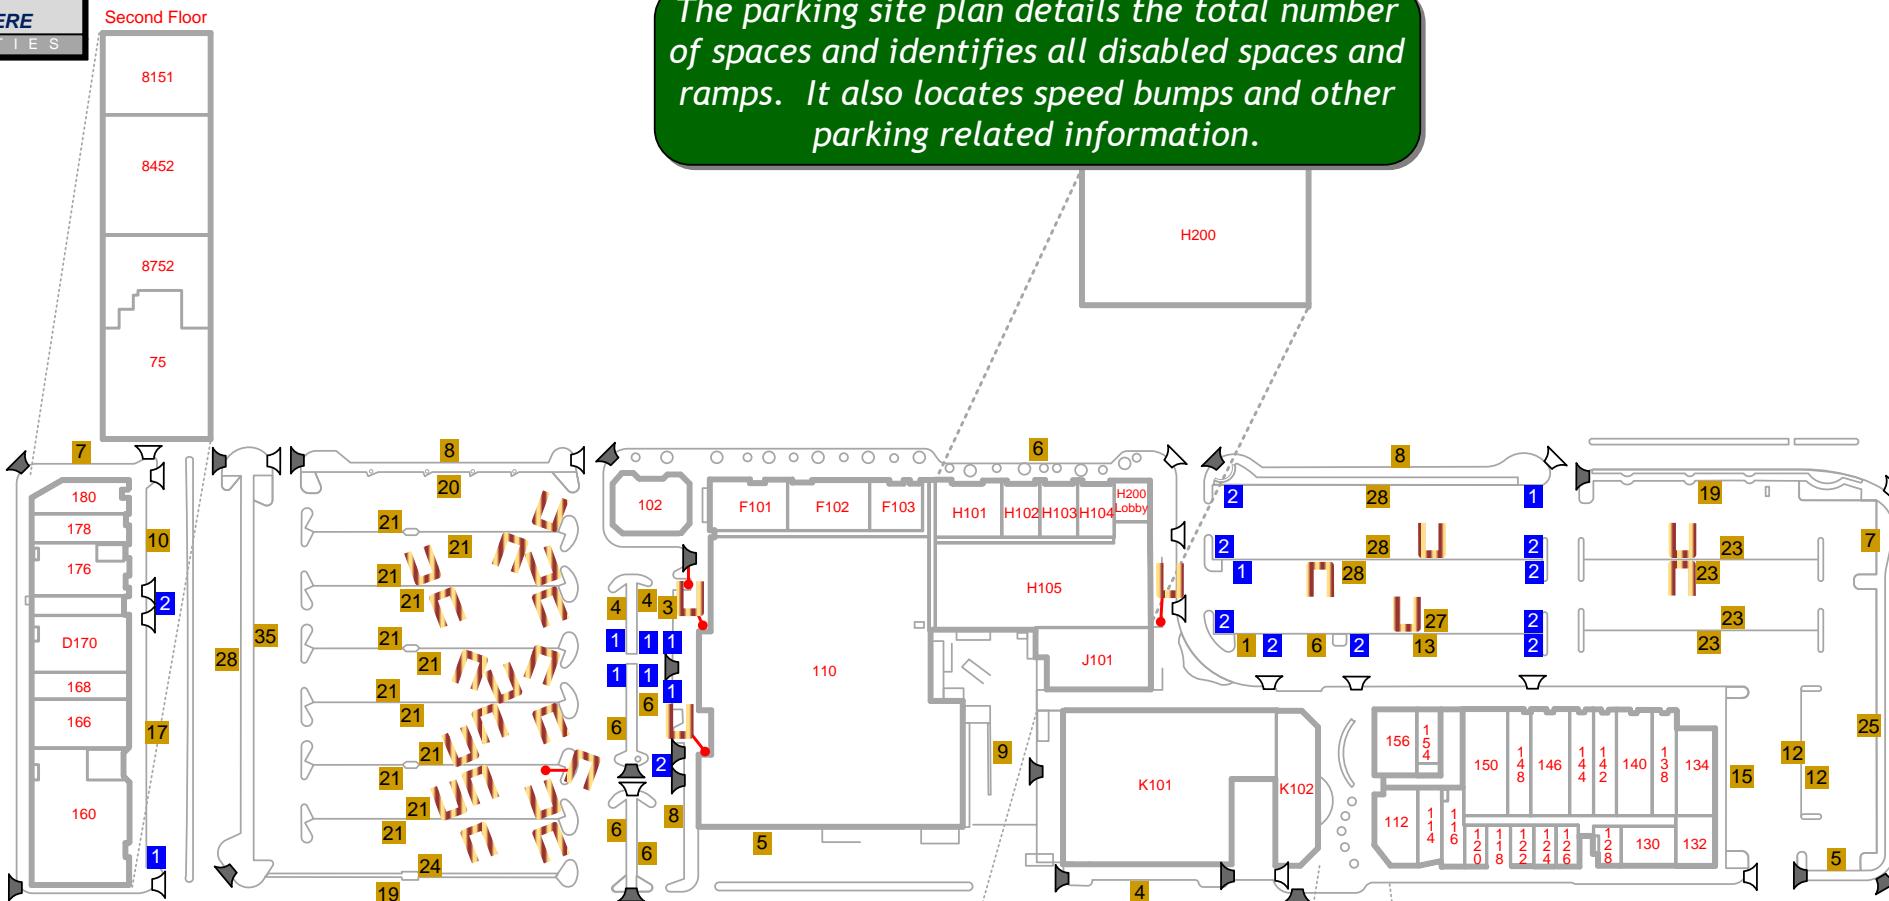

Parking	
Page 3 of 3	
#	Number of Handicapped Parking Spaces
#	Number of Regular Parking Spaces
Ramp	
Shopping Cart Enclosure	
Total Number of Handicapped Parking Spaces	
Total Number of Regular Parking Spaces	
Total Number of Parking Spaces	

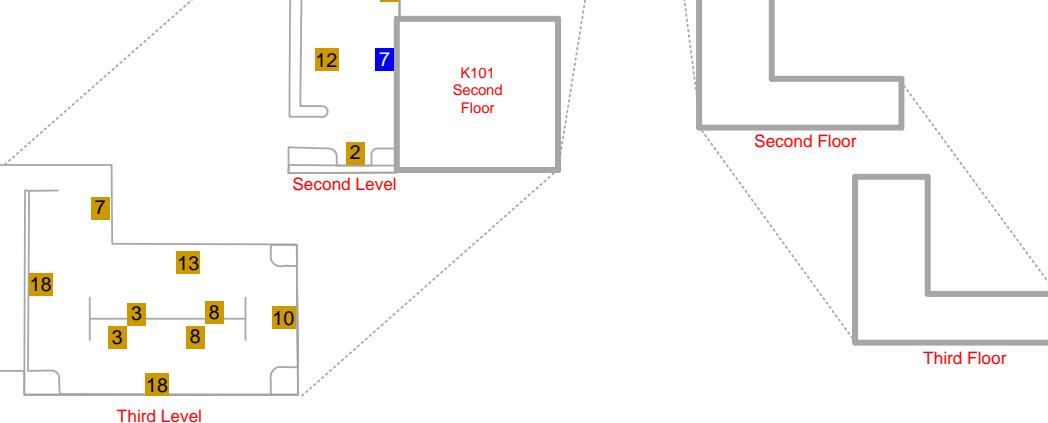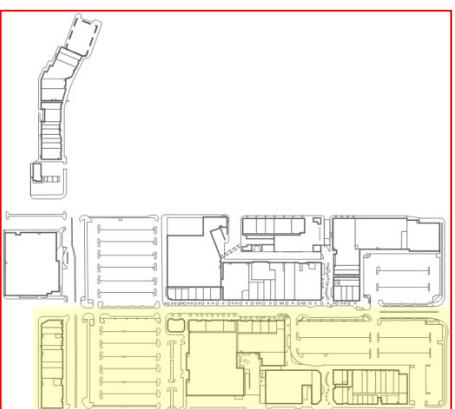


Plans produced by:
ID Plans Corp
05/10/2012
(813) 657-2545



© 2012

The pavement site plan identifies all pavement markings including handicap spaces, direction arrows, stop lines, crosswalks and fire lanes.

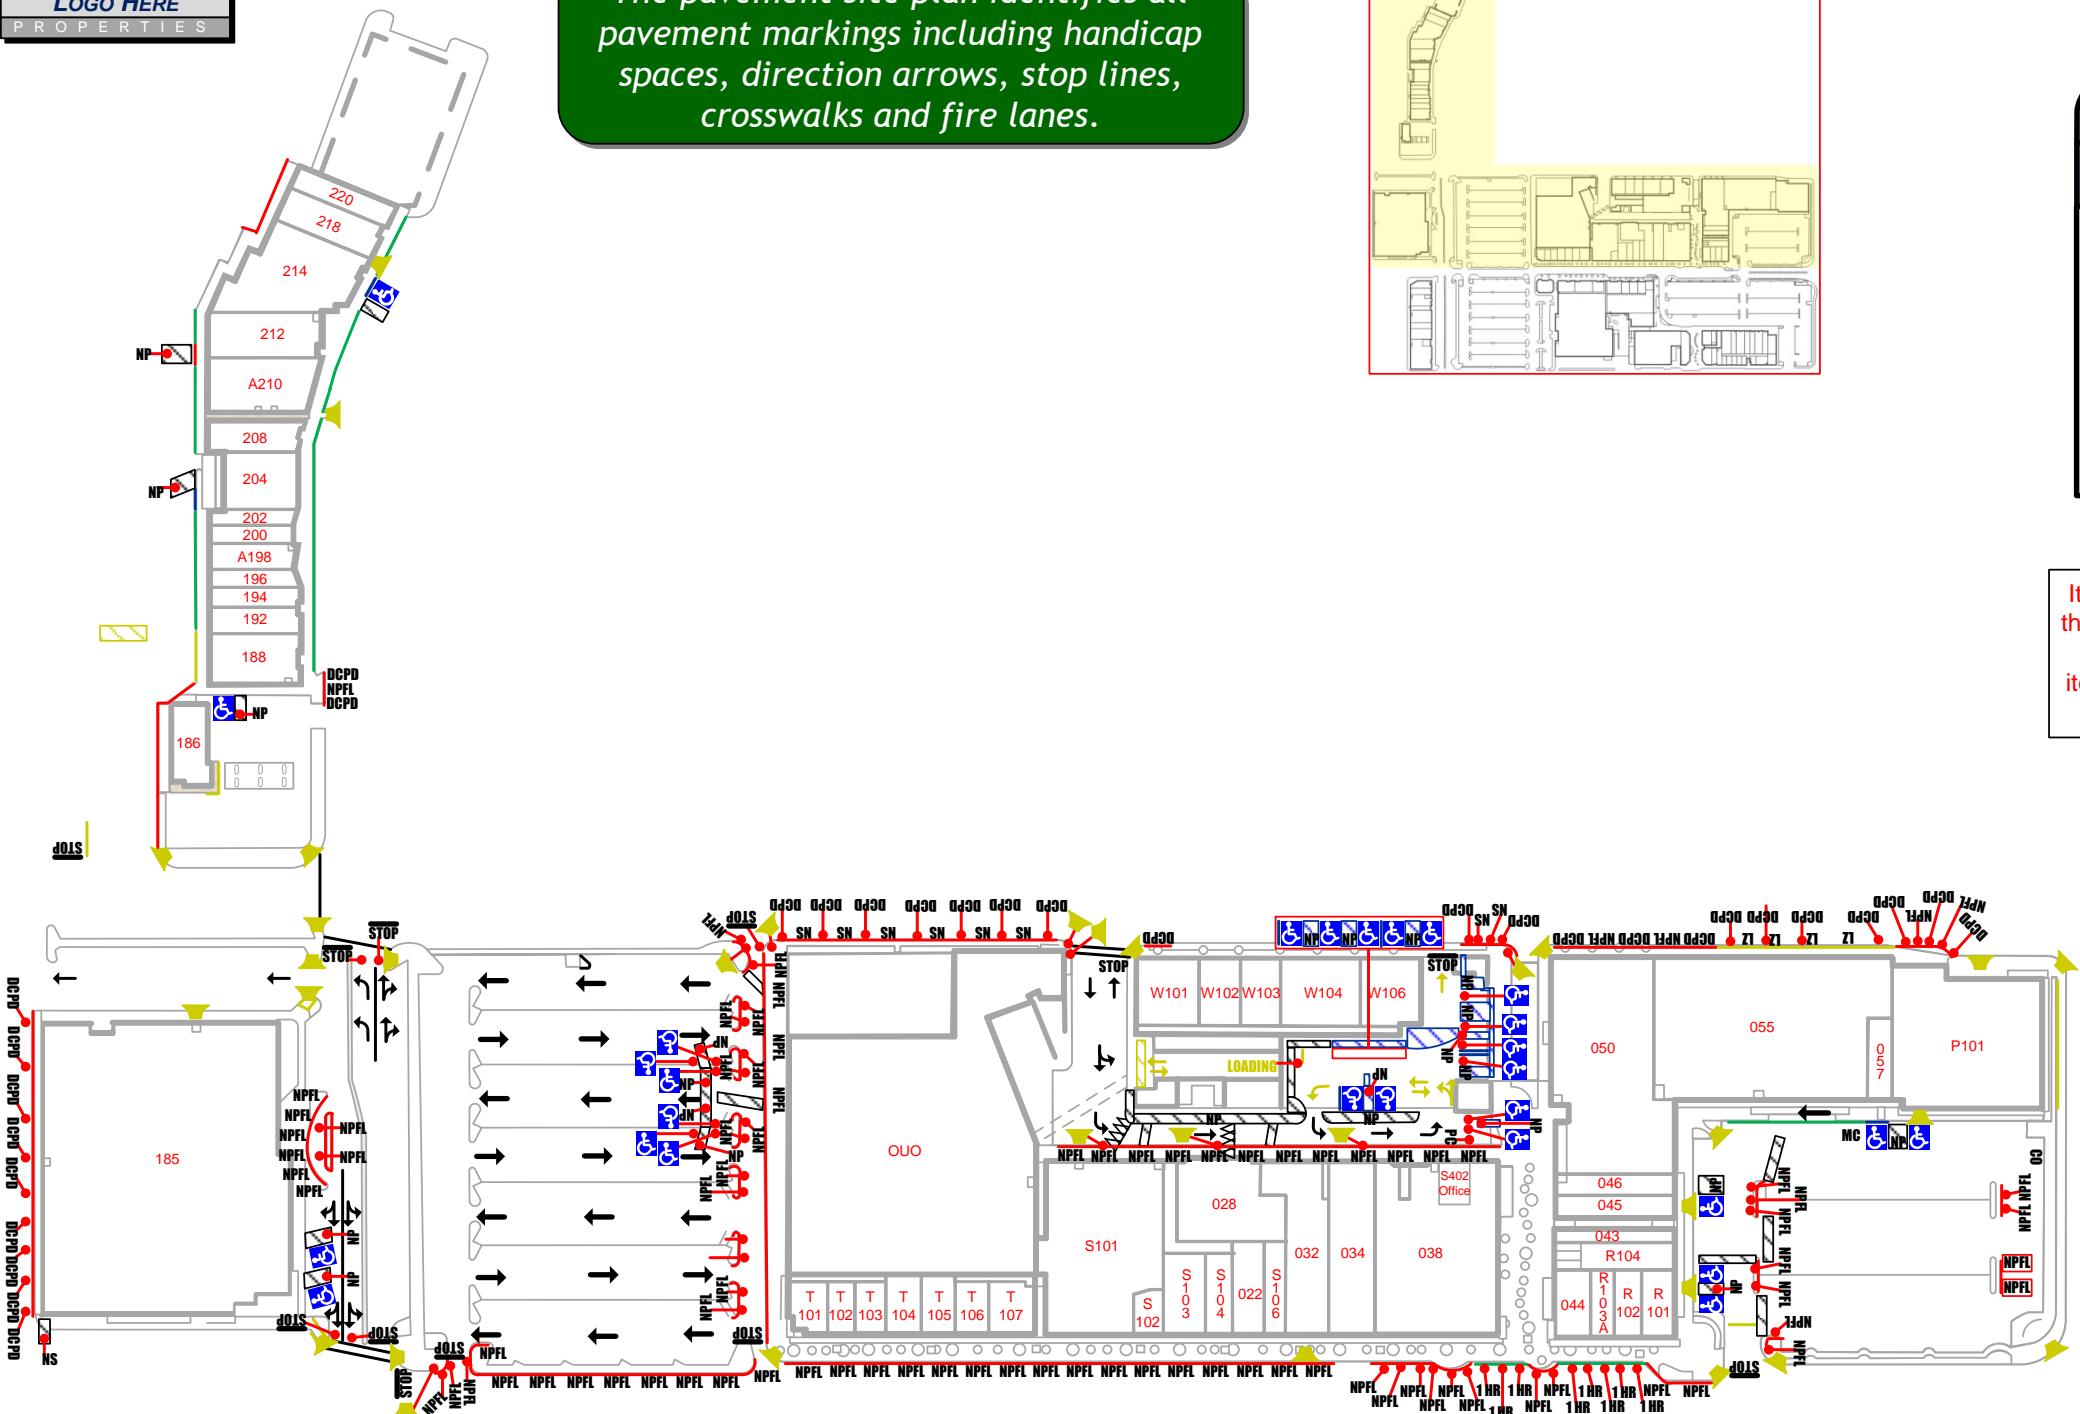

Pavement Markings

Page 1 of 3

CO	Compact Only
MC	Motorcycle
NP	No Parking
NS	No Stopping
PC	Reserved For Patrol Vehicle


Plans produced by:
ID Plans Corp
05/10/2012
(813) 657-2545



© 2012



The pavement site plan identifies all pavement markings including handicap spaces, direction arrows, stop lines, crosswalks and fire lanes.

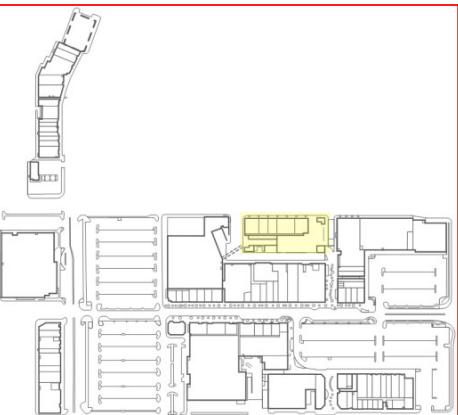

Fifth Level




Fourth Level



Third Level



Second Level

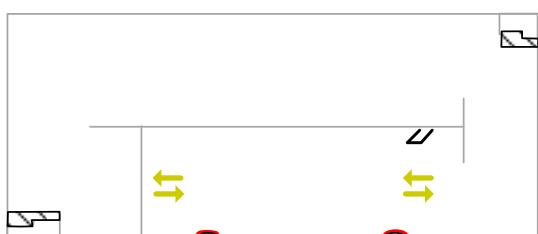



First Level


Items on this page are marked as they are painted on the pavement / curb on site. Please note: any items marked in black are actually painted white on the pavement.

Plans produced by:
ID Plans Corp
05/10/2012
(813) 657-2545



© 2012

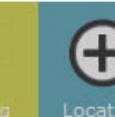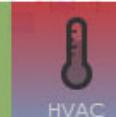

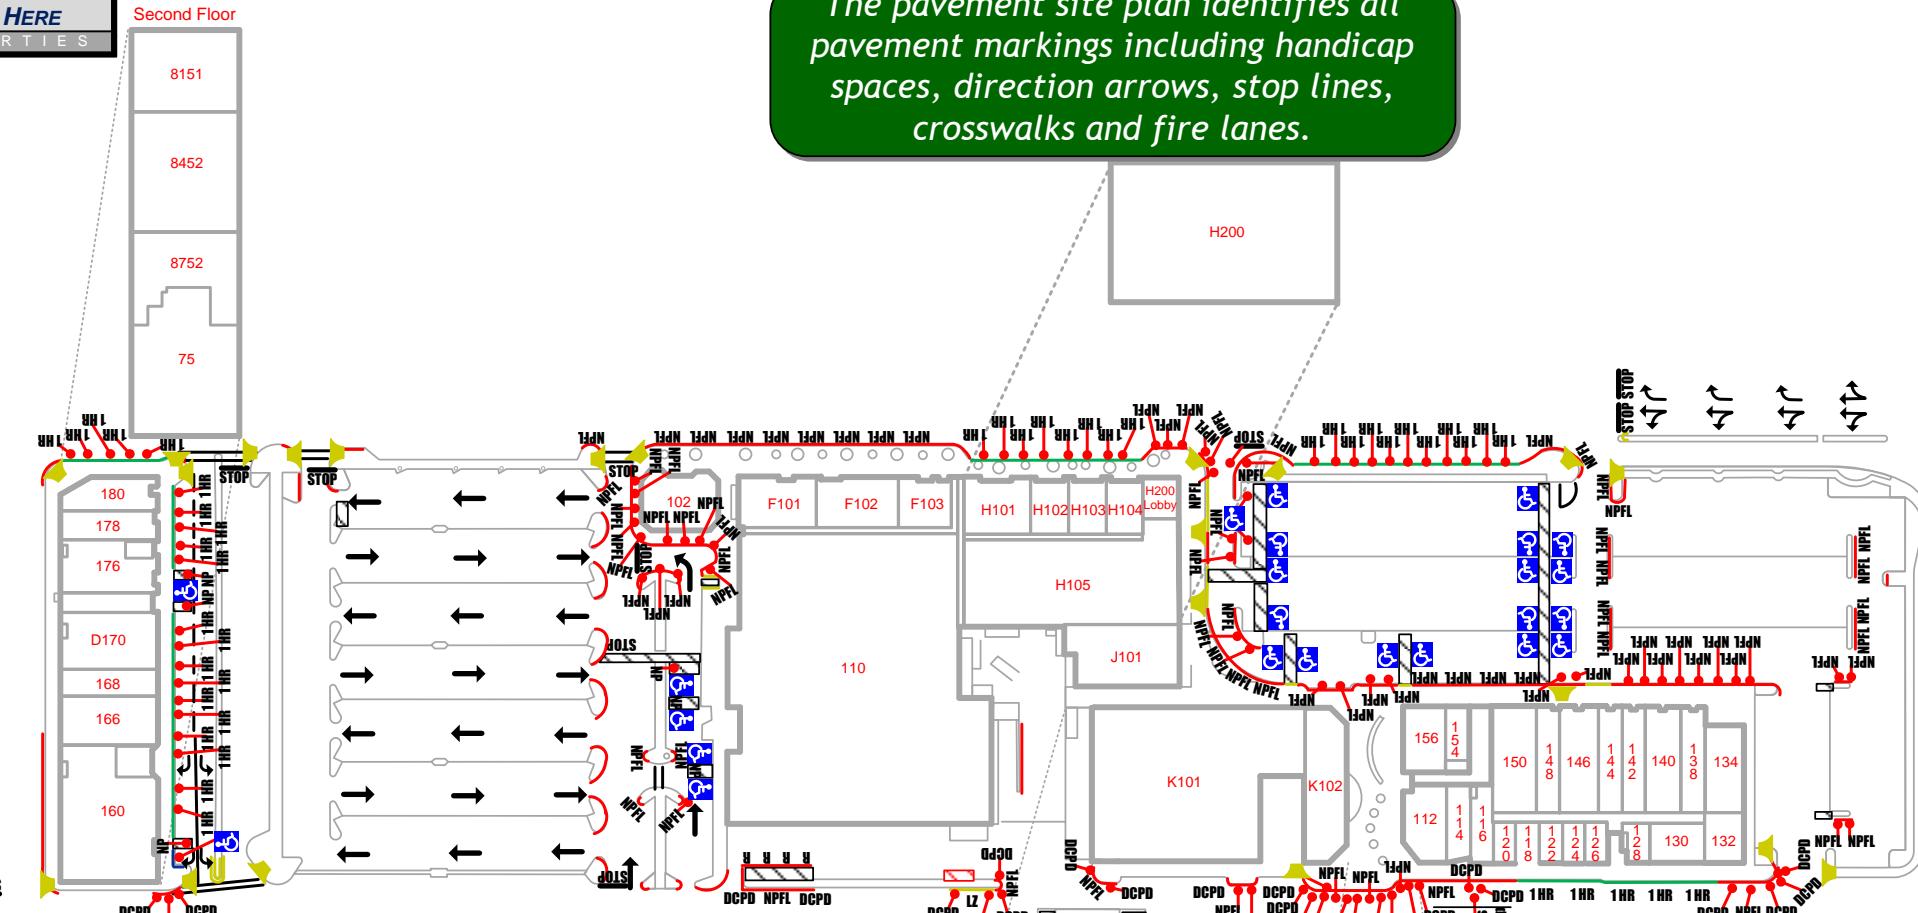



The pavement site plan identifies all pavement markings including handicap spaces, direction arrows, stop lines, crosswalks and fire lanes.

Pavement Markings

Page 3 of 3

LZ	Loading Zone
NPFL	No Parking Fire Lane
R	Reserved
SCO	Small Car Only

Items on this page are marked as they are painted on the pavement / curb on site. Please note: any items marked in black are actually painted white on the pavement.

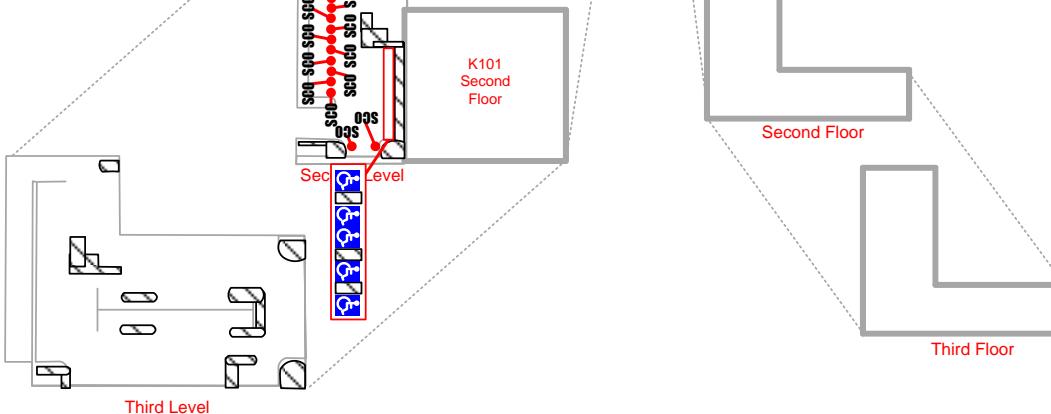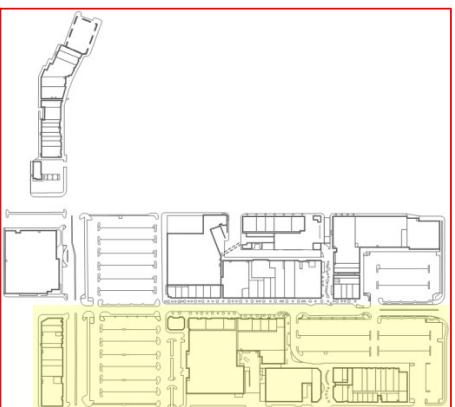

Plans produced by:
ID Plans Corp
05/10/2012
(813) 657-2545



© 2012

The pylon sign measurements site plan provides photos and overall measurements for pylon signs and monuments signs, as well as the panel sign measurements.


Pylon Sign Measurements
Page 1 of 4



Pylon Sign #1



Monument Sign #1

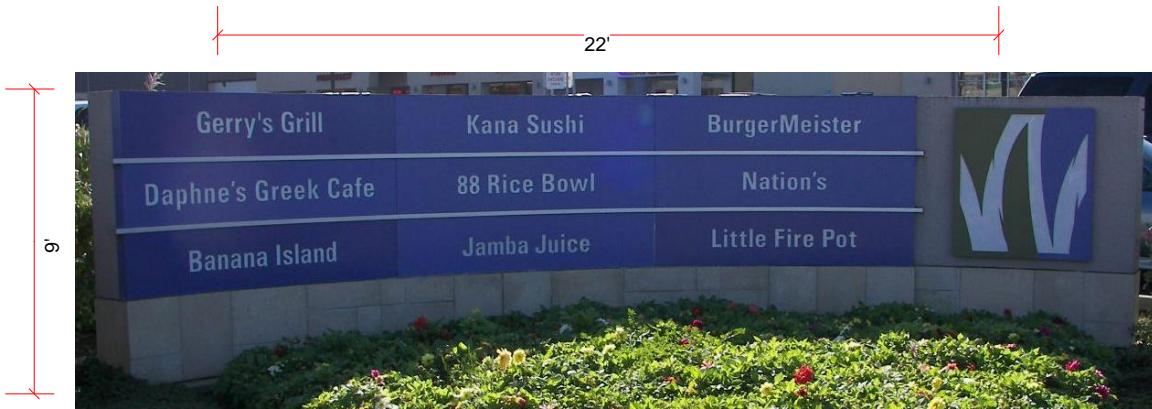


Monument Sign #2

*Sign panels are approximate sizes


Plans produced by:
ID Plans Corp
05/10/2012
(813) 657-2545



© 2012

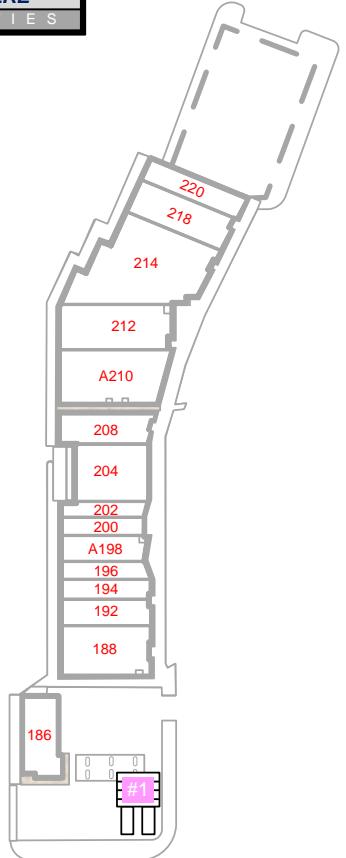


The pylon sign measurements site plan provides photos and overall measurements for pylon signs and monuments signs, as well as the panel sign measurements.

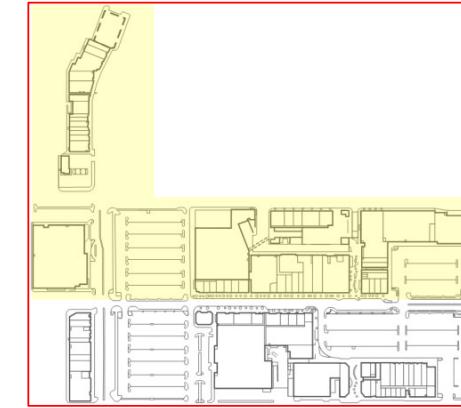

Pylon Sign Measurements

Page 2 of 4

#	Monument Sign
#	Pylon Sign

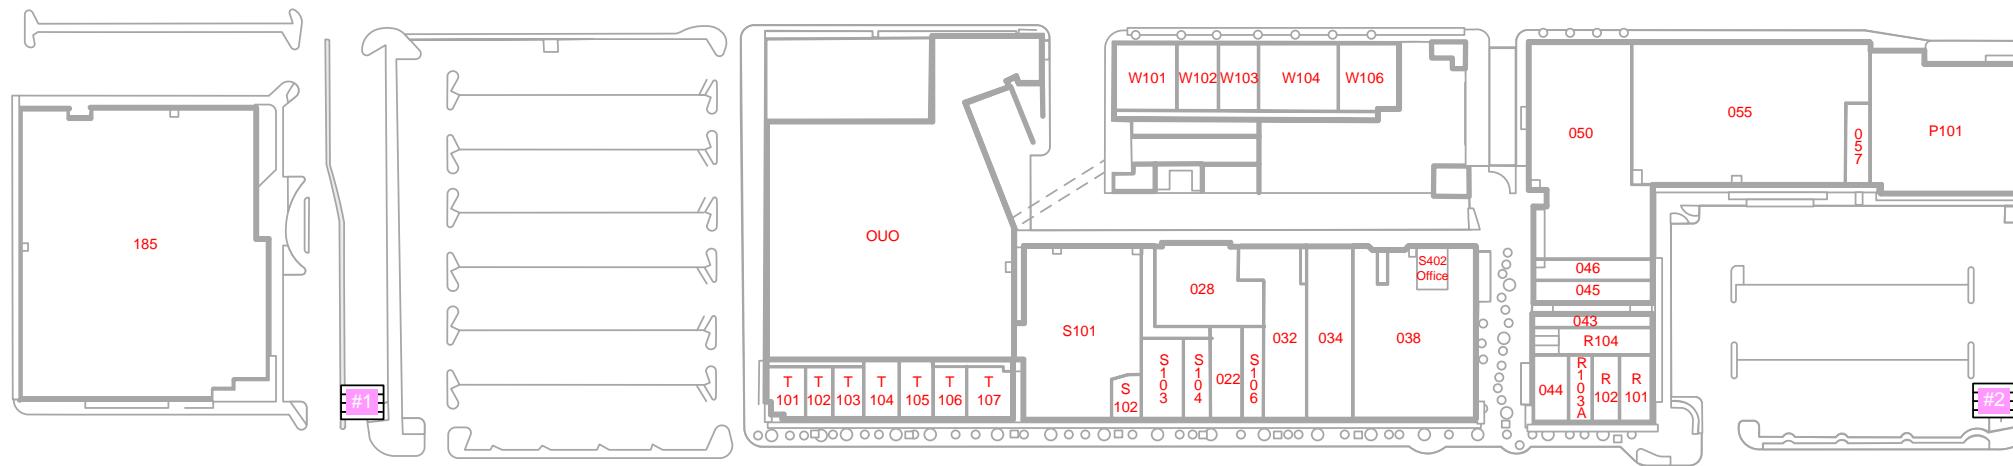

Plans produced by:
ID Plans Corp
05/10/2012
(813) 657-2545



© 2012



*Sign panels are approximate sizes

Pylon Sign #2


The pylon sign measurements site plan provides photos and overall measurements for pylon signs and monuments signs, as well as the panel sign measurements.

ID Plans Mall

Pylon Sign Measurements
Page 3 of 4



Monument Sign #3

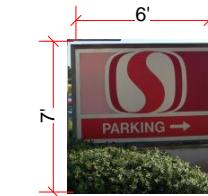

Monument Sign #4

Plans produced by:
ID Plans Corp
05/10/2012
(813) 657-2545





© 2012



The pylon sign measurements site plan provides photos and overall measurements for pylon signs and monuments signs, as well as the panel sign measurements.

Pylon Sign Measurements	
Page 4 of 4	
#	Monument Sign
#	Pylon Sign

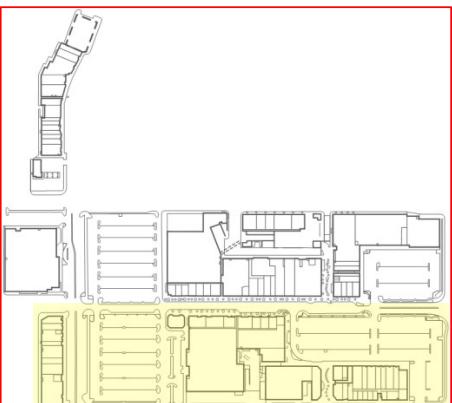
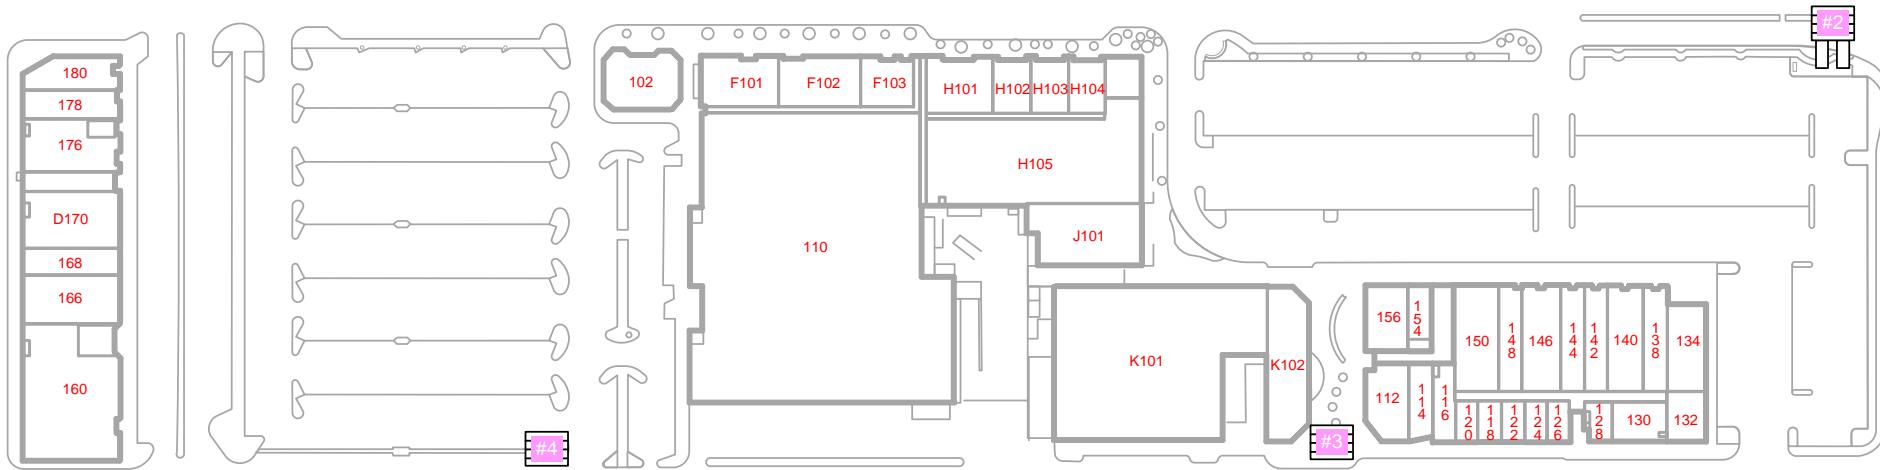


Plans produced by:
ID Plans Corp
05/10/2012
(813) 657-2545



© 2012

The rooftop site plan identifies various items on the roof to keep track of any roofing issues - to be provided by the customer.

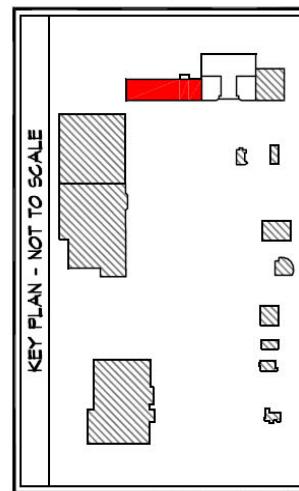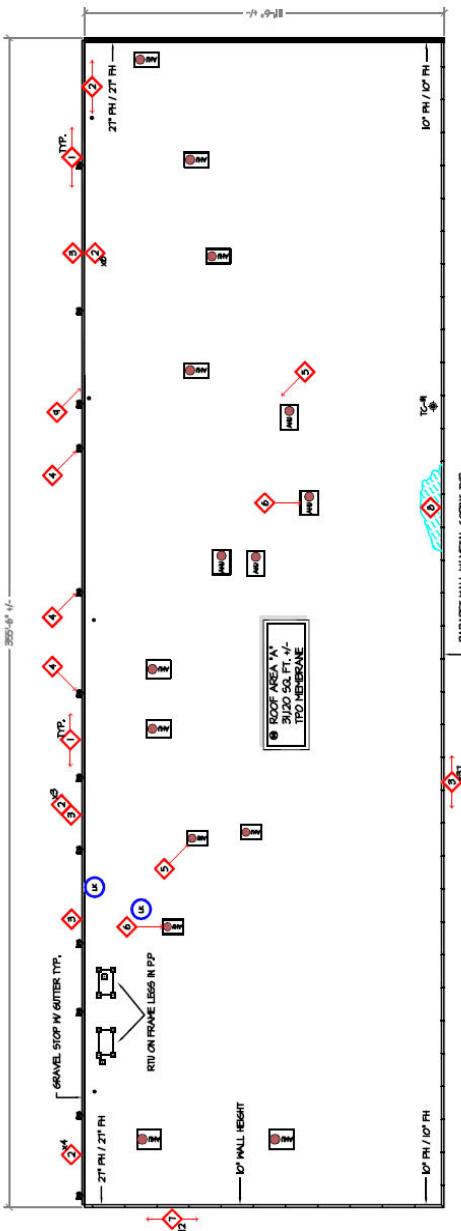


Information can be added, but
needs to be provided by customer.

Plans produced by:
ID Plans Corp
05/10/2012
(813) 657-2545




© 2012

The rooftop site plan identifies various items on the roof to keep track of any roofing issues - to be provided by the customer.

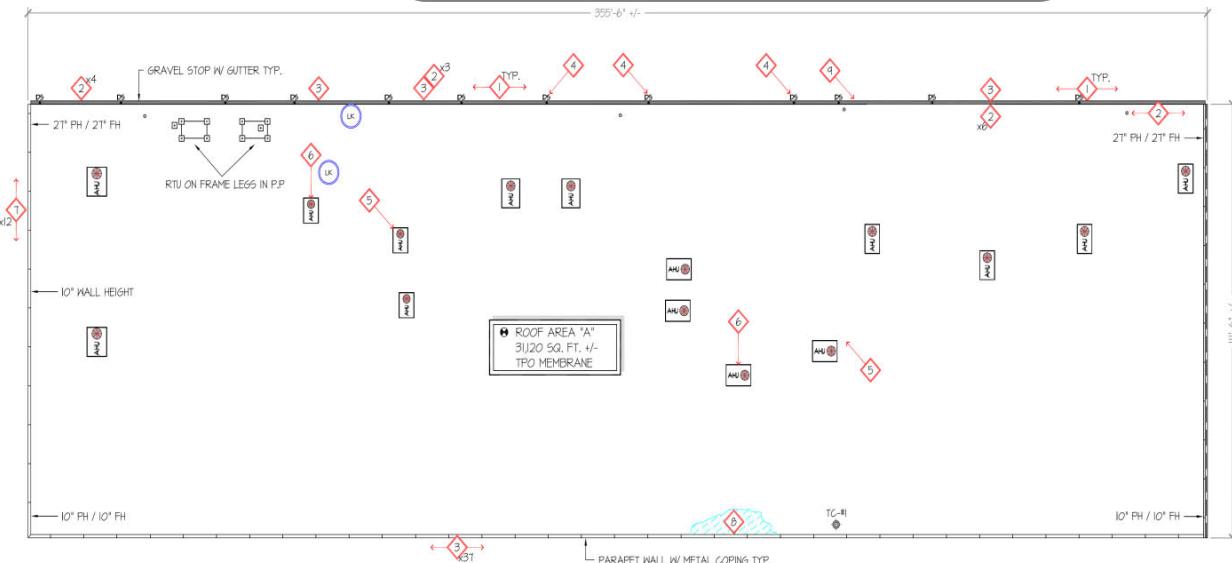

Information can be added, but needs to be provided by customer.


ROOF AREA "A" - 31'10" SQ. FT. +/-
TOTAL PROJECT ROOF AREA - 59,289 SQ. FT. +/-
1/16"=1'-0"
4

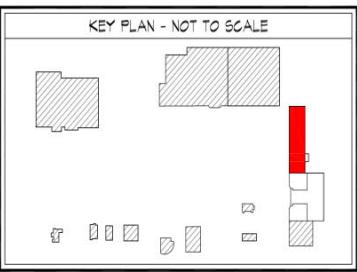

TPO DEFICIENCY LIST	
1	SEALANT DETERIORATION AT GUTTER LAPS AND OUTLETS
2	LOOSE / BROKEN STIFFENER STRAPS IN GUTTER
3	WATER / DEBRIS IN GUTTER
4	DAMAGED DOWNSPOUT
5	CUT / PUNCTURE OR DAMAGED MEMBRANE
6	MECHANICAL DAMAGE / RUST AT HVAC UNITS
7	SEALANT DETERIORATION AT COPING COVER PLATES
8	MINOR PONDING
9	SEALANT SPLITS AT CONTROL JOINT IN PRECAST

SYMBOL LEGEND	
□	PITCH POCKET
DS	DOWNSPOUT
□	STANDARD CURB
G	GAS CONDUIT
●	ROOF DRAIN
□	SQUARE VENT
○	EXHAUST UNIT
T	TEST CUT
AHU	AIR HANDLING UNIT
AHUS	AIR HANDLING UNIT ON SLEEPERS
○	LEAK LOCATION
□	DEFICIENCY LOCATION

NOTE: PENETRATIONS ARE APPROXIMATE IN SIZE AND LOCATION TO BE USED AS REFERENCE POINTS ONLY

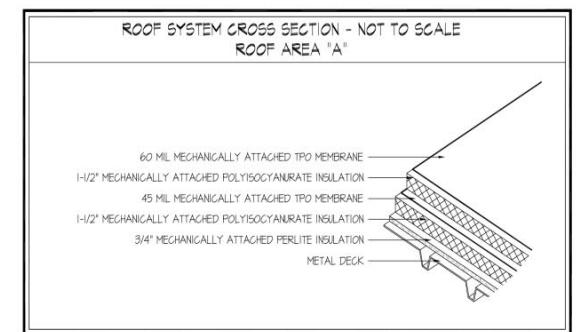

Plans produced by:
ID Plans Corp
05/10/2012
(813) 657-2545



© 2012



1 HR	1 Hour Parking to 8:00 a.m.- 6:00 p.m. Except Sundays & Holidays	PAT	Place All Trash in Bins Do Not Leave Materials on Ground
10	10 MPH	RSC	Removal of Shopping Carts is Prohibited
15 ML	15 Minute Loading	EO	This Elevator is Open from 7am and closes at 9 pm
15M	15 Minute Parking 8:00a.m.-6:00p.m. Saturday and Sunday excluded	NO	NO (Pedestrian Crossing)
2 HR	2 Hour Parking 8:00 a.m.- 6:00 p.m. Saturdays, Sundays & Holidays Excepted	NTC	Notice All Pallets, steel racking, merchandise and trash is the property of Home Depot. It is unlawful to remove anything without expressed permission of The Home Depot. Aviso Todas las plataformas, estantes de acero, mercancía y desperdicios son propiedad de The Home Depot. Es ilegal tomar cualquier cosa sin la expresa autorización de The Home Depot
4 HP	4 Hour Parking for ID Plans Power Center customers only, No overnight parking allowed. Unauthorized vehicles will be towed at owner's expense CVC 22658(a) For towed vehicles call DCPD 991-8119	D1	Direction Sign
AS	Attention Shoppers! Our shopping carts will lock if taken beyond the parking lot perimeter. While distinctive yellow lines mark normal exits, the entire lot perimeter is protected. Nuestros carritos no funcionan fuera de los límites del estacionamiento. Aunque las líneas amarillas distintivas indican las salidas normales, todo el perímetro del estacionamiento está protegido	DS	Directional Sign
ATD	Attention Truck Drivers Upon Arrival you Must Adhere to these Rules: Deliveries are by appointment only. Identify which dock door to utilize. Back Truck/Trailer to dock door. Chock your Wheels. Lower your trailer landing gear. Report to the receiving area and present your paper work upon arrival. Do not enter the sales area of the store from Receiving. Before Departing you Must: Ensure all Home Depot Associates and equipment are out of the trailer before closing the dock door. Ensure dock door is closed by Home Depot Associate. Receive a key Rec # and signature from a Home Depot Associate	DNE	Do Not Enter
ATT	Attention Public parking prohibited Excepting Authorized Vehicles. Authorized vehicles are those whose occupants are Shopping in ID Plans Power Center while the Vehicles are Parked Here. Tenants and tenants employees vehicles are not authorized (they may be parked in the areas designated for tenants and employees) Unauthorized vehicles will be towed away at owner's expense in accordance with 1969 Calif. Vehicle Code 22658 Daly City Police Department Telephone Number 992-1225	DMC	Drivers must chock both wheels before load can be moved
	BUS STOP	END	END
		EX	EXIT ONLY
		EPS	Emergency Pump Shut Off Switch
		F	FDC SERVES BUILDING V BUILDING R UNIT #306 UNIT 310 314 318 322 326 332 336 340 344
		FEDNB	Fire Exit Do Not Block
		FLC	Fire Lane By city Ordinance No Parking Stopping Standing Loitering
		FSR	Fire Sprinkler Risers
		FV	Flammable Vapors No Smoking
		ICF	In Case of Fire do Not Use Elevators Use Stairs
		EO	Closed Circuit Television Cameras Las Camaras De Circuito Cerrado De Television are in use to help provide you with low prices. Recordings will be used in the se utilizan para ayudarnos a ofrecerle precios bajos. Las grabaciones se utilizaran en el Prosecution of Criminal Offenses Procesamiento De Delitos
		NBA	No Bicycles Allowed on Sidewalks
		NPTAZ	No Parking Tow Away Zone Vehicle will be impounded at Owner's Expense authority 22658 (a) CVC For towed vehicles call Daly City Police Dept. 991-8092
		NRT	No Right Turn
		NSCE	No Shopping Carts in Elevators
		NS	No Smoking
		NSP	No Smoking in Public Seating Areas
		NUT	No U Turn
		NWP	No Water Playing or Climbing on Fountain Rocks
		OW	One Way
		PPO	Parking by Permit Only Violators subject to citation and/or tow away at vehicle owner's expense Sec. 22658 CVC For towed vehicles Phone CDPD 992-1225
		Y	Pedestrian Crossing
			Yield Here To Pedestrians

The signage page identifies every sign on the property, its location and the exact wording on each sign.

ID Plans Mall

Signage
Page 1 of 7



Plans produced by:
ID Plans Corp
05/10/2012
(813) 657-2545



© 2012



The signage page identifies every sign on the property, its location and the exact wording on each sign.

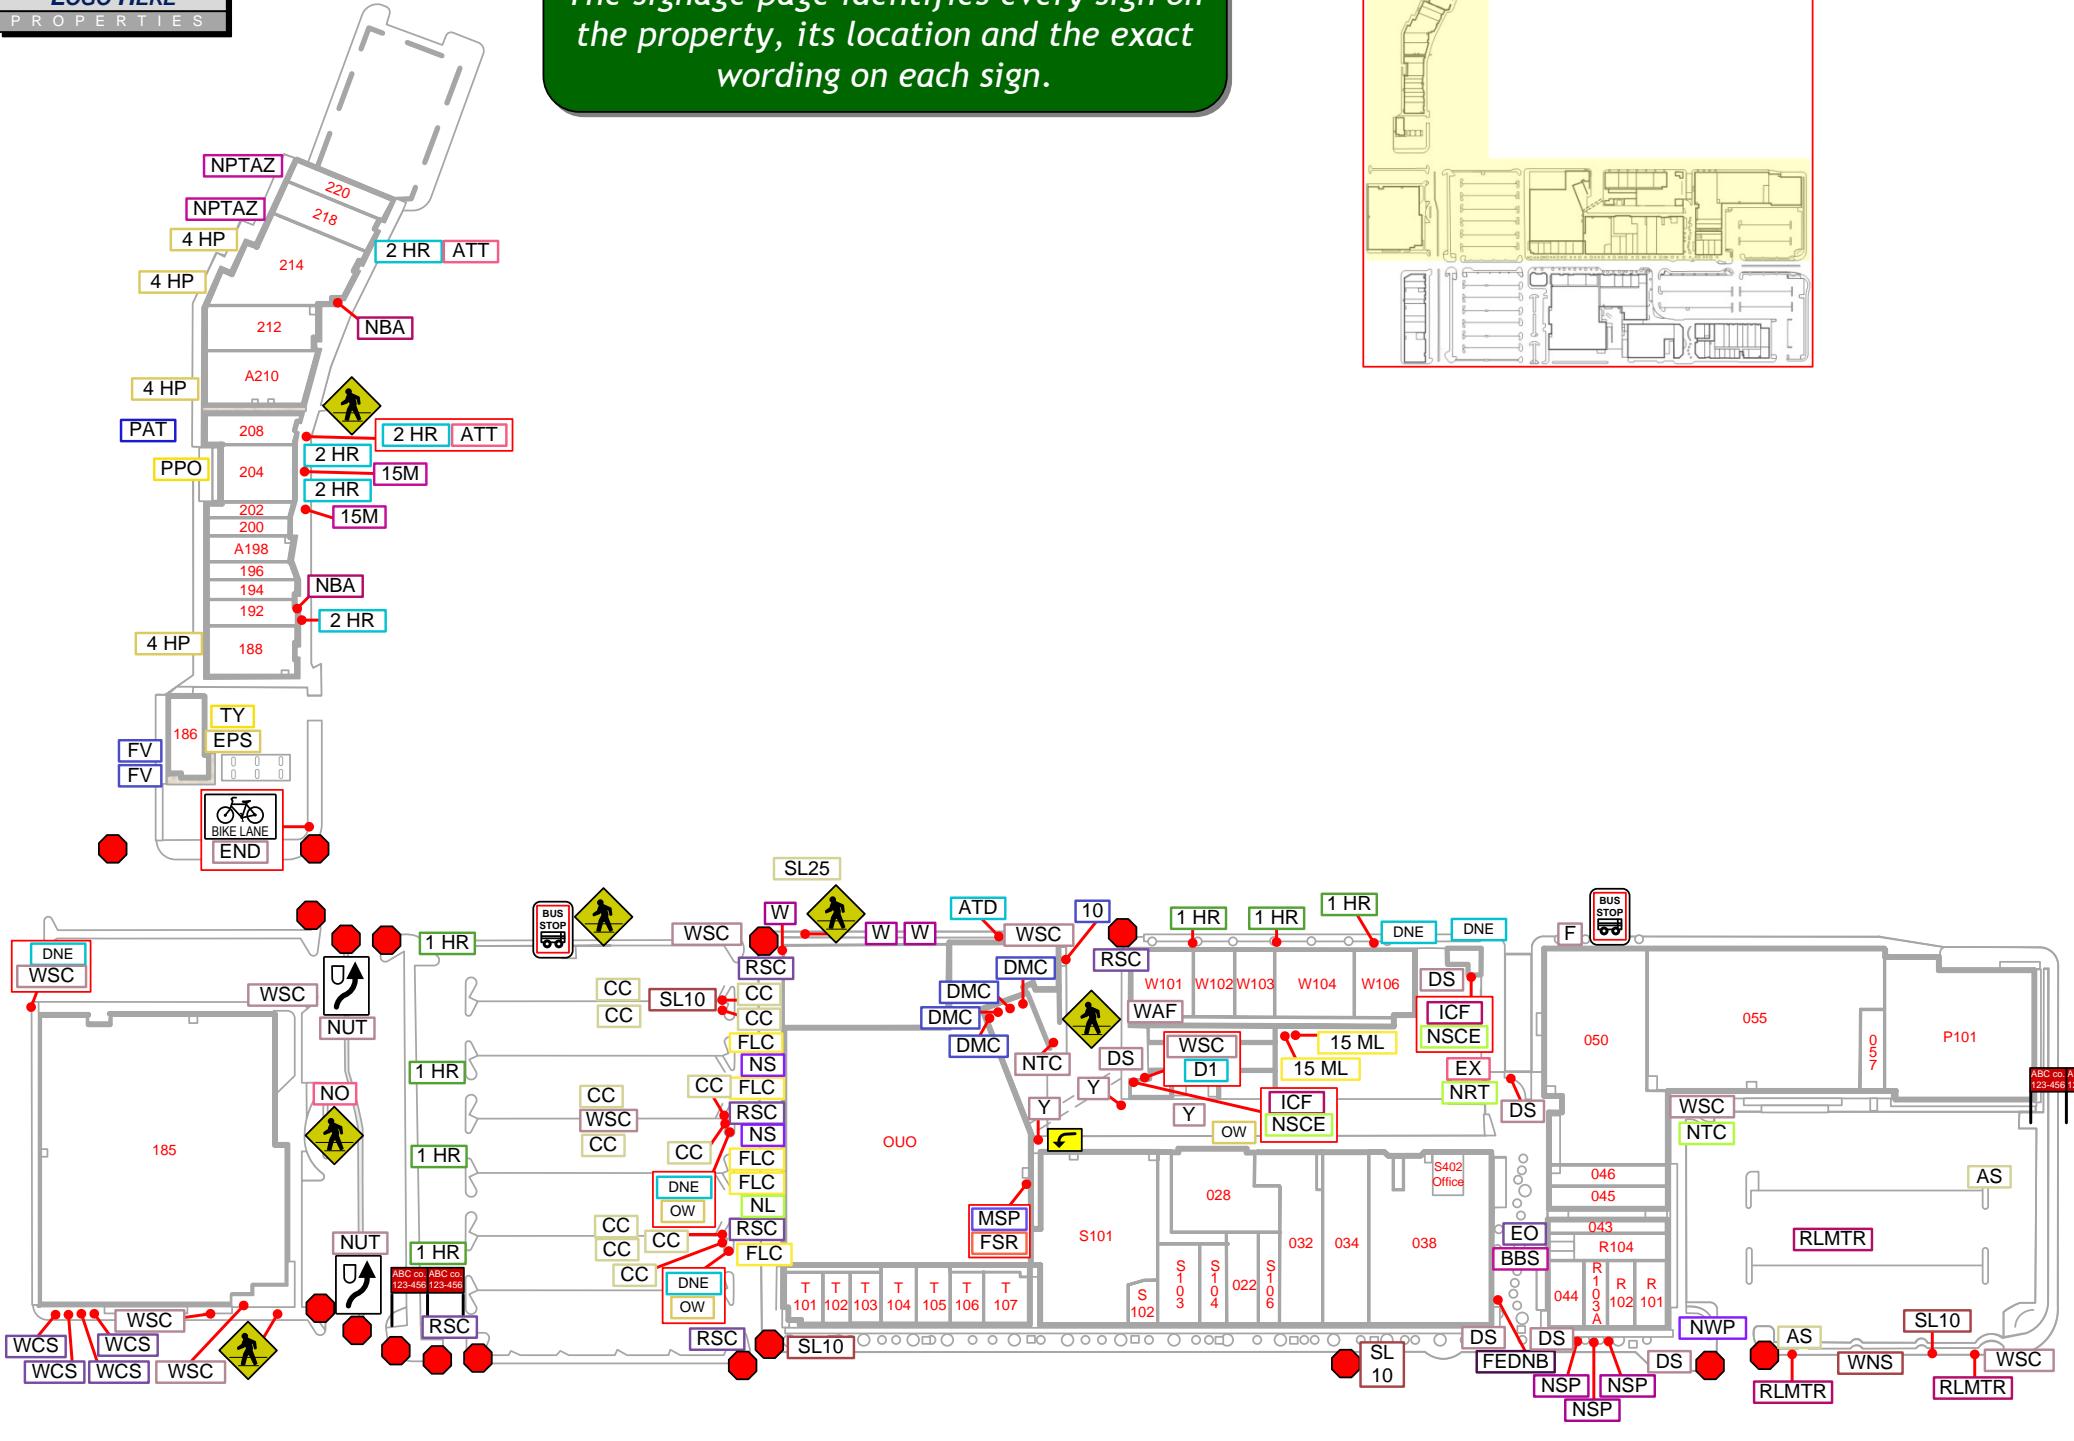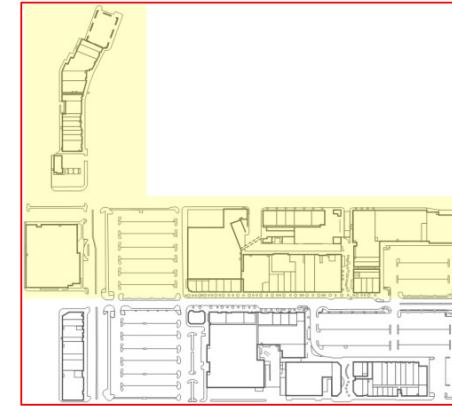




Plans produced by:
ID Plans Corp
05/10/2012
(813) 657-2545



© 2012



The signage page identifies every sign on the property, its location and the exact wording on each sign.

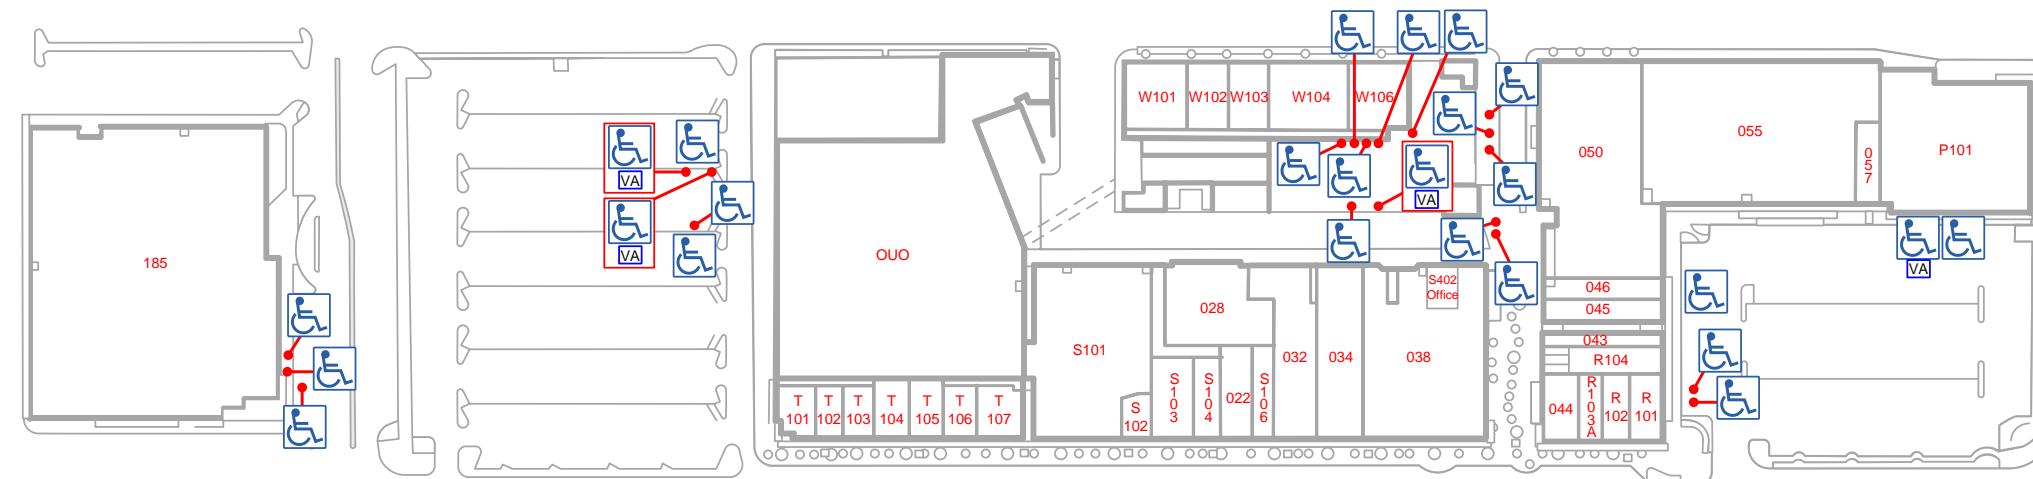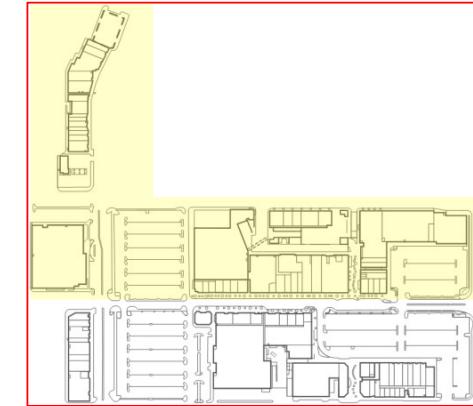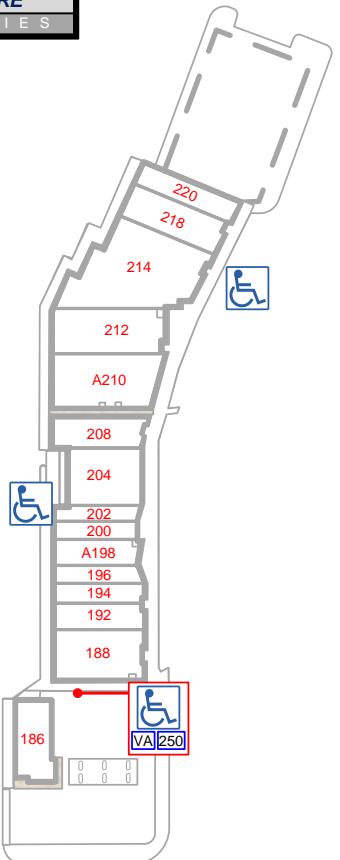


Plans produced by:
ID Plans Corp
05/10/2012
(813) 657-2545




© 2012

Signage	
Page 3 of 7	
250	\$250 Fine
	Handicap
	Van Accessible

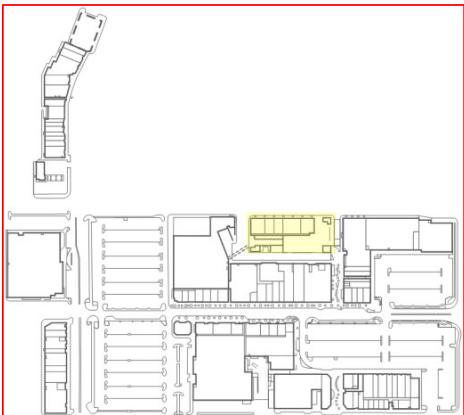

The signage page identifies every sign on the property, its location and the exact wording on each sign.

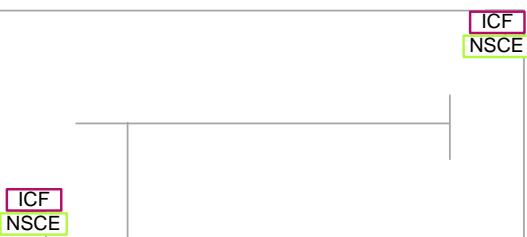


Fifth Level




Fourth Level



Third Level

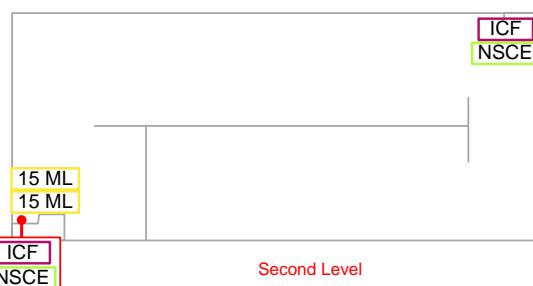

Second Level

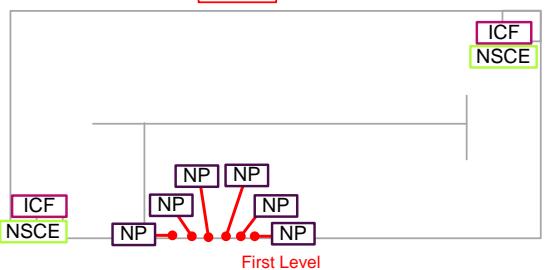

First Level

Signage

Page 4 of 7

15 ML	15 Minute Loading
ICF	In Case of Fire do Not Use Elevators Use Stairs
NP	No Parking
NSCE	No Shopping Carts in Elevators

Plans produced by:
ID Plans Corp
05/10/2012
(813) 657-2545



© 2012



The signage page identifies every sign on the property, its location and the exact wording on each sign.

Signage

Page 5 of 7

	1 Hour Parking to 8:00 a.m.- 6:00 p.m. Except Sundays & Holidays		Notice All Pallets, steel racking, merchandise and trash is the property of Home Depot. It is unlawful to remove anything without expressed permission of The Home Depot. Aviso Todas las plataformas, estantes de acero, mercancía y desperdicios son propiedad de The Home Depot. Es ilegal tomar cualquier cosa sin la expresa autorización de The Home Depot		Removal of Shopping Carts is Prohibited
	2 Hour Parking 8:00 a.m.- 6:00 p.m. Saturdays, Sundays & Holidays Excepted				Speed Limit 10
	4 Hour Parking for ID Plans Power Center customers only, No overnight parking allowed				Stop Sign
	25 Speed Limit		No Dumping \$100 Fine By Order of the Health Department		Vehicle Access Only
	Authorized Personnel Only		No Dumping Tenants Only Violators will be Prosecuted to the Fullest Extent the Law Allows PC374		No Soliciting No Distribution of Handbills Flyers or Advertisements No Loitering No Skateboarding or Skating No Unruly Conduct No Animals Other than Service Dogs No Smoking in Public Seating Areas No unlawful or Unauthorized Use of Property Private Property Conduct rules for the comfort and safety of our Patrons and General Public
	Bus Stop		No Parking For Safeway		
	Caution Cart will Stop suddenly if taken beyond the yellow line Cuidado: Carrito se detendra repentinamente si pasa la linea amarilla		No Pedestrian Access		
	DO NOT ENTER		No Right Turn		
	Directory Sign		No U Turn		Unauthorized vehicles not displaying distinguishing placards or license plates issued for physically handicapped persons will be towed away at owner's expense CVC 22511.8 Private Property Unauthorized or improperly parked vehicles are subject to immediate tow at owner's expense. No overnight parking, no parking in excess of four (4) hours. CVC 22658(a) CVC 22658 DCPD (650) 991-8119 For towed vehicles call Big Guys Towing 630-359-5163
	Doors Must be closed at all times		RIGHT TURN ONLY		
	Enter		ParaTransit Redi Wheels		
	Lane Ends Merge Left		Pedestrian Crossing		
	NO PARKING ANY TIME		Place All Trash in Bins Do Not Leave Materials on Ground		


Plans produced by:
ID Plans Corp
05/10/2012
(813) 657-2545



© 2012



The signage page identifies every sign on the property, its location and the exact wording on each sign.

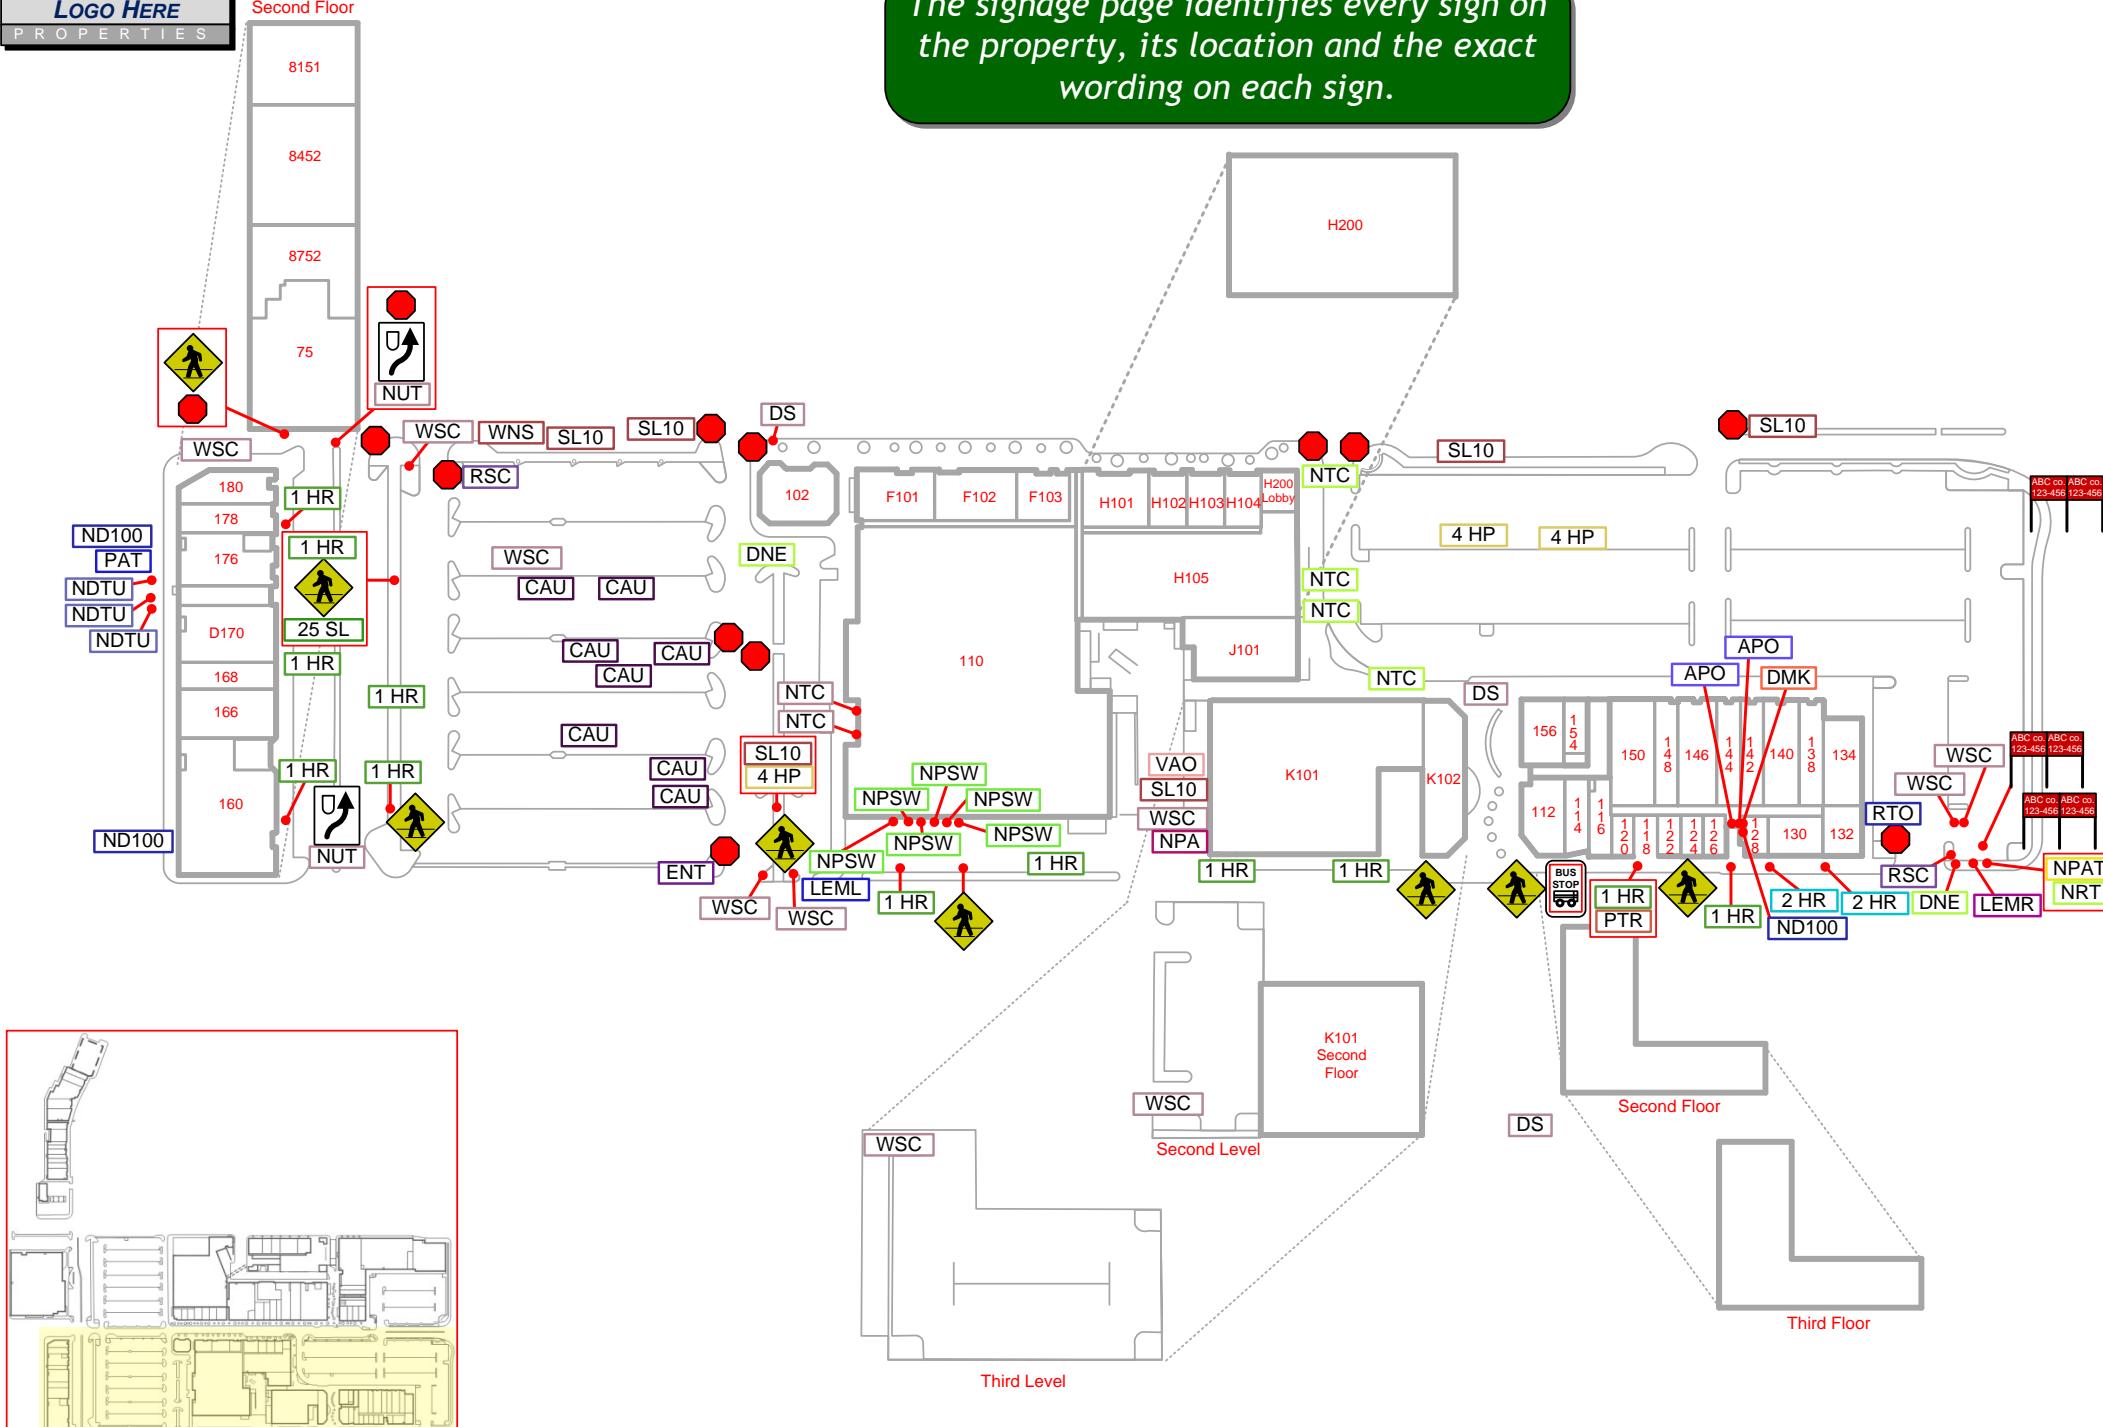

Plans produced by:
ID Plans Corp
05/10/2012
(813) 657-2545



© 2012





The signage page identifies every sign on the property, its location and the exact wording on each sign.

Signage

Page 7 of 7

	Handicap
	Van Accessible

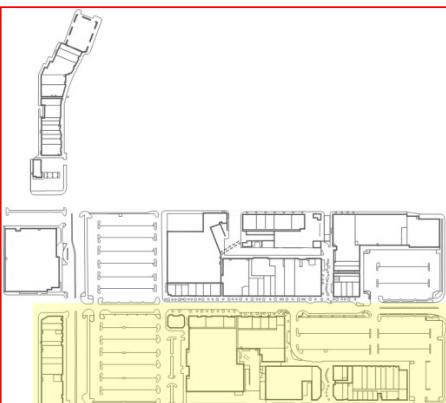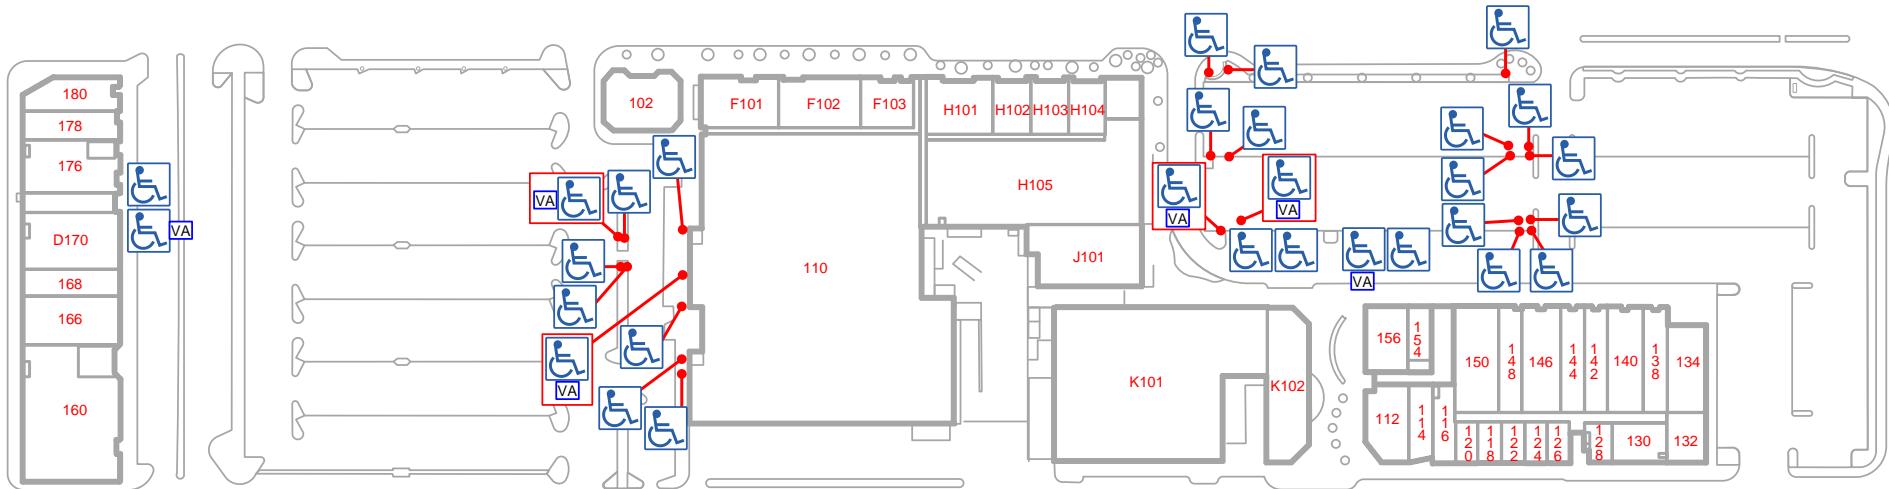

Plans produced by:
ID Plans Corp
05/10/2012
(813) 657-2545



© 2012

The space site plan locates the space for each tenant, the name of the tenant and the square footage of the space.

Space Numbers & Square Footage											
Space #	Address	Tenant Name	Square Footage	Space #	Address	Tenant Name	Square Footage				
SOUTHGATE AVE.											
220	251	YONG IN MARTIAL ARTS ACADEMY	1,436	S103	448	AVAILABLE	3,017				
218	235	AVAILABLE	2,327	S104	444	AVON	1,763				
214	209-219	KING WAH RESTAURANT	7,161	022	440	DALE CITY OPTOMETRY	2,060				
212	207	KUMON LEARNING CENTER	3,500	S106	436	GAMESTOP	1,432				
A210	203	AVAILABLE	4,100	028	416	BANANA ISLAND	5,200				
208	201	BANGKOK GARDEN	1,980	032	432	HOLLYWOOD VIDEO	6,400				
204	199	UNITED STATES POST OFFICE	3,175	034	420	PARTY WAREHOUSE	5,475				
202	189	MANNY'S HAIRCUT	1,100	038	418	BEVERLYS	14,427				
200	187	GENESIS DENTAL	1,275	S111	418 (LOWER LEVEL)	AVAILABLE	13,500				
A198	183	H&R BLOCK	1,500	S402	402	LE, HO & COMPANY, LLP	2,633				
196	181	TIMES SALON	1,125	044	344	DAPHNE'S GREEK CAFÉ	1,800				
194	177	SUBWAY	1,350	R103 A	340	JAMBA JUICE	1,200				
192	175	QUICKLY	1,370	R102	336	AT&T	1,181				
188	169	WESTLAKE COIN LAUNDRY	3,000	R101	332	STARBUCKS	1,600				
186	151	ARCO	18,731	R104	326	WESTLAKE VISION CENTER/VISION CENTER OPTOMETRY	1,440				
185	99	BURLINGTON COAT FACTORY	55,000	043	322	GEORGETTE'S OF WESTLAKE	1,650				
O10	700	HOME DEPOT	109,000	045	314	SLIDER'S DINER	2,000				
WESTLAKE CENTER											
T101	526	SHENG KEE BAKERY	1,641	046	310	BASKIN ROBBINS	980				
T102	518	AVAILABLE	1,172	050	306	DSW SHOES	17,280				
T103	522	AVAILABLE	1,328	055	216	WALGREENS	30,745				
T104	514	KICK CITY	1,498	057	200	GNC	1,343				
T105	508	LOBELLA	1,338	P101	100	T.J. MAXX (2 LEVELS)	26,780				
T106	506	DAI ICHI	1,493	LAKE MERCED BLVD.							
T107	500	YOGURT CIRCLE	1,582	W101	494	MASSAGE ENVY SALON	2,885				
S101	468	FURNITURE GALLERY	14,117	W102	490	WESTLAKE NAIL SALON	1,825				
S102	456	CLAIRE'S	948	W103	486	AVAILABLE (COMING SOON WINGSTOP RESTAURANT)	1,825				
				W104	482	AVAILABLE	3,650				
				W106	470-474 A-B	LITTLE FIRE POT/DIM SUM BAKERY	2,755				
Sub Total Square Footage											
399,093											

Plans produced by:
ID Plans Corp
05/10/2012
(813) 657-2545




© 2012



The space site plan locates the space for each tenant, the name of the tenant and the square footage of the space.

Space

Page 2 of 6

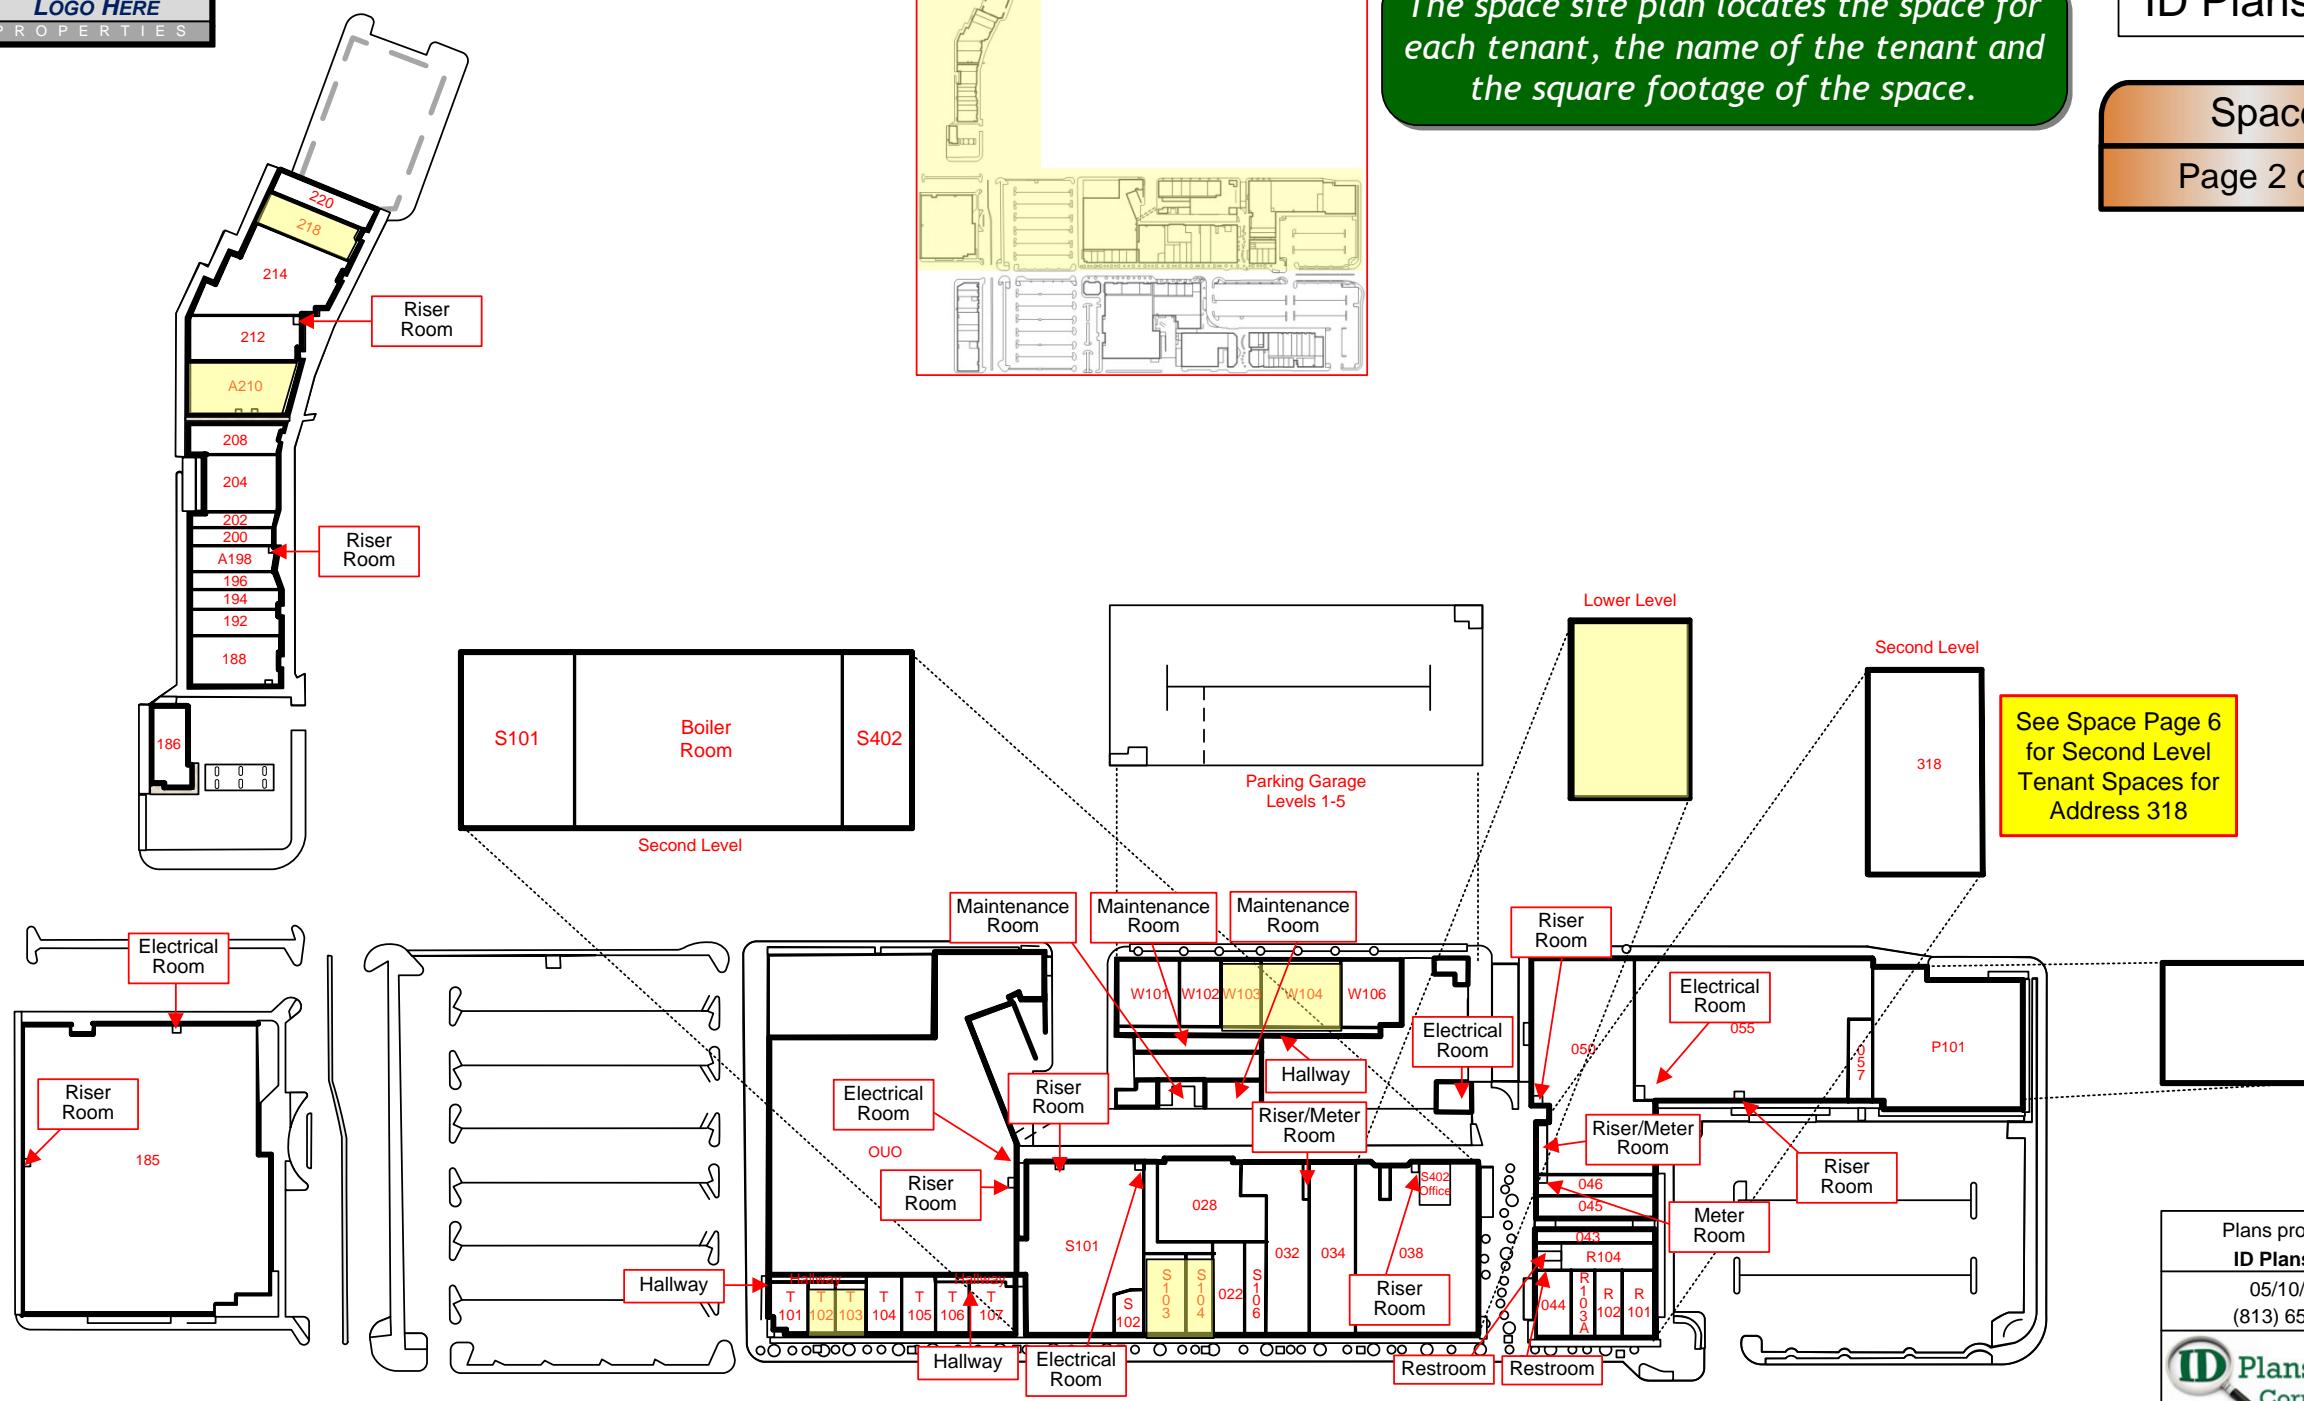

The space site plan locates the space for each tenant, the name of the tenant and the square footage of the space.

Space Numbers & Square Footage											
Space #	Address	Tenant Name	Square Footage	Space #	Address	Tenant Name	Square Footage				
SOUTHGATE AVE.											
8151	15	KAISER PERMANENTE HEARING CENTER	2,810	K101	405	ROSS DRESS FOR LESS	39,050				
8452	45	SETON MEDICAL CENTER	13,111	K102	403	SLEEP TRAIN	4,206				
75	75	2ND FLOOR	12,614	156	335	WESTLAKE COFFEE SHOP	1,831				
8752	75	AVAILABLE	6,471	154	331	WESTLAKE HEARING AID CENTER	838				
180	95	US BANK	2,880	150	247	T-MOBILE	3,280				
178	85	PHO'HUYNH HIEP 3	2,700	148	243	BROASTER CHICKEN	1,200				
176	65	PATELCO CREDIT UNION	2,606	146	239	BANK OF THE WEST	2,925				
D170	33	BANK OF AMERICA	6,236	144	235	THE UPS STORE	2,400				
168	25	TOKYO TERIYAKI JAPANESE CUISINE	1,800	142	227	RED WING SHOES	825				
166	19	HSBC	2,976	140	223	RADIO SHACK	2,177				
160	5	CHASE	7,800	138	215	SUPERCUTS	1,200				
110	601	SAFEWAY	52,000	PARK PLAZA DRIVE							
WESTLAKE CENTER											
102	701	88 RICE BOWL	2,970	134	213	CHIPOTLE MEXICAN GRILL	4,016				
F101	515	KANA JAPANESE CUISINE	3,000	132	201	NATIONS GIANT HAMBURGERS	1,350				
F102	511	GERRY'S GRILL	2,978	130	203	DANCO REAL ESTATE	1,267				
F103	507	BURGERMEISTERS HAMBURGERS	1,935	128	207	ELITE HAIR SALON	720				
H101	457	VERIZON WIRELESS	2,500	126	301	TANI'S KITCHEN	473				
H102	451	GOOD FEET	1,460	124	305	MAGIC TOUCH BEAUTY SALON	468				
H103	445	COLOR ME MINE	1,460	122	309	PULIDO'S TAILOR	490				
H104	441	MIKI	1,492	118	313	WESTLAKE ART GALLERY	540				
H105	417	TRADER JOE'S	14,040	120	317	WESTLAKE SHOE REPAIR	460				
H200	423	COST PLUS WORLD MARKET	22,900	116	321	STRUCTURE HAIR DESIGN	1,070				
J101	415	SAN MATEO CREDIT UNION	4,445	114	325	CIGARETTES "R" CHEAPER	900				
				112	327	WESTLAKE LIQUORS	2,000				
Sub Total Square Footage						246,870					



Plans produced by:
ID Plans Corp
05/10/2012
(813) 657-2545



© 2012



The space site plan locates the space for each tenant, the name of the tenant and the square footage of the space.

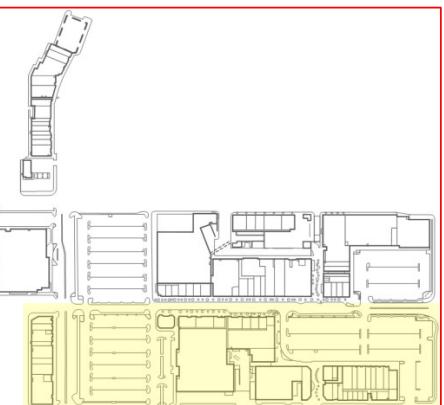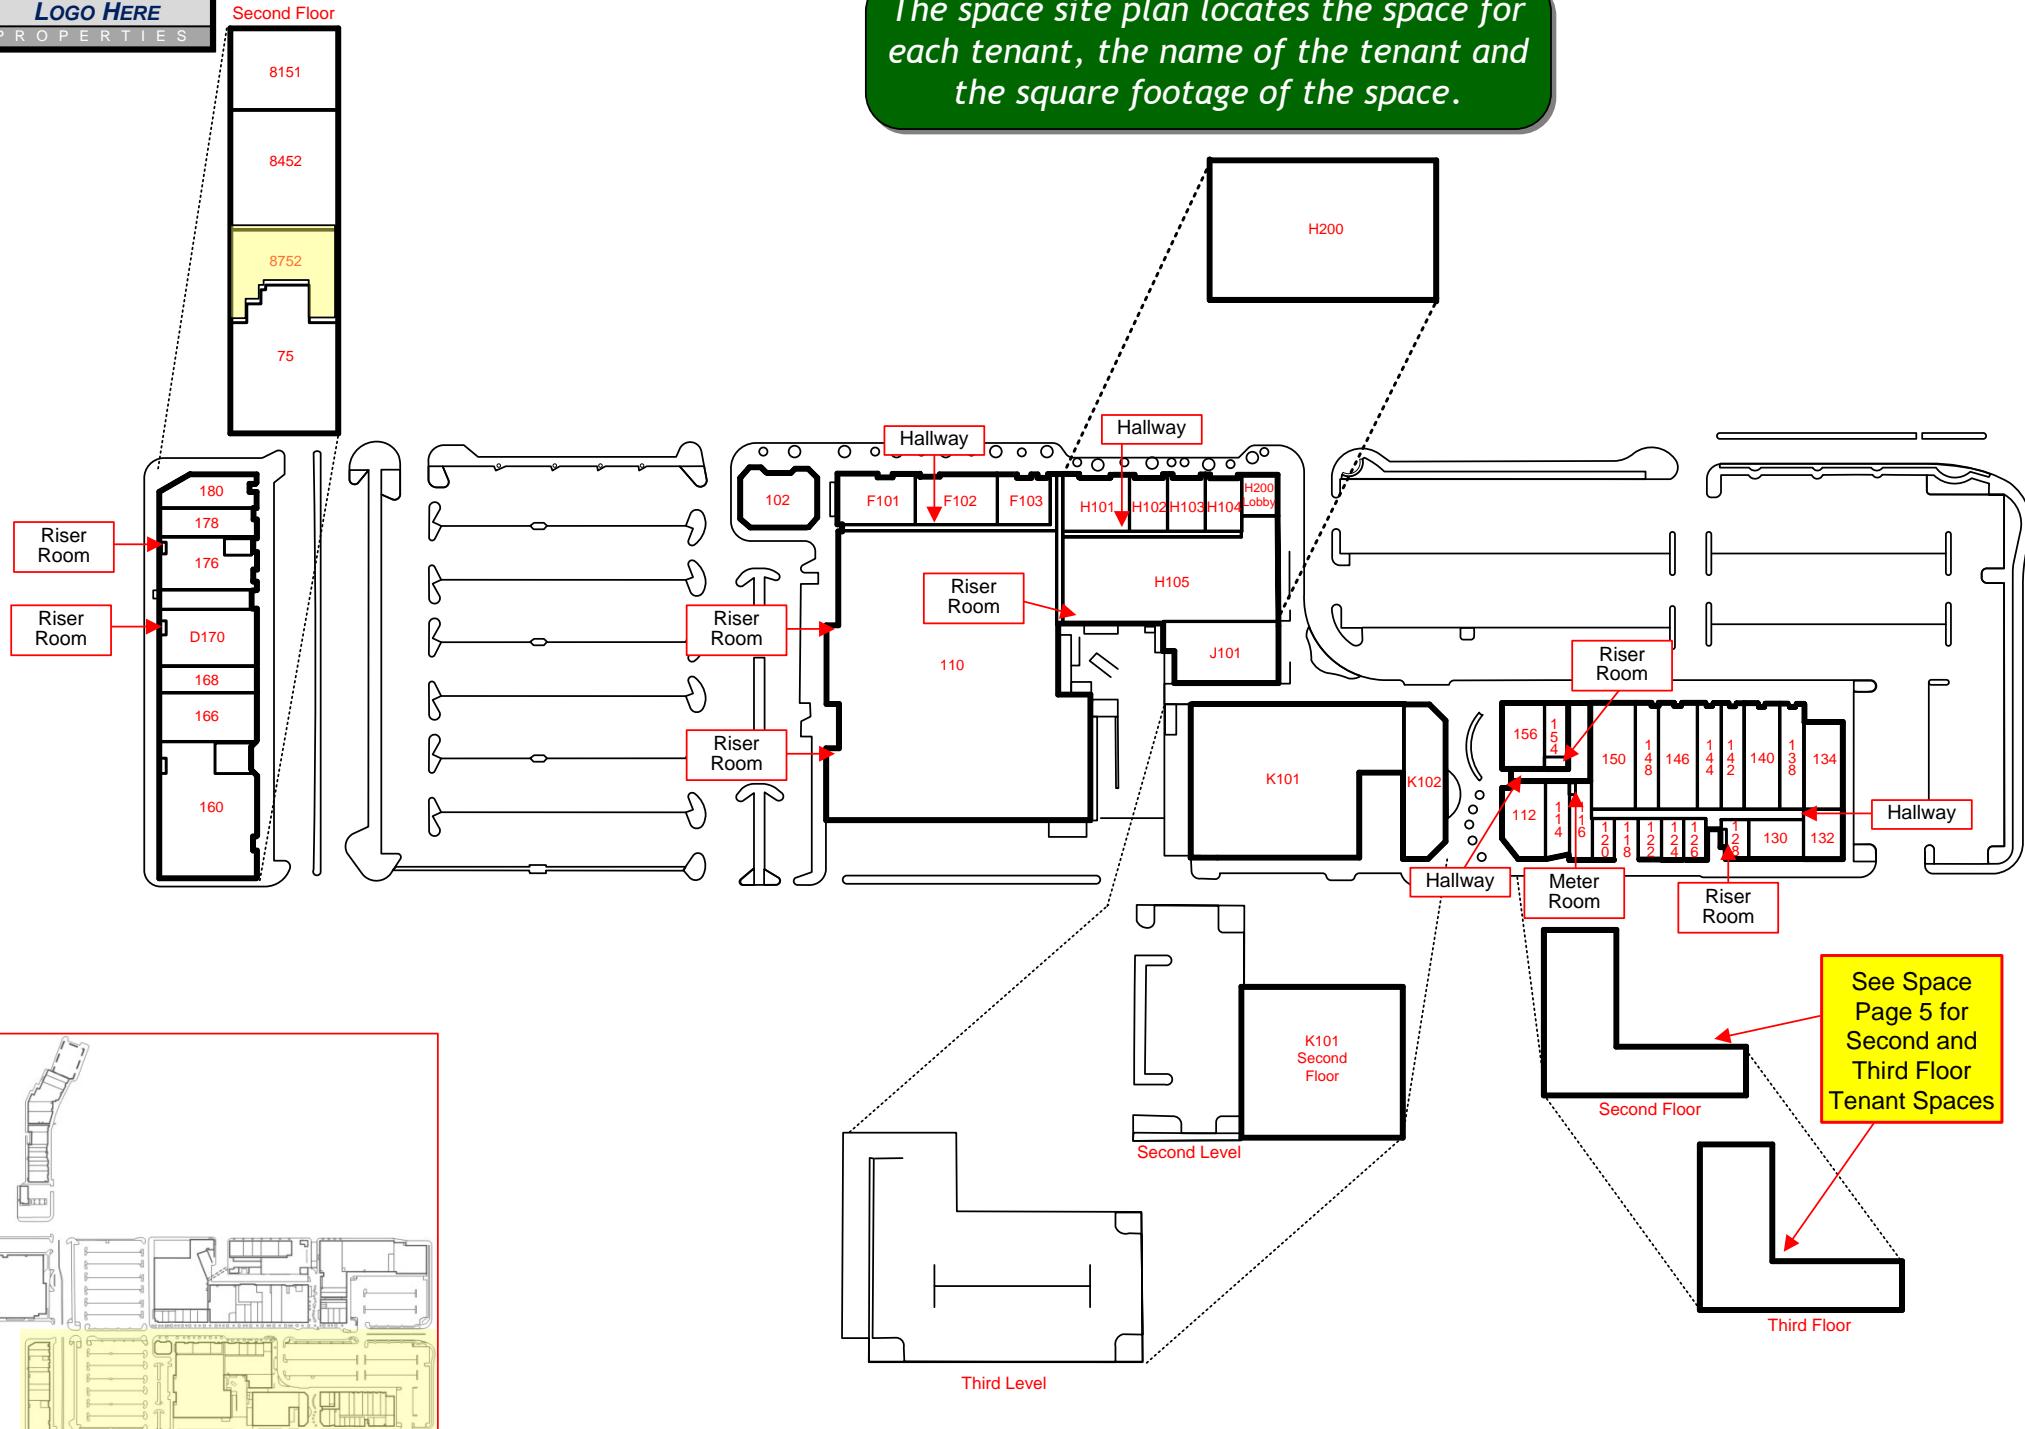


Plans produced by:
ID Plans Corp
05/10/2012
(813) 657-2545



© 2012

Second Floor

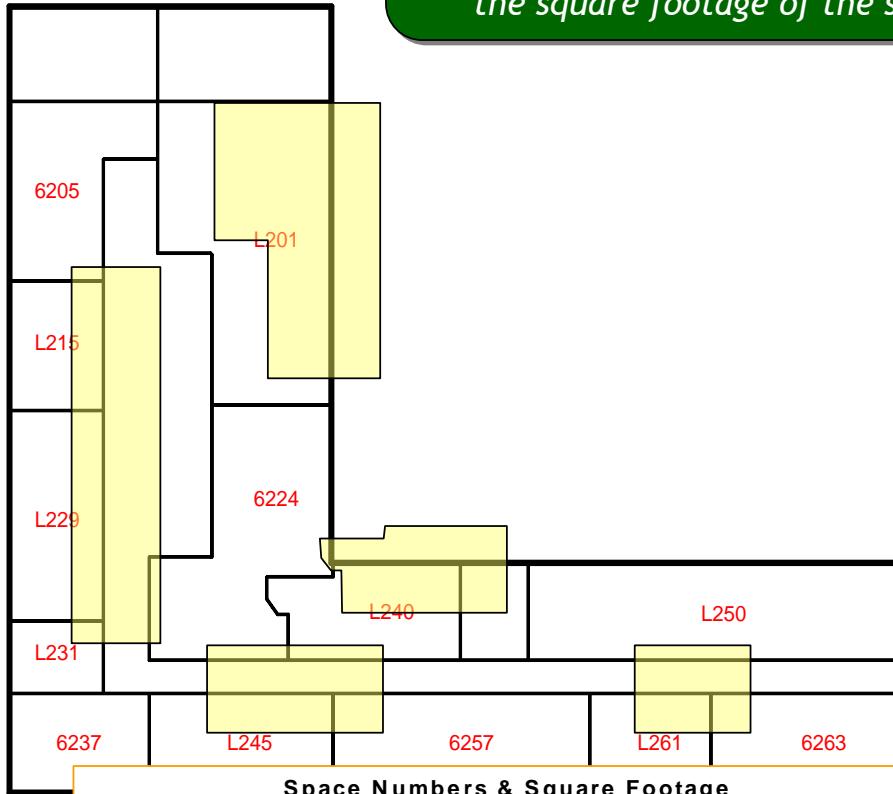


Space Numbers & Square Footage

Space #	Address/Suite #	Tenant Name	Square Footage
WESTLAKE CENTER			
6205	341/205	DR. MICHAEL W. JOHNSTON DDS	925
L215	341/215	AVAILABLE	423
L229	341/229	AVAILABLE	1,453
L231	341/231	AVAILABLE	342
6237	341/237	DR. RODOLFO C. VILLASIN DDS	520
L245	341/245	AVAILABLE	648
6257	341/257	DR. ANTHONY J. ERRICO DPM	818
L261	341/261	AVAILABLE	477
6263	341/263	DR. SUSAN R. SHELDON DDS MS	771
L250	341/250	WESTLAKE SLEEP CENTER	1,037
L240	341/240	AVAILABLE	574
6224	341/224	DR. ARASH ZEDAH DDS	810
L201	341/201	AVAILABLE	2,999
Sub Total Square Footage			11,797

The space site plan locates the space for each tenant, the name of the tenant and the square footage of the space.

Third Floor

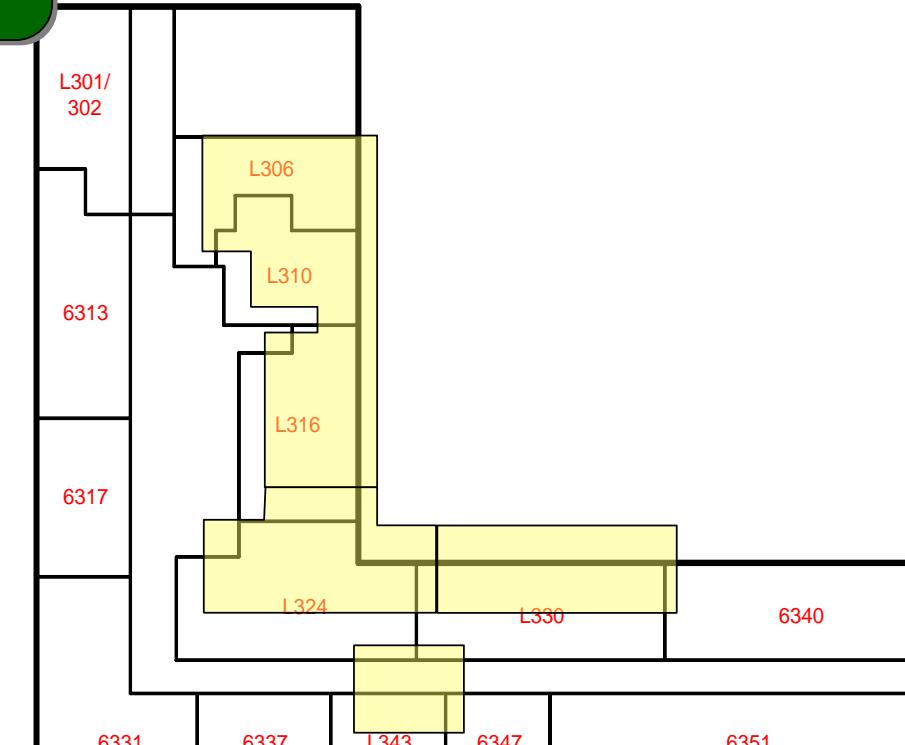

Space Numbers & Square Footage

Space #	Address/Suite #	Tenant Name	Square Footage
WESTLAKE CENTER			
L301	341/301/302	DR. CHARLES Y LO MD/DR. JAYSON LO DMD	1,632
6313	341/313	DR. ROGER WEINGARTNER DPM	987
6317	341/317	DR. VIVIAN D. HERNANDEZ MD	600
6331	341/331	ADVANCED DENTURE CARE	1,023
6337	341/337	BUSH DENTAL	527
L343	341/343	AVAILABLE	485
6347	341/347	MEDICAL DOCTORS	500
6351	341/351	DR. MARK NI DDS	1,150
6340	341/340	WALLACE W YUEN ACUPUNCTURE	750
L330	341/330	AVAILABLE	800
L324	341/324	AVAILABLE	946
L316	341/316	AVAILABLE	620
L310	341/310	AVAILABLE	457
L306	341/306	AVAILABLE	702
Sub Total Square Footage			11,179


Plans produced by:
ID Plans Corp
05/10/2012
(813) 657-2545



© 2012



Second Level

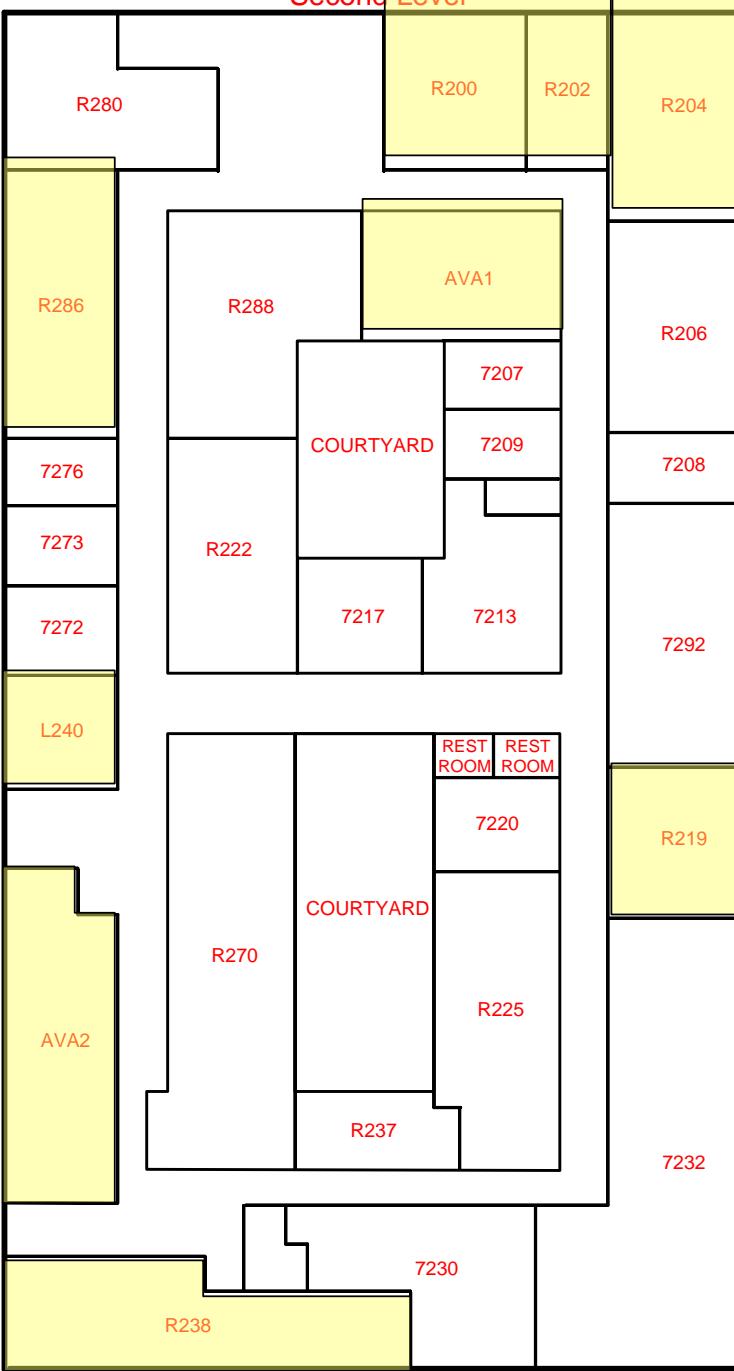

The space site plan locates the space for each tenant, the name of the tenant and the square footage of the space.

ID Plans Mall

Space
Page 6 of 6

Space Numbers & Square Footage

Space #	Address/Suite #	Tenant Name	Square Footage
WESTLAKE CENTER			
R280	318/280	SHAMES CONSTRUCTION	525
R200	318/200	AVAILABLE	427
R202	318/202	AVAILABLE	320
R204	318/204	AVAILABLE	345
R206	318/206	PROBITE DENTAL LAB	372
7208	318/208	FARMERS INSURANCE, CALY CAYABYAB	310
7292	318/292	ABDULLAH ACCOUNTING SERVICE, INC.	880
R219	318/219	AVAILABLE	490
7232	318/232	STATEWIDE REALTY	1,370
7230	318/230	JACKSON HEWITT TAX SERVICE	475
R238	318/238	AVAILABLE	518
AVA2	318/239	AVAILABLE	685
L240	318/240	AVAILABLE	553
7272	318/272	RIVER PAST CORP.	200
7273	318/274	898 DALY INC (ALSO KNOWN AS GREAT HIGHWAY ENTERPRISES)	200
7276	318/276	SSC REALTY & ASSOC., INC.	200
R286	318/286	AVAILABLE	610
R288	318/288	FUN FIVE TRADING, LLC	444
AVA1	318/205	AVAILABLE	671
7207	318/207	CITY & COUNTY AUTO SALES/LEASING	170
7209	318/209	MICHAEL H. SAMSON, CHB CONS.	189
7213	318/213	MADE IN BRAZIL PLUS	260
7217	318/217	FARMERS INSURANCE, JERRY WU	250
R222	318/222	ERA INFINITY	414
7220	318/220	ARNOLD INSURANCE BROKER	285
R225	318/225	LAN ENGINEERING CORP.	600
R237	318/237	ELSO COSMETIC COMPANY	330
R270	318/270	STATE FARM, GARY TU	1,320
Sub Total Square Footage			13,413
TOTAL SQUARE FOOTAGE - ALL PAGES			682,352



The storm drain site plan identifies the size and quantity of catch basins and their location, as well as the location of storm drains and spillways.




	Catch Basin 26 1/2" x 48" Grate		Catch Basin 19 1/2" x 37 1/2" Grate		Catch Basin 26 1/2" x 48" Grate		Round Catch Basin 26" Grate		Square Catch Basin 16" x 16" Grate
	Catch Basin 16 1/2" x 22 1/2" Grate		Catch Basin 24" x 26 1/2" Grate		Catch Basin 27" x 36" Grate		Round Catch Basin 8 3/4" Grate		Storm Drain
	Catch Basin 17" x 21" Grate		Catch Basin 24" x 36 1/2" Grate		Catch Basin 5 1/2" x 20" Grate		Square Catch Basin 4 1/2" x 4 1/2" Grate		Storm Drain Manhole Cover
	Catch Basin 17" x 25" Grate		Catch Basin 24" x 40" Grate	# icon"/>	Catch Basin w/ Number of Grates				

Plans produced by:
ID Plans Corp
05/10/2012
(813) 657-2545



© 2012

The storm drain site plan identifies the size and quantity of catch basins and their location, as well as the location of storm drains and spillways.

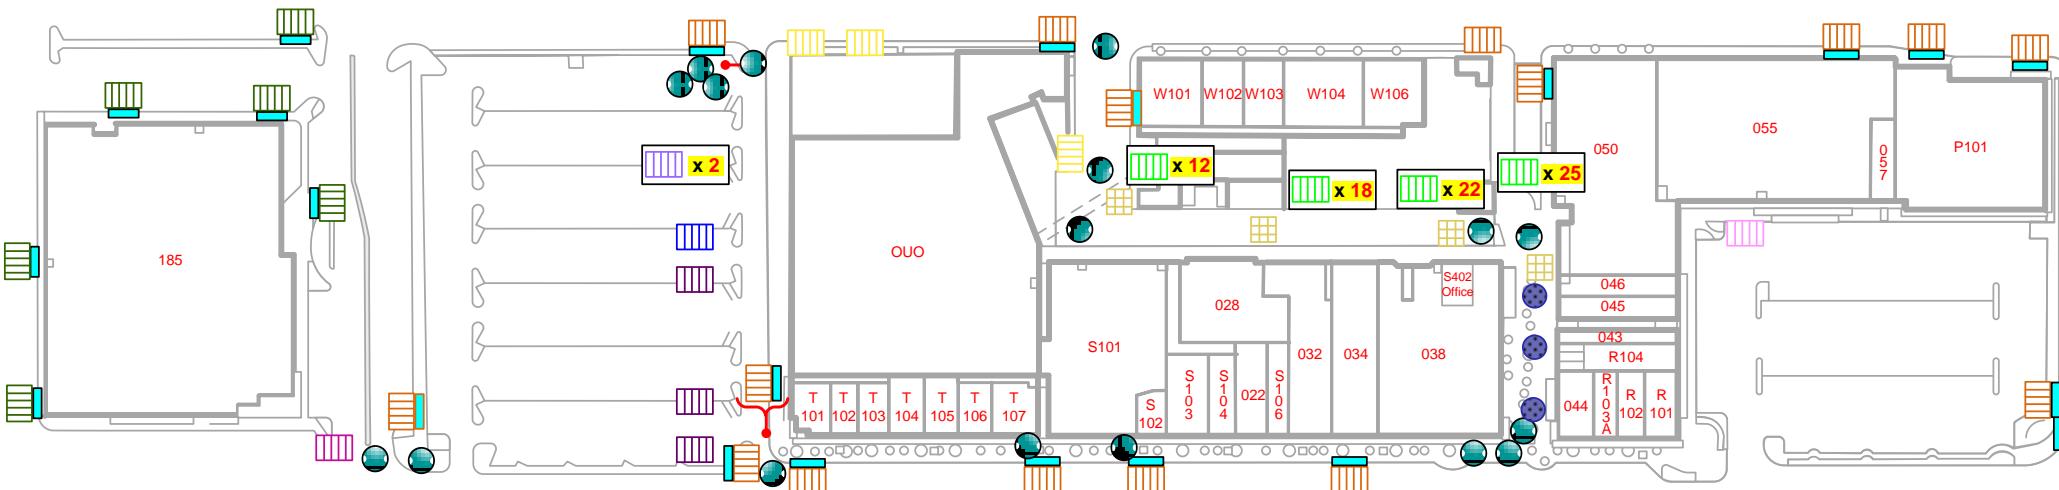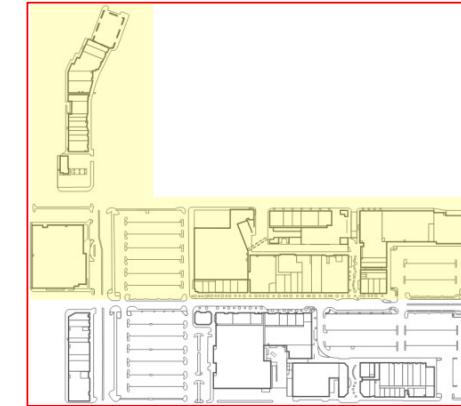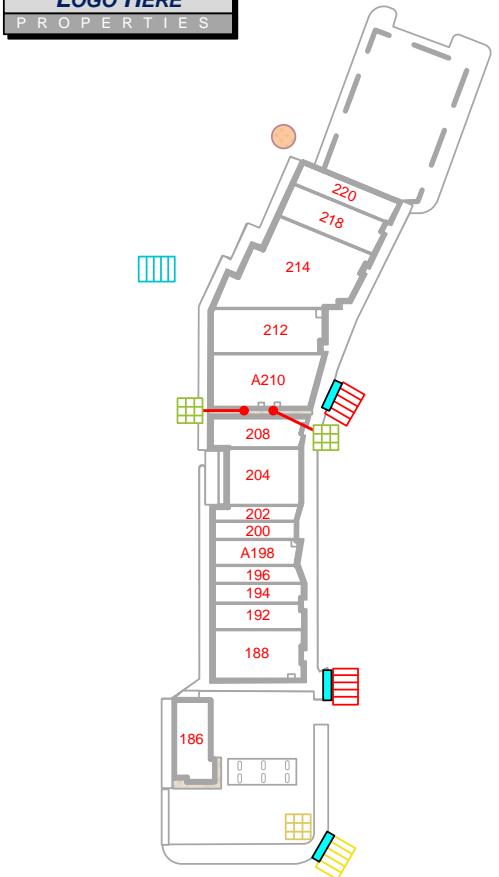


Plans produced by:
ID Plans Corp
05/10/2012
(813) 657-2545



© 2012

The storm drain site plan identifies the size and quantity of catch basins and their location, as well as the location of storm drains and spillways.

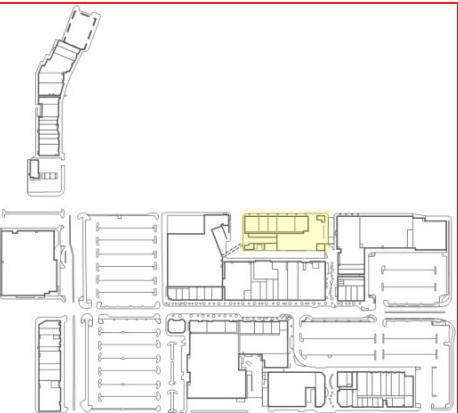

Fifth Level




Fourth Level



Third Level



Second Level

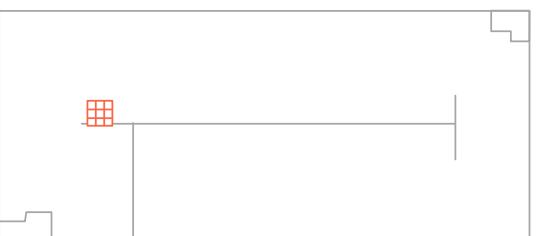

First Level

Storm Drain



Page 3 of 5

Square Catch Basin
11 1/2" x 11 1/2" Grate

Plans produced by:
ID Plans Corp
05/10/2012
(813) 657-2545



© 2012

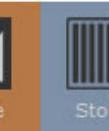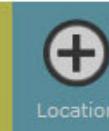




The storm drain site plan identifies the size and quantity of catch basins and their location, as well as the location of storm drains and spillways.

	Catch Basin 13 3/4" x 17 3/4" Grate		Catch Basin 23 1/2" x 29" Grate		Catch Basin w/ Number of Grates		Square Catch Basin 14 1/2" x 14 1/2" Grate		Square Catch Basin 39" x 39" Grate
	Catch Basin 15 1/2" x 35" Grate		Catch Basin 24" x 26 1/2" Grate		Round Catch Basin 8 3/4" Grate		Square Catch Basin 20" x 20" Grate		Storm Drain
	Catch Basin 17" x 22 1/2" Grate		Catch Basin 24" x 40" Grate		Square Catch Basin 12" x 12" Grate		Square Catch Basin 23 3/4" x 23 3/4" Grate		Storm Drain Manhole Cover
	Catch Basin 18" x 20 1/2" Grate		Catch Basin 26 1/2" x 36" Grate		Square Catch Basin 13" x 13" Grate		Square Catch Basin 26 1/2" x 26 1/2" Grate		

Plans produced by:
ID Plans Corp
05/10/2012
(813) 657-2545



© 2012

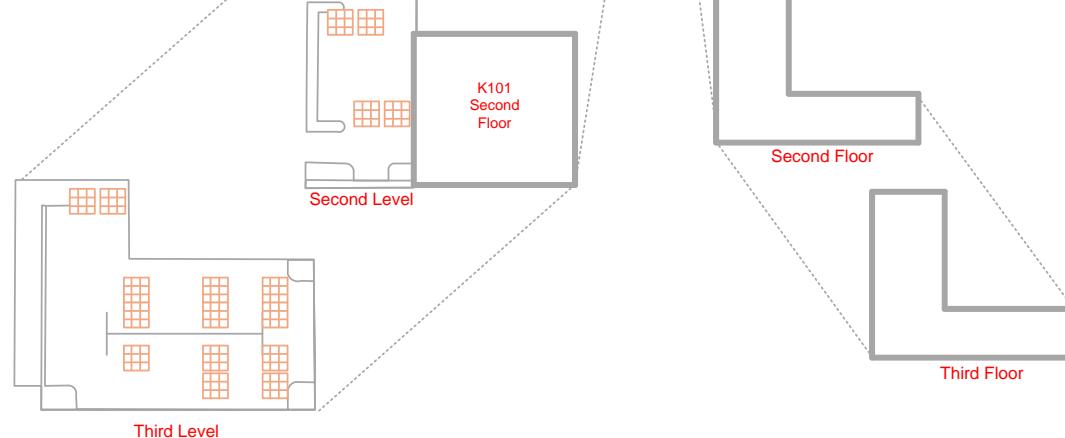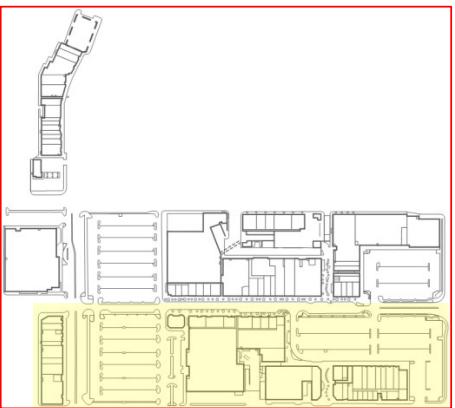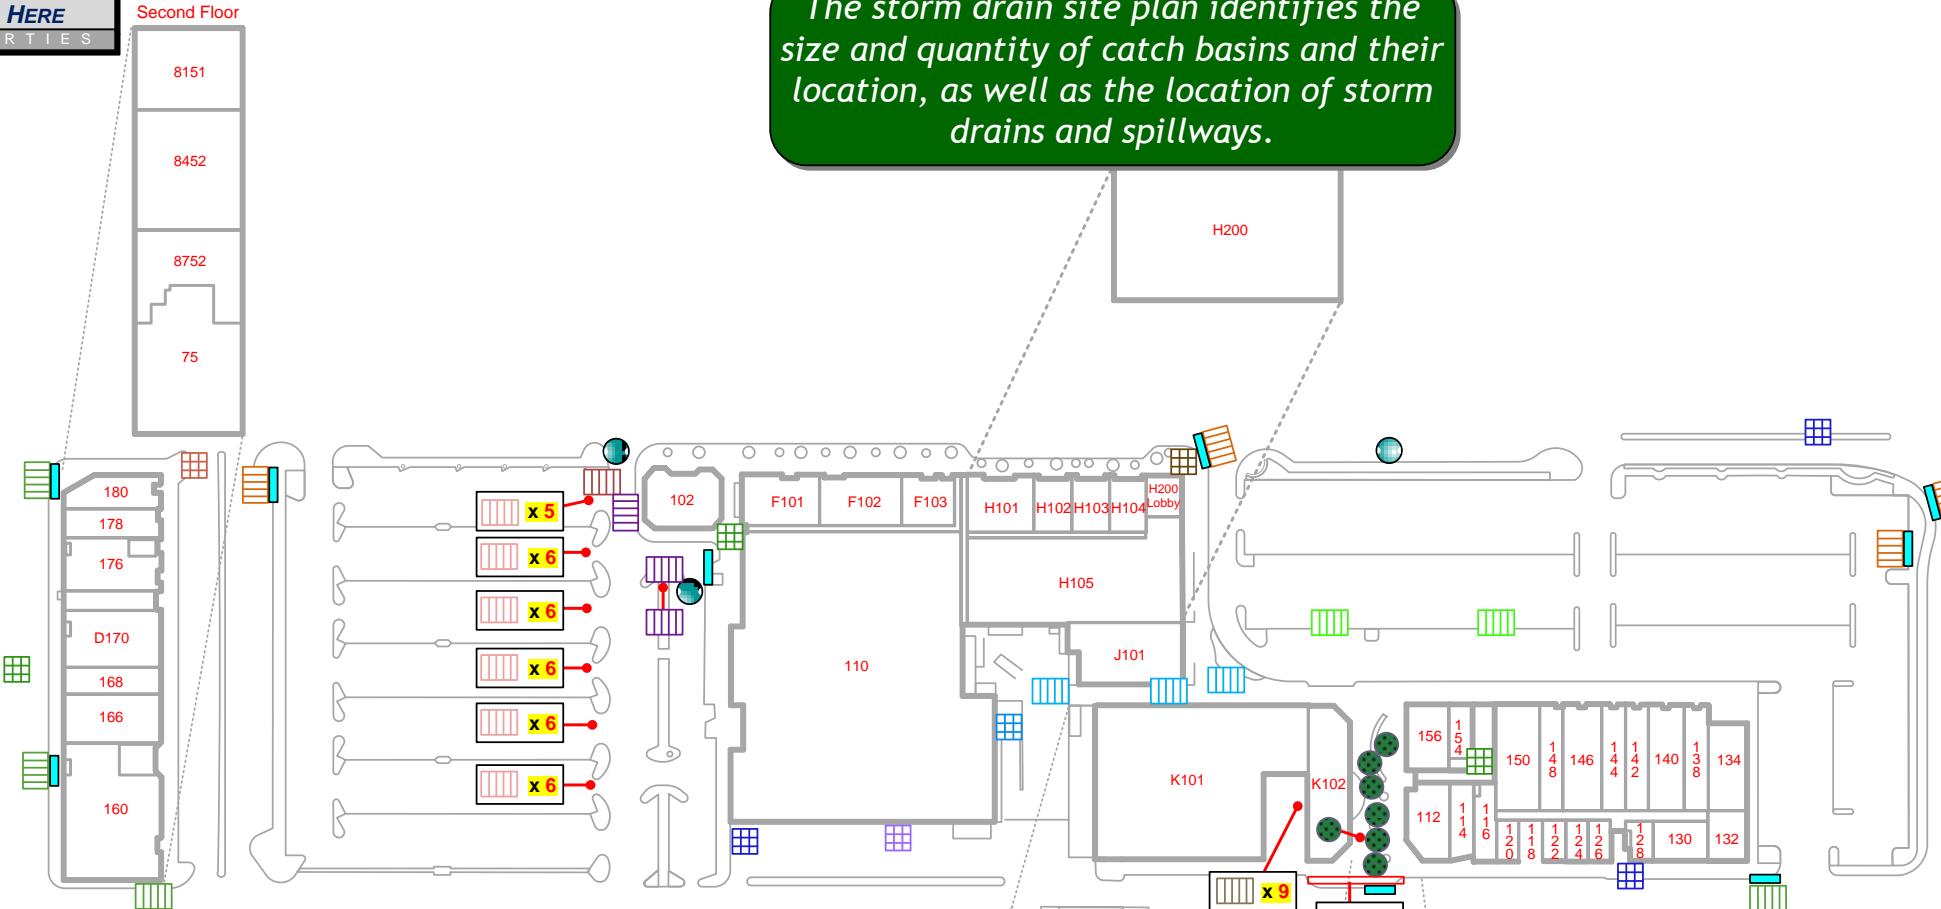

Plans produced by:
ID Plans Corp
05/10/2012
(813) 657-2545



© 2012

The water site plan identifies the location of water meters, the spaces they operate, the name of the tenant, and the meter numbers. It also identifies hose bibs, zurn fittings, sewer clean-outs, water shut-offs and back-flow preventers.


Water Meter Information							
Reference #	Space #	Tenant Name	Meter #	Reference #	Space #	Tenant Name	Meter #
1	220	YONG IN MARTIAL ARTS ACADEMY	49580741	36			NO METER
2	218	AVAILABLE	48971113	37			NO METER
3	214		57598208	38			NO METER
4	214	KING WAH RESTAURANT	64523738	39	028	BANANA ISLAND	59753467
5			NO METER	40	S106	GAMESTOP	38585903
6	212	KUMON LEARNING CENTER	50638213	41	022	DALY CITY OPTOMETRY/CLAIRES	44905021
7	208	BANGKOK GARDEN	57598089	42		OFF	1646809
8	204	US POST OFFICE	57267545	43	032	HOLLYWOOD VIDEO	50403834
9	202	MANNY'S HAIRCUT	52414015	44	034	PARTY WAREHOUSE	86874358
10	200	GENESIS DENTAL	47732567	45	038	BEVERLY'S	44662680
11			NO METER	46		UPPER LEVEL 418	30028290
12	A198	H&R BLOCK	47122925	47	S103	AVAILABLE	NO METER
13	196	TIMES SALON	57598145	48	S104	AVON	31127814
14	194	SUBWAY	53779376	49		LABELED 474A-494	68340831
15	192	QUICKLY	57267544	50	050	DSW SHOES	66071016
16			NO METER	51		OFF	3617020
17	188	WESTLAKE COIN LAUNDRY	43304100	52			48971196
18	186	ARCO	07091101	53	043	GEORGETTE'S OF WESTLAKE	44581204
19	185	BURLINGTON COAT FACTORY	53873473	54	045	SLIDER'S DINER	41647626
20	0U0	HOME DEPOT	4905936	55	R104	WESTLAKE VISION CENTER/VISION CENTER OPTOMETRY	50403842
21	T101	SHENG KEE BAKERY	20891	56			NO METER
22	T102	AVAILABLE	NO METER	57		PUBLIC BATHROOMS	53490998
23	T103	AVAILABLE	NO METER	58	046	BASKIN ROBBINS	3617020
24	T104	KICK CITY	18107473	59	044	DAPHNES GREEK CAFÉ	16904938
25	T105	LOBELLA	18107476	60	R103A	JAMBA JUICE	65469513
26	T106	DAI ICHI	18107474	61	R101	STARBUCKS	18260591
27	T107	YOGURT CIRCLE	69572289	62	055	WALGREENS	62177065
28		IRRIGATION	1565716	63	057	GNC	62177068
29	W101	MASSAGE ENVY SPA	18411789	64	P101	TJ MAXX	68091904
30	W102	WESTLAKE NAIL SPA	24414	65			4905989
31	W103	AVAILABLE	NO METER	66	HOUSE	MASTER SERVES OUO, 110, 120, F101-103, H101-105, H200, J101, K102, T101-107, S104, IRRIGATION HIGH FLOW)	07070211
32	W104	AVAILABLE	000)4310				
33	W106	LITTLE FIRE POT	66796838	67	HOUSE	MASTER SERVES OUO, 110, 120, F101-103, H101-105, H200, J101, K102, T101-107, S104, IRRIGATION	57158183
34			NO METER				
35	S101	FURNITURE GALLERY	46247477				

Plans produced by:
ID Plans Corp
05/10/2012
(813) 657-2545




© 2012




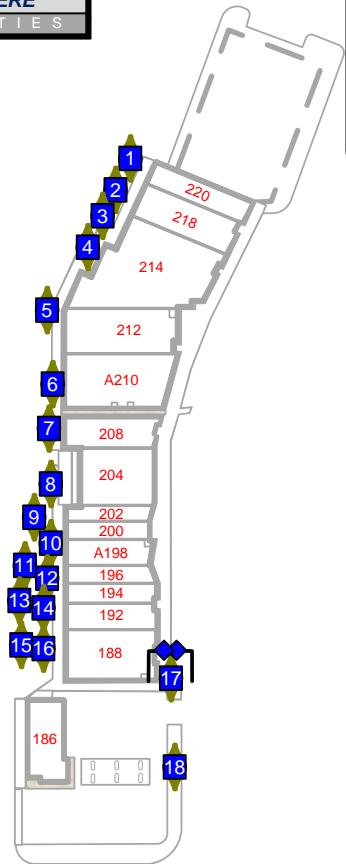

The water site plan identifies the location of water meters, the spaces they operate, the name of the tenant, and the meter numbers. It also identifies hose bibs, zurn fittings, sewer clean-outs, water shut-offs and back-flow preventers.

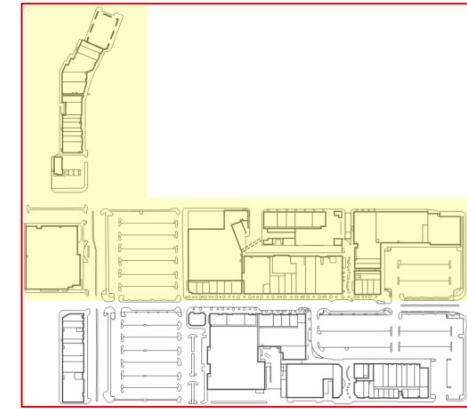

Water	
Page 2 of 7	
	1" Backflow Preventer
	2" Backflow Preventer
	4" Backflow Preventer
	Hot Bag
	House Water Meter with Number
	Sub Water Meter
	Tenant Water Meter with Number

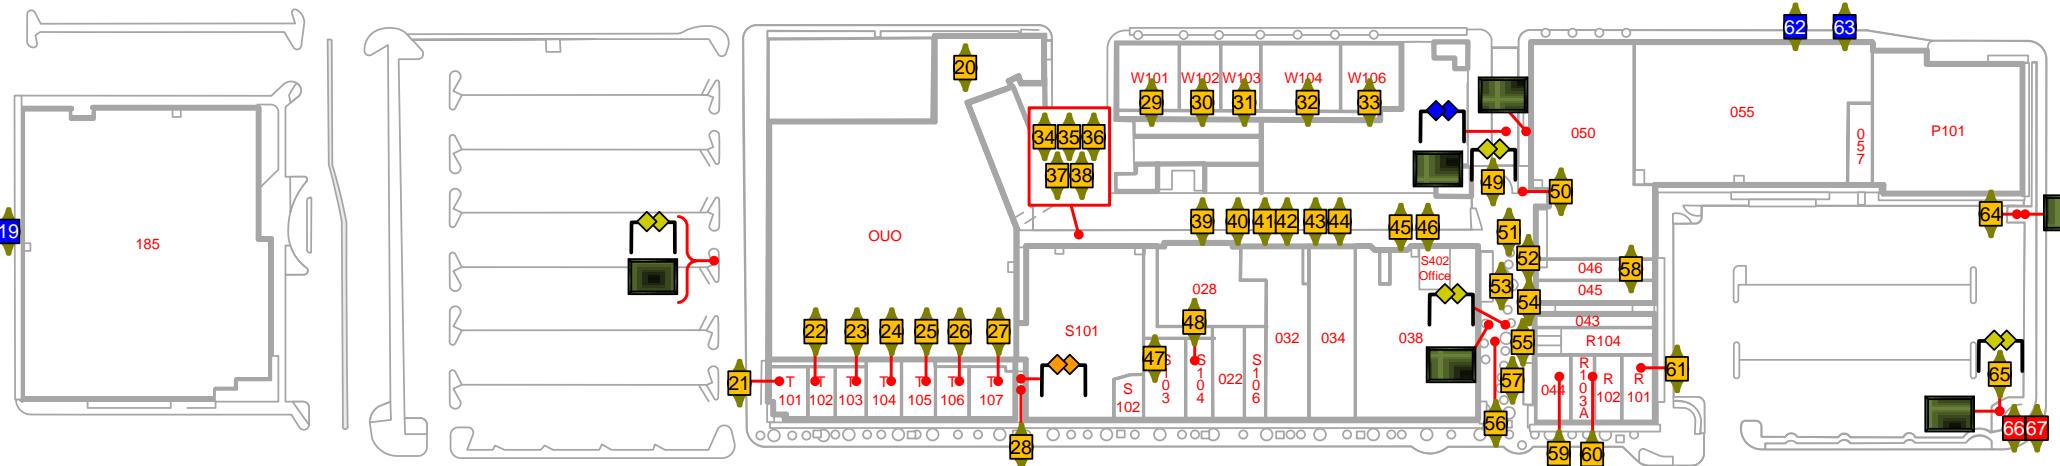

Plans produced by:
ID Plans Corp
05/10/2012
(813) 657-2545



© 2012

The water site plan identifies the location of water meters, the spaces they operate, the name of the tenant, and the meter numbers. It also identifies hose bibs, zurn fittings, sewer clean-outs, water shut-offs and back-flow preventers.

Water Meter Information							
Reference #	Space #	Tenant Name	Meter #	Reference #	Space #	Tenant Name	Meter #
68	75	2ND FLOOR	48348146	99	K102	SLEEP TRAIN	65712768
69	178	PHO HUYNH HIEP 3	48971128	100		UPPER LEVELS	1478218
70	180	US BANK	09319664	101		UPPER LEVELS	4075004
71	176	PATELCO CREDIT UNION	62697266	102		UPPER LEVELS	10704263
72	D170	BANK OF AMERICA	57875522	103	156	WESTLAKE COFFEE SHOP	57075493
73	8452	SETON MEDICAL CENTE	66369181	104	154	WESTLAKE HEARING AID CENTER	57569833
74	168	TOKYO TERIYAKI JAPANESE CUISINE	57151029	105	116	STRUCTURE HAIR DESIGN	57075491
75	166	HSBC	44652977	106	112	WESTLAKE LIQUORS	(000)20
76	8151	KAISER PERMANENTE HEARING CENTER	49061590	107	114	CIGARETTES "R" CHEAPER	(000)16
77	160	CHASE	57598142	108	120	WESTLAKE SHOE REPAIR	57569839
78	160	CHASE	62063213	109	146	BANK OF THE WEST	57569840
79	HOUSE	MASTER SERVES 022-050, P101, R101-104, W101-106 (HIGH FLOW)	07075798	110	118	WESTLAKE ART GALLERY	57569838
80	HOUSE	MASTER SERVES 022-050, P101, R101-104, W101-106	07769705	111	144	THE UPS STORE	57569841
81			39094387	112	122	PULIDO'S TAILOR	57569837
82			4905641	113	148	BROASTER CHICKEN	56318341
83			05249279	114	124	MAGIC TOUCH BEAUTY SALON	57569835
84	102	88 RICE BOWL	57104109	115	150	T-MOBILE	56346767
85	F101	KANA JAPANESE CUISINE	3387725	116	126	TANI'S KITCHEN	57569836
86	F102	GERRY'S GRILL	4905642	117		WESTLAKE CLEANERS	57075494
87	F103	BURGERMEISTERS HAMBURGERS	3367724	118	HOUSE	MASTER SERVES 112-156, UPPER LEVELS	1261478
88	F103	BURGERMEISTERS HAMBURGERS	4906051	119	134	CHIPOLTE MEXICAN GRILL	68472275
89	H101	VERIZON WIRELESS	61157331	120		NO METER	
90	H102	GOOD FEET	65376351	121		OFF	39940013
91	H103	COLOR ME MINE	65376353	122		OFF	39331576
92	H104	MIKI	65376354	123	140	RADIO SHACK	39218233
93	110	SAFEWAY	19913692	124	138	SUPERCUTS	39218235
94	H105	TRADER JOE'S	T103237	125	132	NATION'S GIANT HAMBURGERS	97547281
95	H200/H105	COST PLUS WORLD MARKET/TRADER JOE'S	60320799	126	142	RED WING SHOES	67488511
96	J101	SAN MATEO CREDIT UNION	65712767	127	128	ELITE HAIR SALON	39218231
97	H200	COST PLUS WORLD MARKET	60456160	128	130	DANCO REAL ESTATE	39331573
98	K101	ROSS DRESS FOR LESS	65712804				


Water Company: City Dept. of Public Works
Telephone Number: 888-225-5300

Plans produced by:
ID Plans Corp
05/10/2012
(813) 657-2545



© 2012




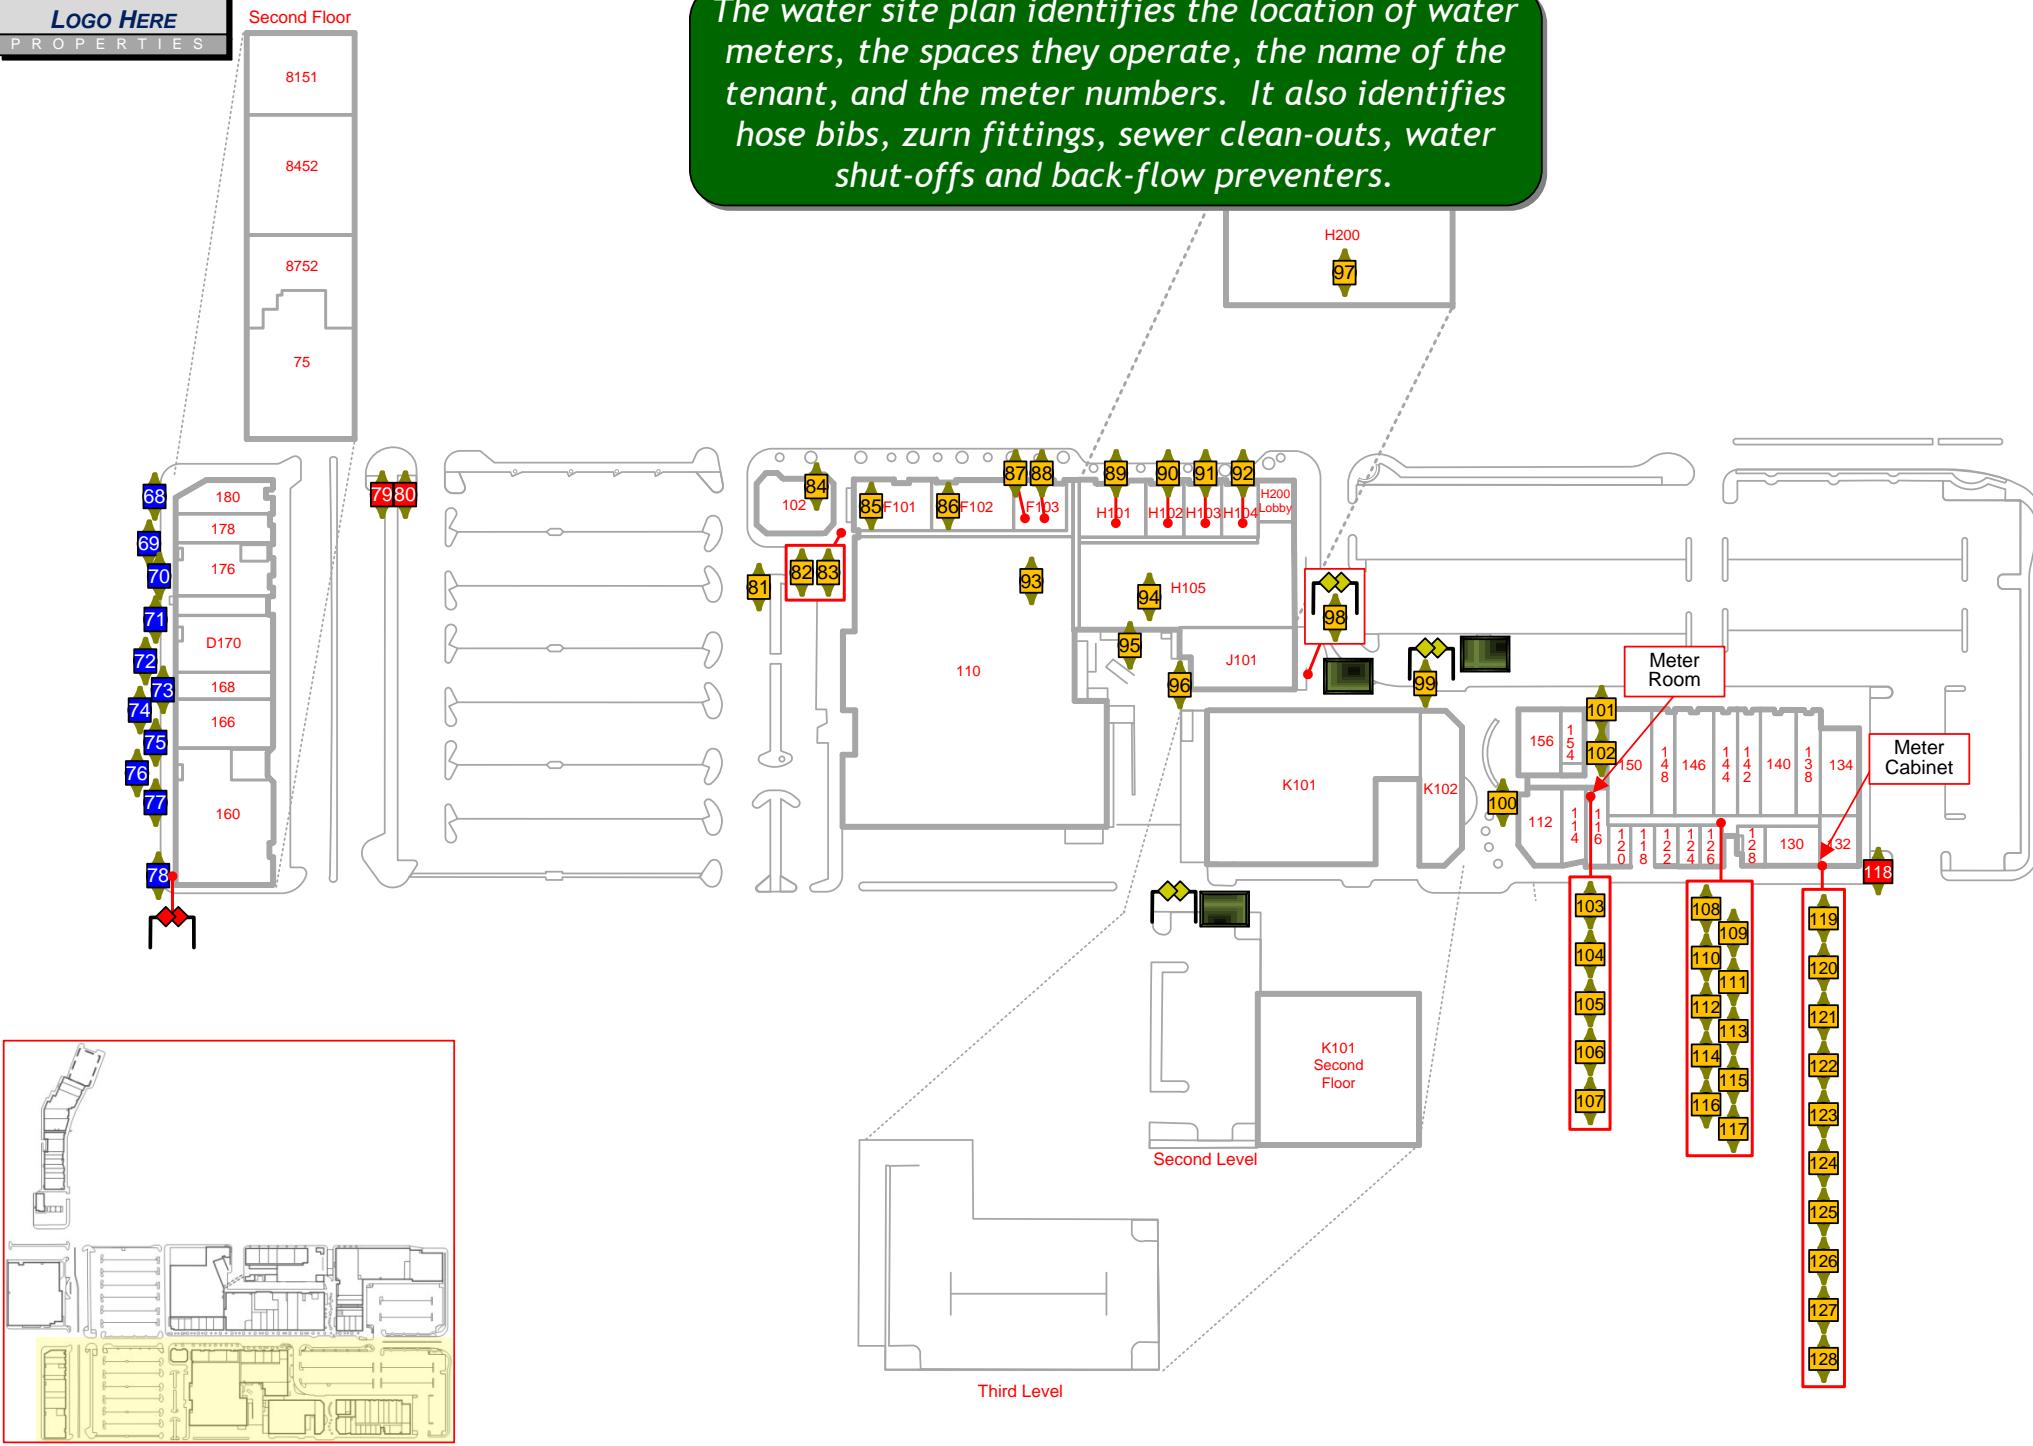


Plans produced by:
ID Plans Corp
05/10/2012
(813) 657-2545



© 2012

The water site plan identifies the location of water meters, the spaces they operate, the name of the tenant, and the meter numbers. It also identifies hose bibs, zurn fittings, sewer clean-outs, water shut-offs and back-flow preventers.

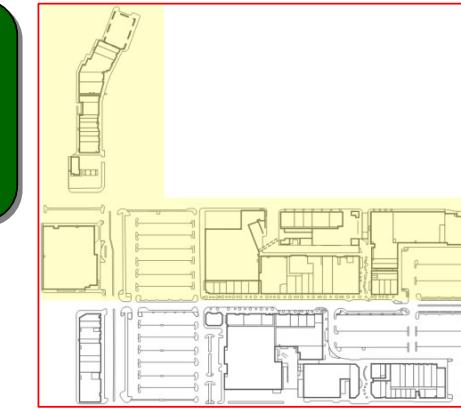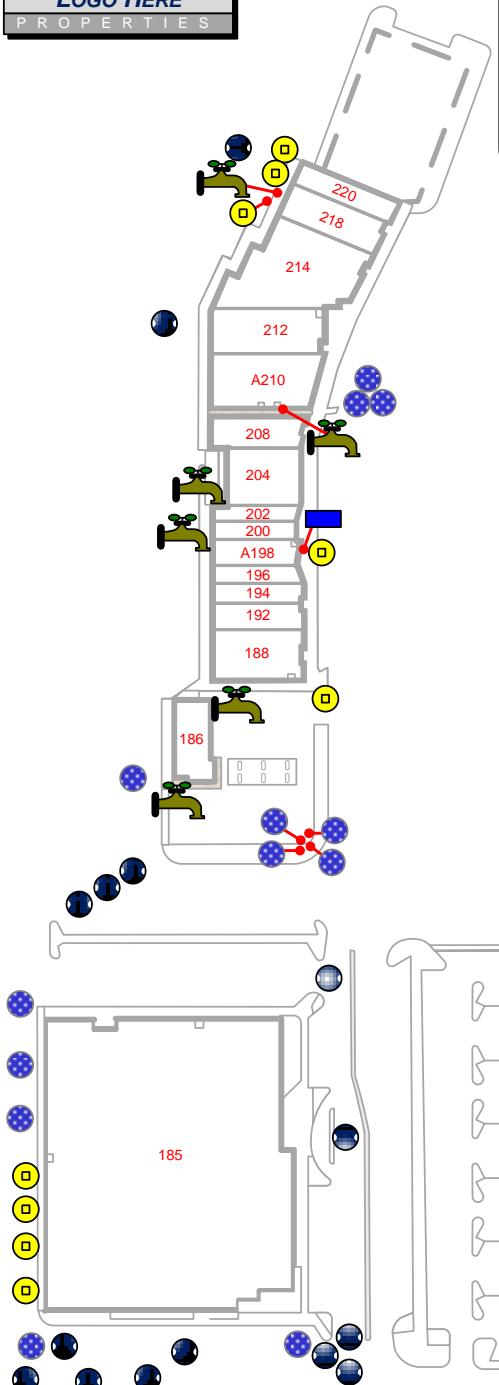


Water
Page 5 of 7

	Hose Bibb
	Inground Water Shutoff
	Sewer Cleanout
	Sewer Manhole Cover
	Zurn Hose Bibb


Plans produced by:
ID Plans Corp
05/10/2012
(813) 657-2545



© 2012

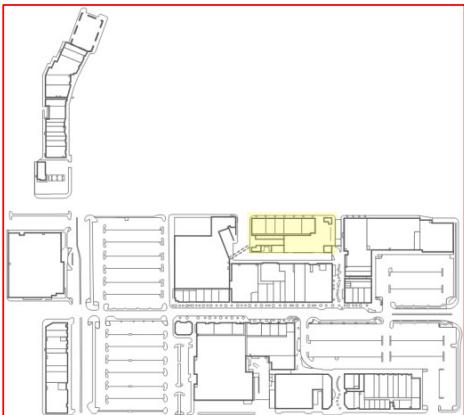

The water site plan identifies the location of water meters, the spaces they operate, the name of the tenant, and the meter numbers. It also identifies hose bibs, zurn fittings, sewer clean-outs, water shut-offs and back-flow preventers.

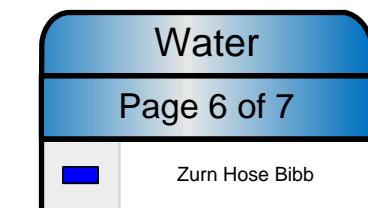

Fifth Level




Fourth Level



Third Level



Second Level

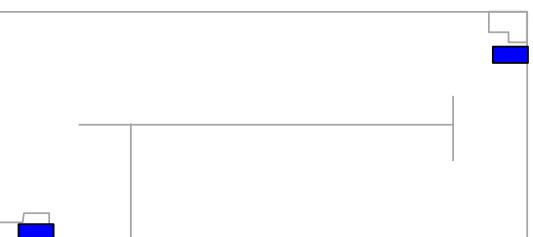

First Level

Plans produced by:
ID Plans Corp
05/10/2012
(813) 657-2545





© 2012



The water site plan identifies the location of water meters, the spaces they operate, the name of the tenant, and the meter numbers. It also identifies hose bibs, zurn fittings, sewer clean-outs, water shut-offs and back-flow preventers.

Water	
Page 7 of 7	
	Hose Bibb
	Inground Water Shutoff
	Sewer Cleanout
	Sewer Manhole Cover
	Zurn Hose Bibb

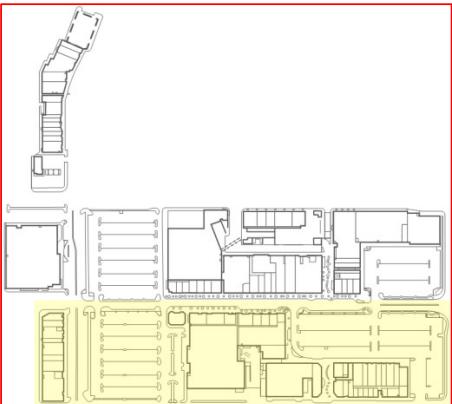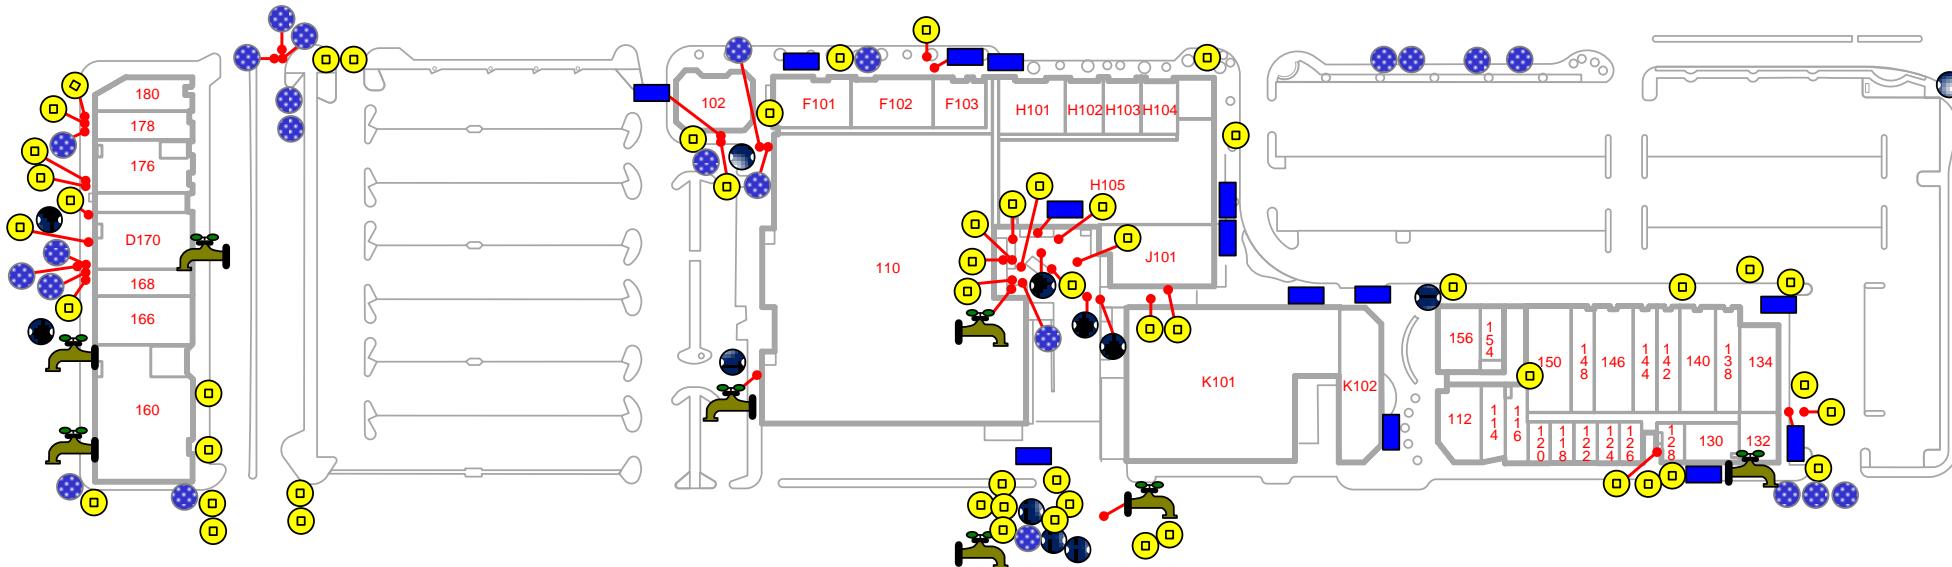

Plans produced by:
ID Plans Corp
05/10/2012
(813) 657-2545



© 2012